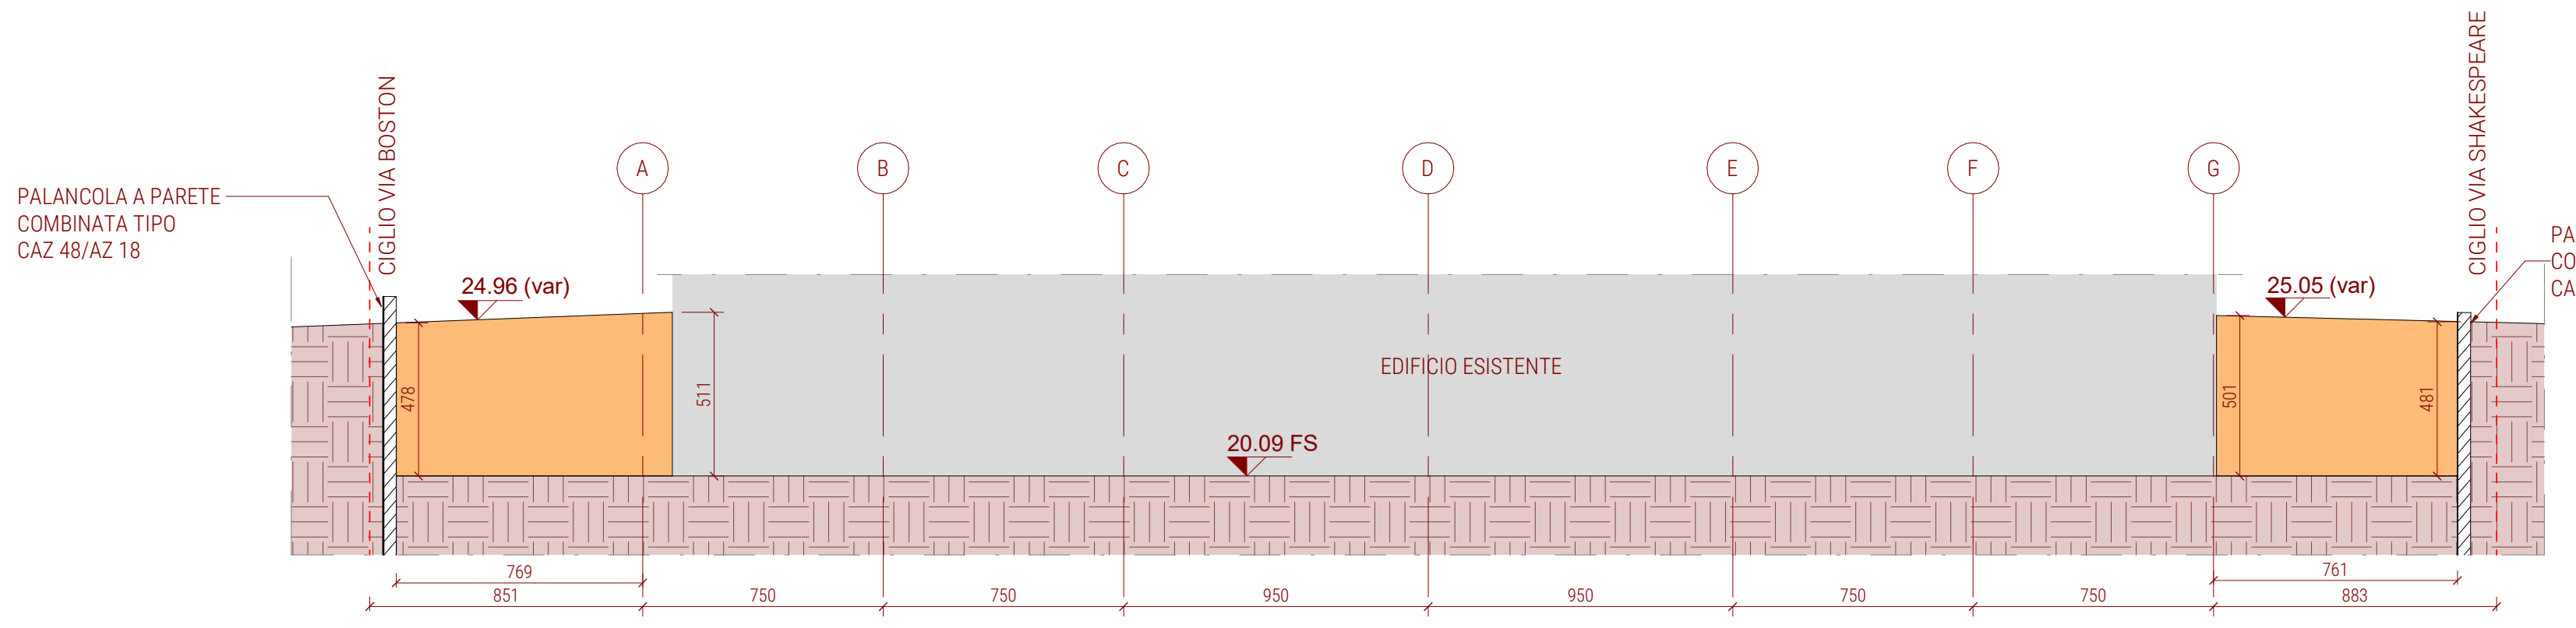

SEZIONE SCAVI SV2

1 : 200

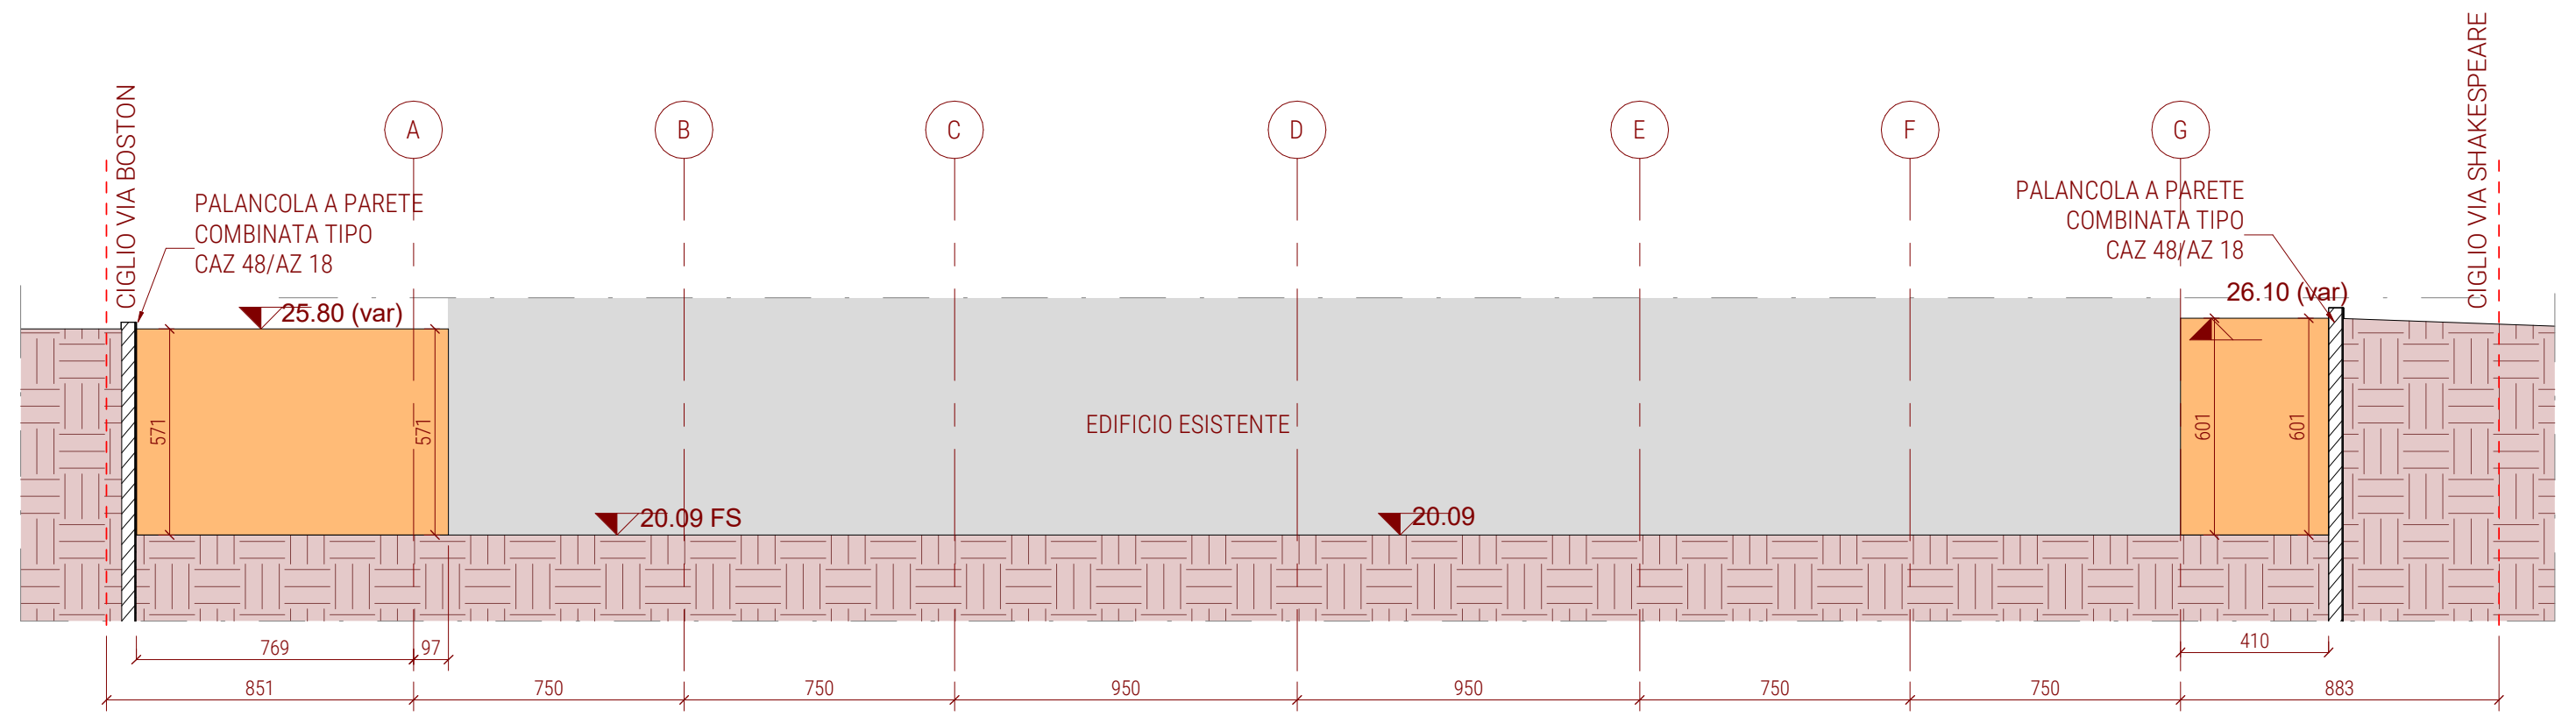

SEZIONE SCAVI SV1

1 : 200

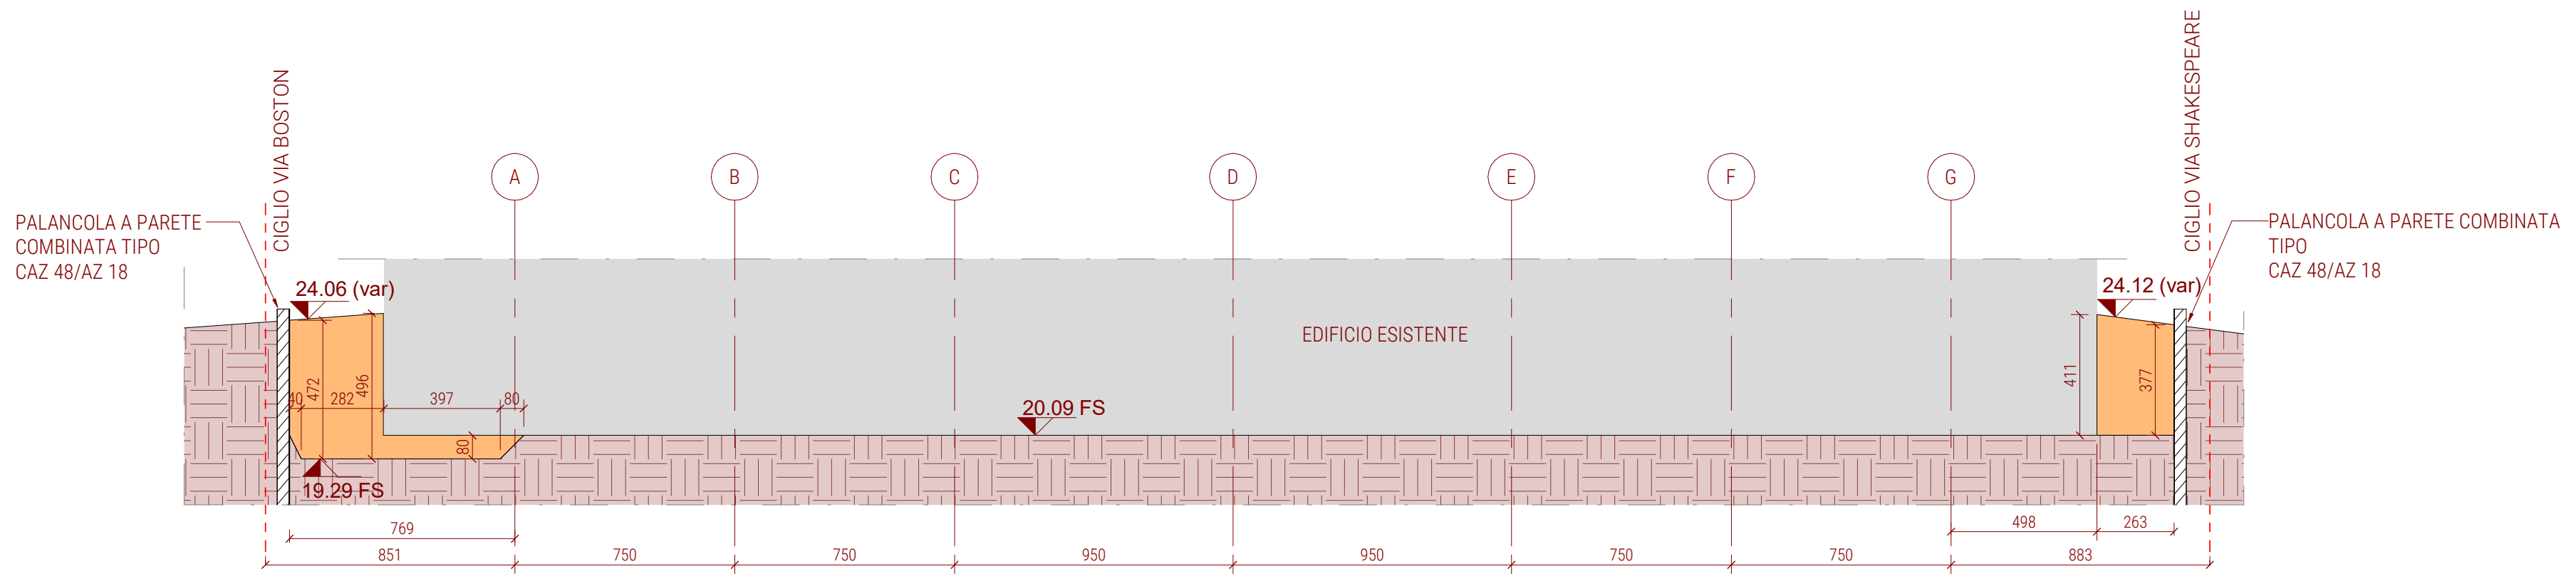

SEZIONE SCAVI SV3

1 : 200

FS = FONDO SCAVO

QUOTE ALTIMETRICE IN METRI s.l.m
OUOTA 0.00 DI PROGETTO CORRISPONDE A +25.40 s.l.m

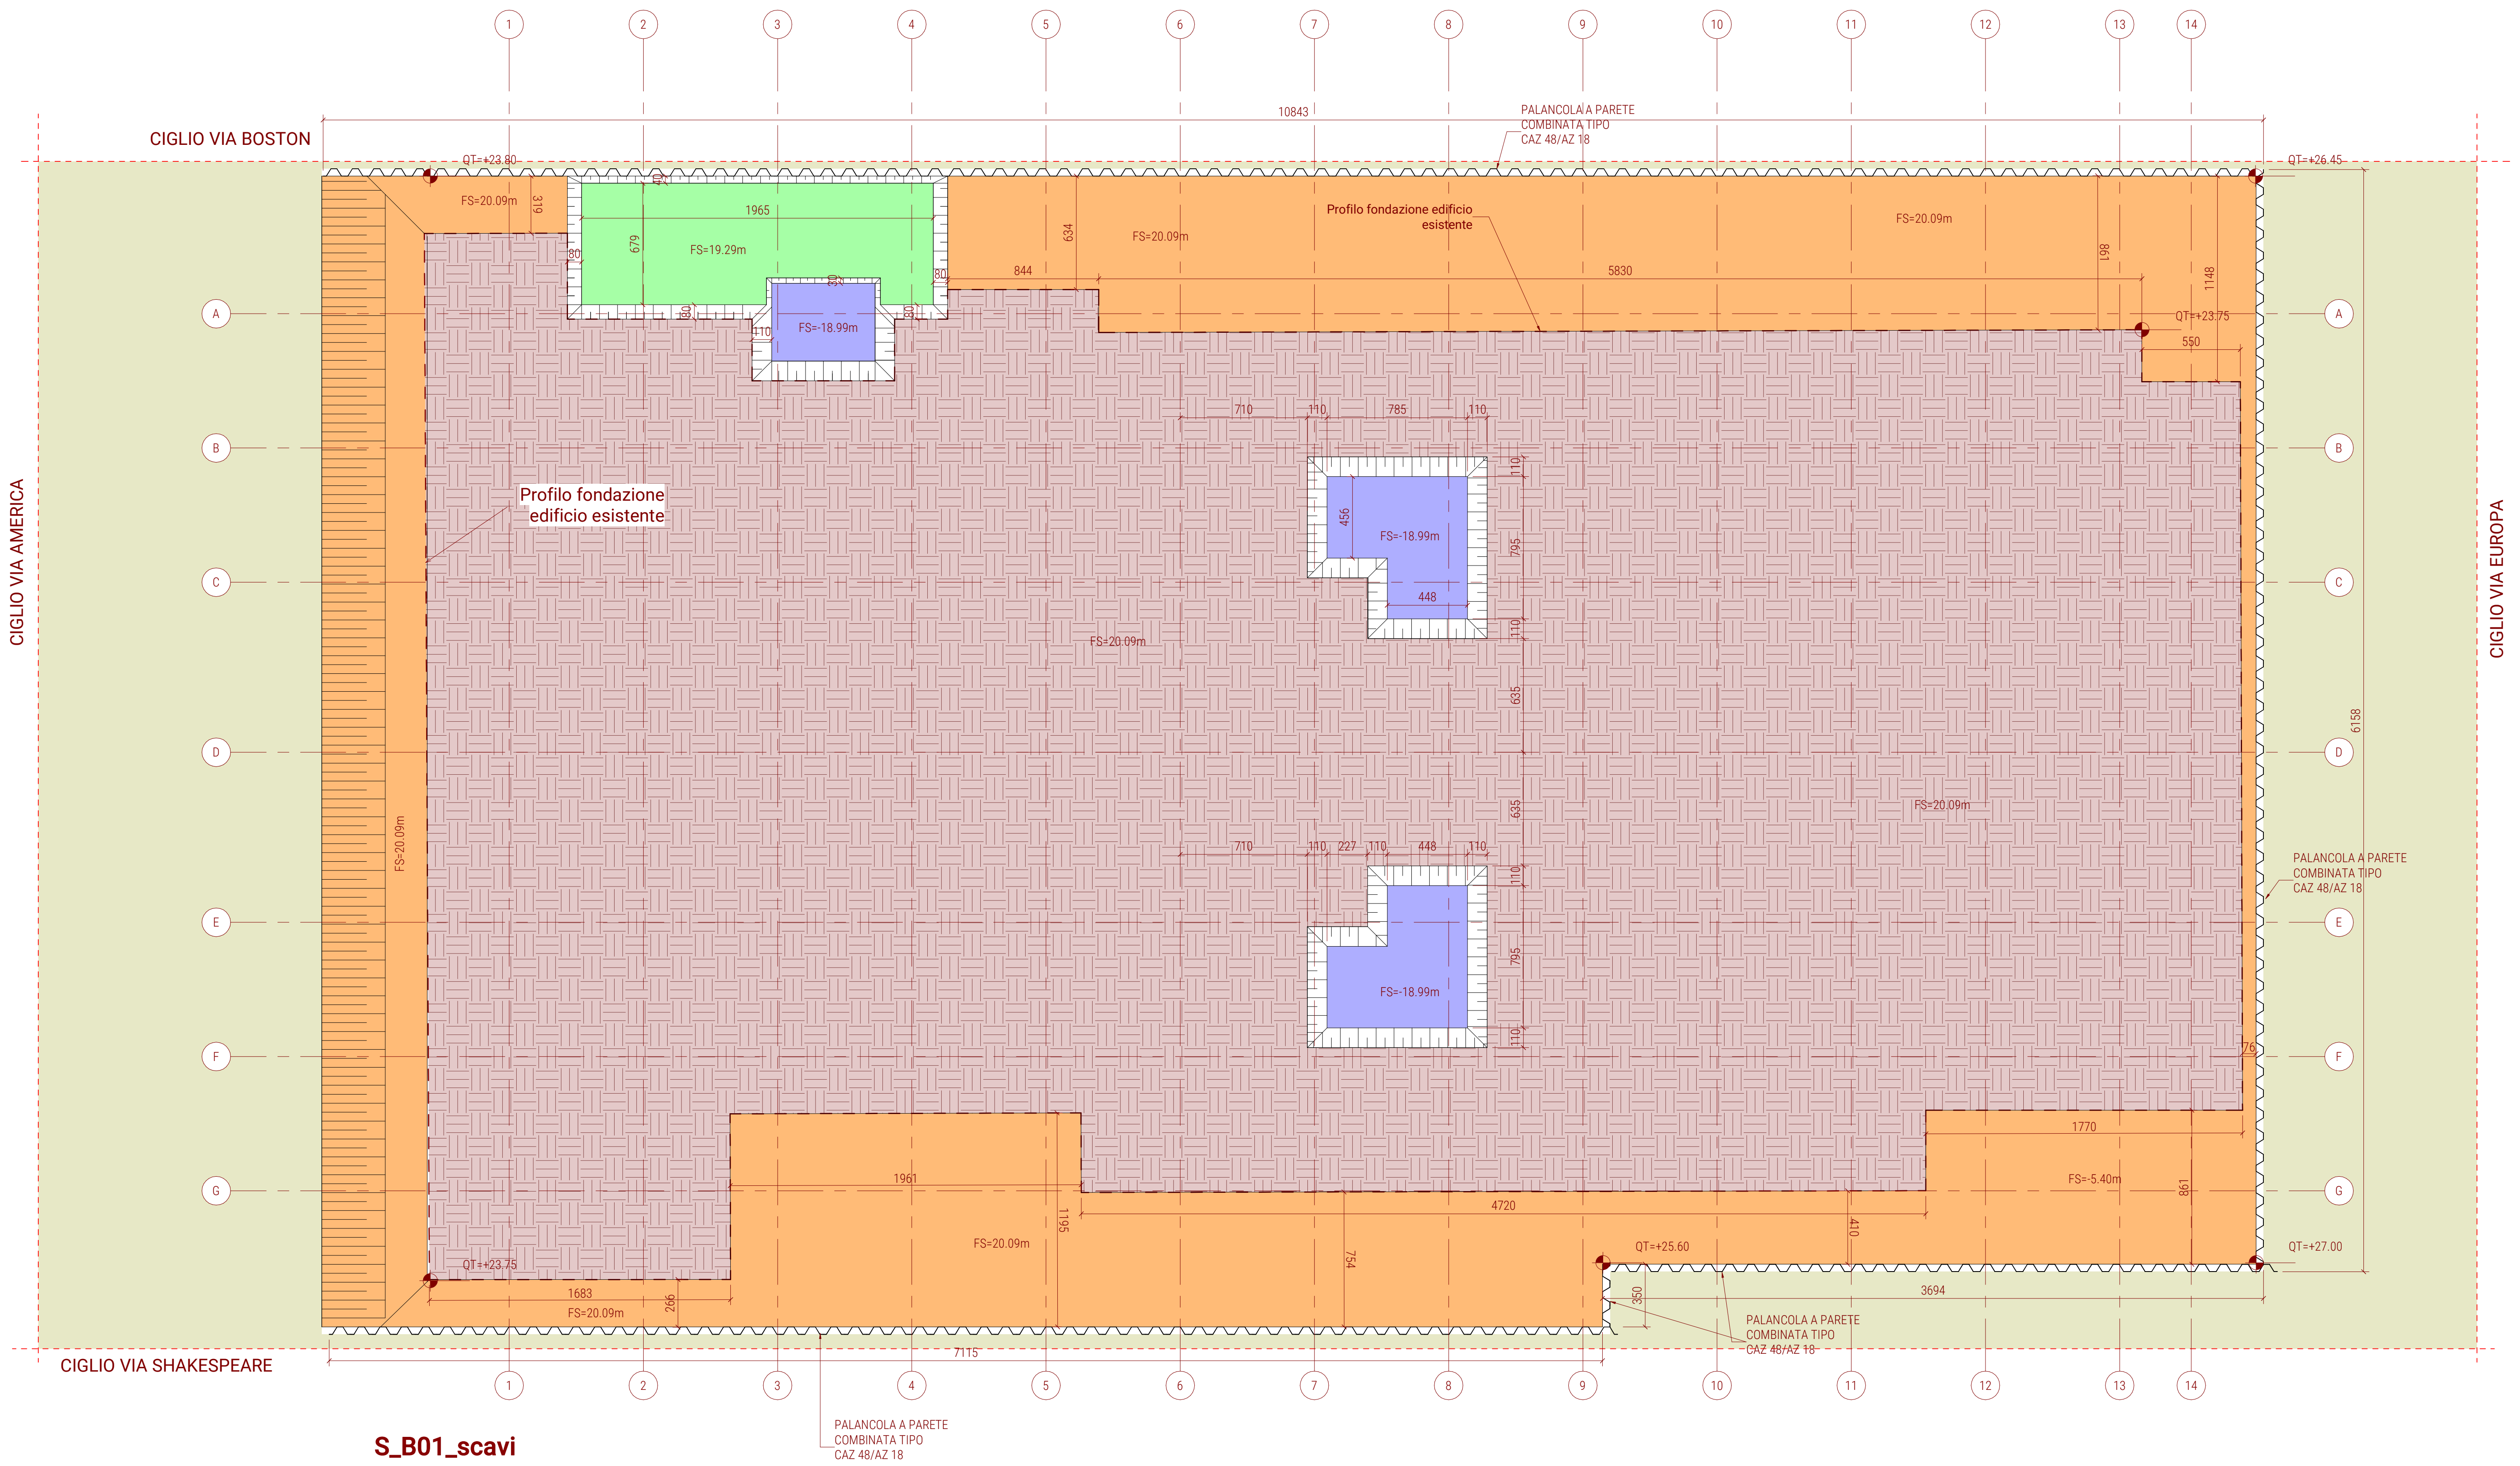

S_B01_scavi

1 : 200

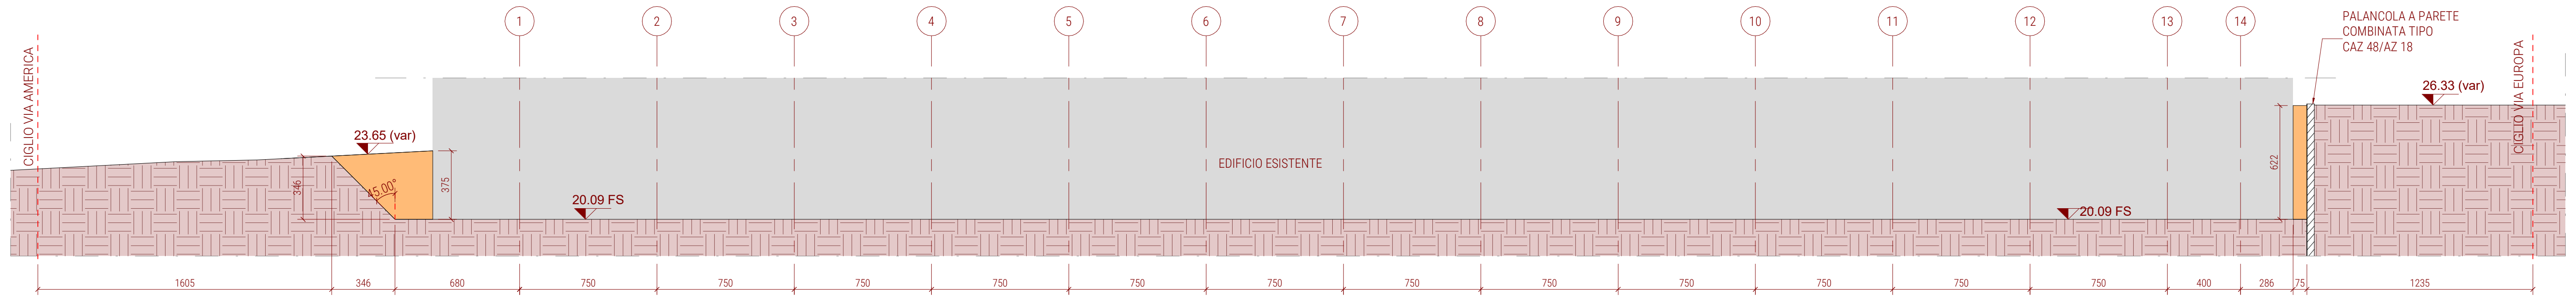

SEZIONE SCAVI SV4

1 : 200

SCHEDA MATERIALI

CALCESTRUZZO

PARTE D'OPERA	Classe Calcestruzzo (NTC 2018)	Classe di esposizione (UNI EN 206:2016)	Copriferro nominale	D_{MAX} Inerte	Classe di consistenza
Magrone	C 12/15	-	-	32 mm	S3
Pali fondazione	C 25/30	XC2	75 mm	20 mm	S4
Strutture fondazione	C 32/40	XC2	35 mm	20 mm	S4
Strutture in elevazione	C 32/40	XC3	35 mm	16 mm	S4
Solette	C 32/40	XC3	35 mm	16 mm	S4
Soletta completamento	C 32/40	XC3	30 mm	16 mm	S4

ACCIAIO PER CALCESTRUZZO

Classe di resistenza	Snervamento	Rottura	Specifiche	Caratteristiche e controlli
B 450 C	450 N/mm²	540 N/mm²	Barre ad aderenza migliorata saldabili	Secondo DM 17/01/2018

RESINA PER ANCORANTI CHIMICI

Tipo HILTI HIT-RE 500 V4 per ancoraggi su calcestruzzo

MALTA DI LIVELLAMENTO

Malta di livellamento espansiva antiritiro tipo "Masterflow" S55

STRUTTURE IN XLAM E TAVOLATO

Classe di resistenza C24

LEGNO LAMELLARE

Classe di resistenza	Resistenza a flessione	Resistenza a taglio	Resistenza a trazione parallela	Resistenza a trazione perpendicolare
GL24h Travi e Pilastri	24 N/mm²	3.5 N/mm²	19.2 N/mm²	0.5 N/mm²
GL28h Travetti e Travi cop.	28 N/mm²	3.5 N/mm²	22.3 N/mm²	0.5 N/mm²

PIOLATURE

Connettore tipo Tecnaria CLT MAXI 080 per solai in legno

Connettore tipo Tecnaria CTF 040 per solai in acciaio

CONVENZIONI PER PIEGATURE SOVRAPPOSIZIONI E COPRIFERRO

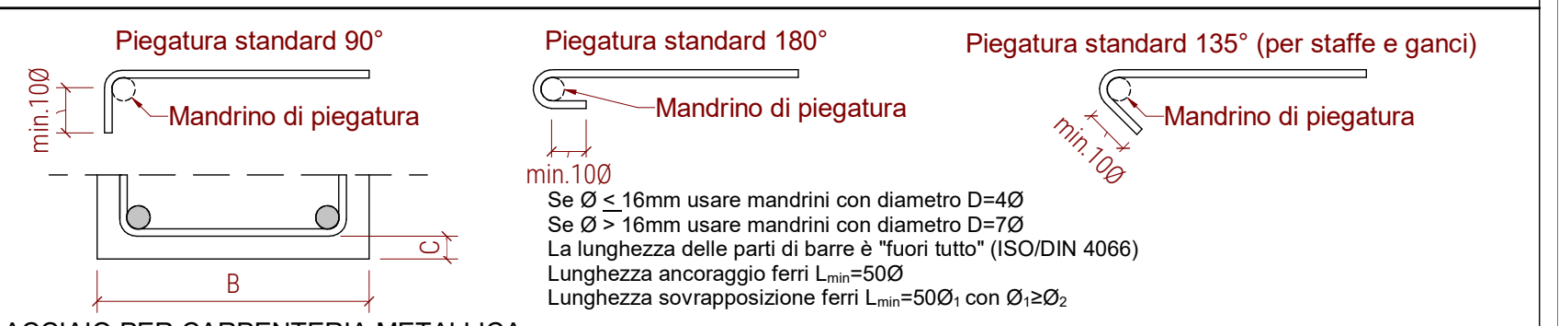

Se Ø ≤ 16mm usare mandrini con diametro D=4Ø
Se Ø > 16mm usare mandrini con diametro D=7Ø
La lunghezza delle parti di barre è "fuori tutto" (ISO/DIN 4066)
Lunghezza ancoraggio ferri L_{min}=50Ø
Lunghezza sovrapposizione ferri L_{min}=50Ø$_1$ con Ø$_1$≥Ø$_2$

ACCIAIO PER CARPENTERIA METALLICA

Classe di resistenza	Snervamento	Rottura	Classe di esecuzione	Caratteristiche e controlli
S 355	355 N/mm²	510 N/mm²	EXC3	Secondo DM 17/01/2018

UNIONI CARPENTERIA METALLICA

ELEMENTO	Classe di resistenza
Bulloni e tirafondi	8.8
Dadi	8.8
Rondelle	C50

La coppia di serraggio è quella indicata sulle targhette delle confezioni, nel caso non sia riportata ma compaia il solo fattore k secondo la classe funzionale pari a:

$$M = k \times d \times 0.7 \times A_{res} \times f_{tb}$$

con d=il diametro nominale della vite; A_{res} è l'area resistente della vite; f_{tb} è la resistenza ultima a trazione del bullone.
Viti, dadi e rondelle dovranno essere forniti dal medesimo produttore;

SALDATURE

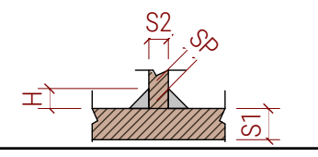

Le saldature eseguite in cantiere dovranno essere sottoposte a procedure di verifica da parte di istituto certificato

Salvo dove diversamente indicato le saldature sono a CORDONE D'ANGOLO secondo la seguente regola:
S1≥ S2
H= S2
Sp=0.7xH

AVVERTENZE E NOTE

Strutture metalliche di piano e copertura con relative unioni zincate.
Strutture metalliche interne protette mediante intonaco intumescente per protezione al fuoco R60.
Le strutture in cemento armato dell'interrato e in elevazione sono R120, le strutture in legno sono R60.
Quote altimetriche in m.
Quote strutturali in cm salvo dove diversamente indicato.
Verificare quote e dimensioni in cantiere.
Orditura solai di piano indicata a pavimento di piano.
Profilati tubolari laminati a caldo secondo UNI EN 10210.

APPROVAZIONE COMMITTENTE	
	A - APPROVATO
	B - APPROVATO CON COMMENTI
	C - NON APPROVATO

Rev.	Data	Descriz.	Red.	Ver.	App.
0	05/10/2026	Emissione	GPA	GO	PS

SCALA	SEDE PROGETTO	NUMERO PROGETTO
1:200	VIALE BOSTON 25 Comune di ROMA, RM - 00144	RMB1284

STATO
P

FASE PROGETTUALE:
PFTE

RTP:

Mandataria:
Progetto strutturale
via Leone X 3
50129 Firenze
+39 055 468291
info@gpapartners.com

Mandante:
Progetto architettonico
The White Chapel Building, 10
Whitechapel High Street Londra, E1 8QS,
United Kingdom
+44 (0)20 3006 3900
info@plparchitecture.com

Mandante:
Progetto architettonico
Via San Vito, 26
20123 Milano, Italia
+39 328 841 0677
office@oblyk.studio

Mandante:
Progetto impianti
Via Cavour, 4
70027 Palo del Colle (BA)
+39 080 8594347
info@studioperillo.eu

Mandante:
Responsabile progettazione sostenibile dell'oopera
Via Giuseppe Verdi, 26
63822 Porto San Giorgio (FM)
+39 0734674423
info@valentiniarchitetture.com

Mandante:
Via Beccarini, 29
48018 Faenza (RA)
+39 0546663423
ingegneria@enser.it

PROGETTO: CIG: B4C1AD81FA CUP: G84H22000360001

Realizzazione della nuova sede del Ministero dell'Ambiente e della Sicurezza Energetica
“MASE”

Codice bene: RMB1284
Codice fabbricato: RM0411001

TITOLO

PIANTA DEGLI SCAVI

AGENZIA DEL DEMANIO
Struttura per la progettazione
Via Barberini 38, 00187, Roma
RUP: Arch. Isabella Di Marsico
DEC: Ing. Benedetto Grivo

NOME FILE
RMB1284-ADD-PLANGENER-XX-DR-S-PN0002

REV
0
05/10/2026