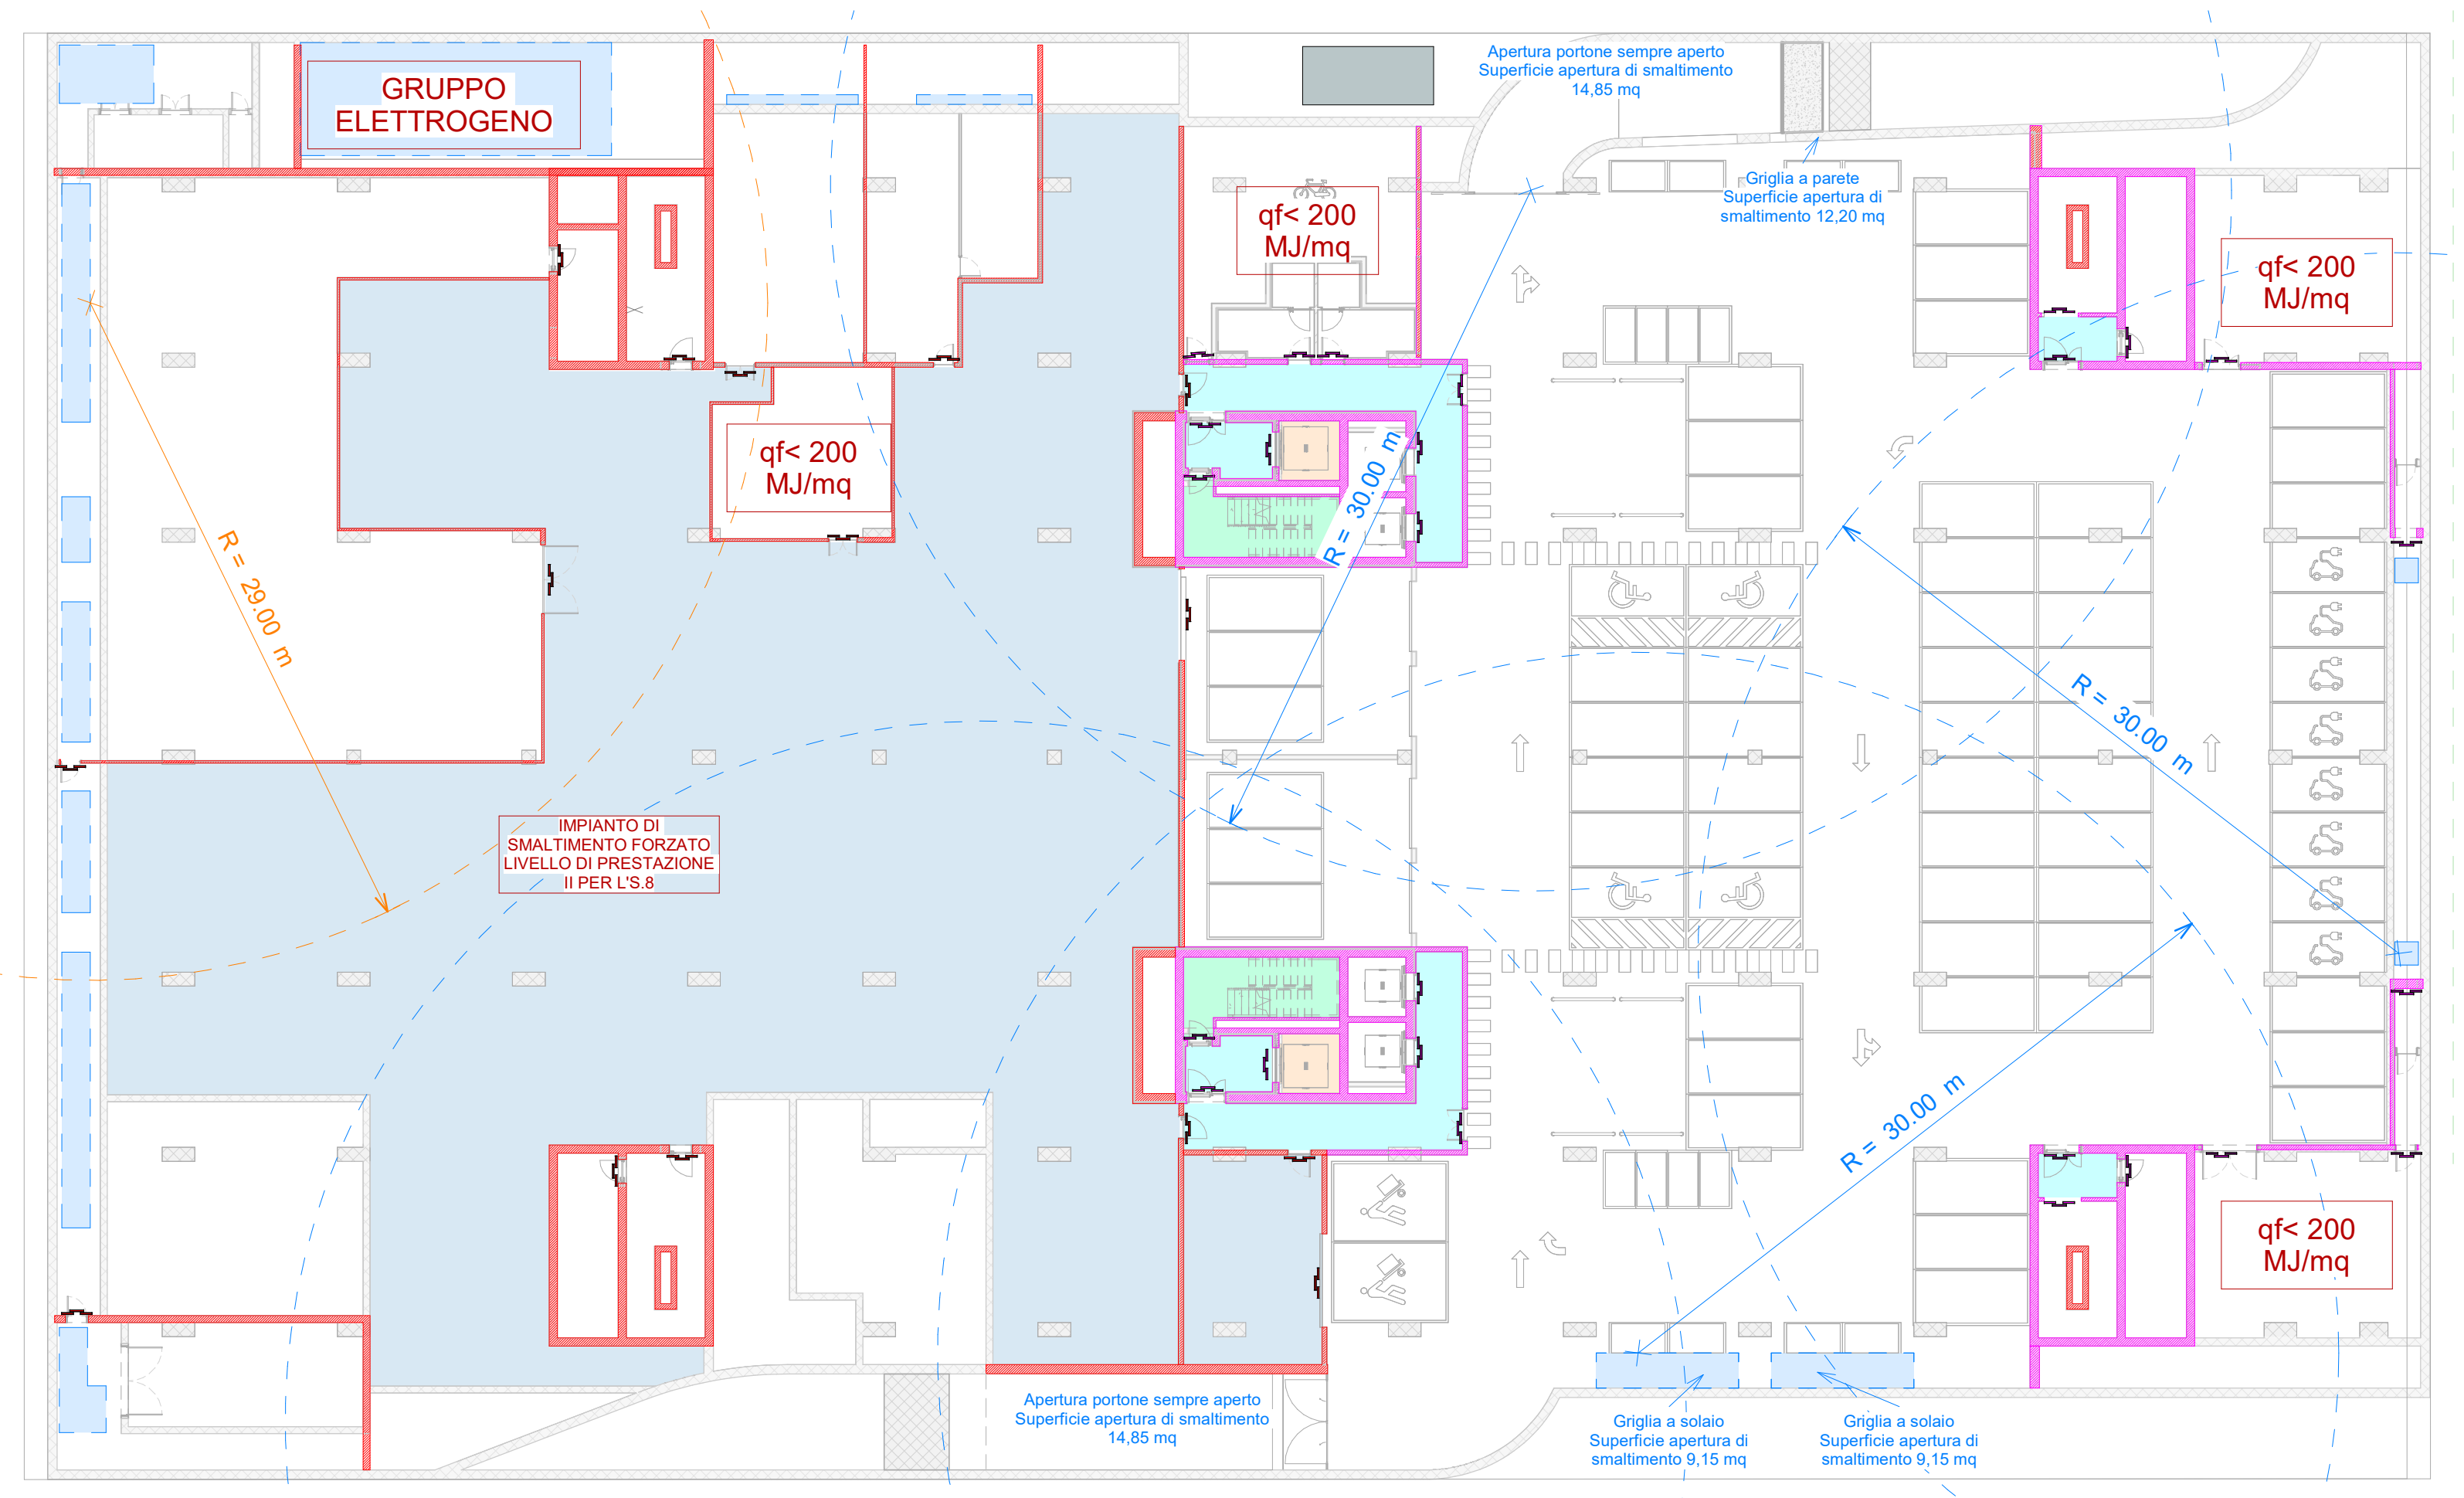
GRUPPO ELETTROGENO
qf< 200 MJ/mq
qf< 200 MJ/mq
qf< 200 MJ/mq
qf< 200 MJ/mq
R = 29.00 m
R = 30.00 m
R = 30.00 m
R = 30.00 m
IMPIANTO DI SMALTIMENTO FORZATO LIVELLO DI PRESTAZIONE II PER L'S.8
Apertura portone sempre aperto Superficie apertura di smaltimento 14,85 mq
Griglia a parete Superficie apertura di smaltimento 12,20 mq
Apertura portone sempre aperto Superficie apertura di smaltimento 14,85 mq
Griglia a solaio Superficie apertura di smaltimento 9,15 mq
Griglia a solaio Superficie apertura di smaltimento 9,15 mq

Piano interrato - Aperture di smaltimento - Scala 1 : 250

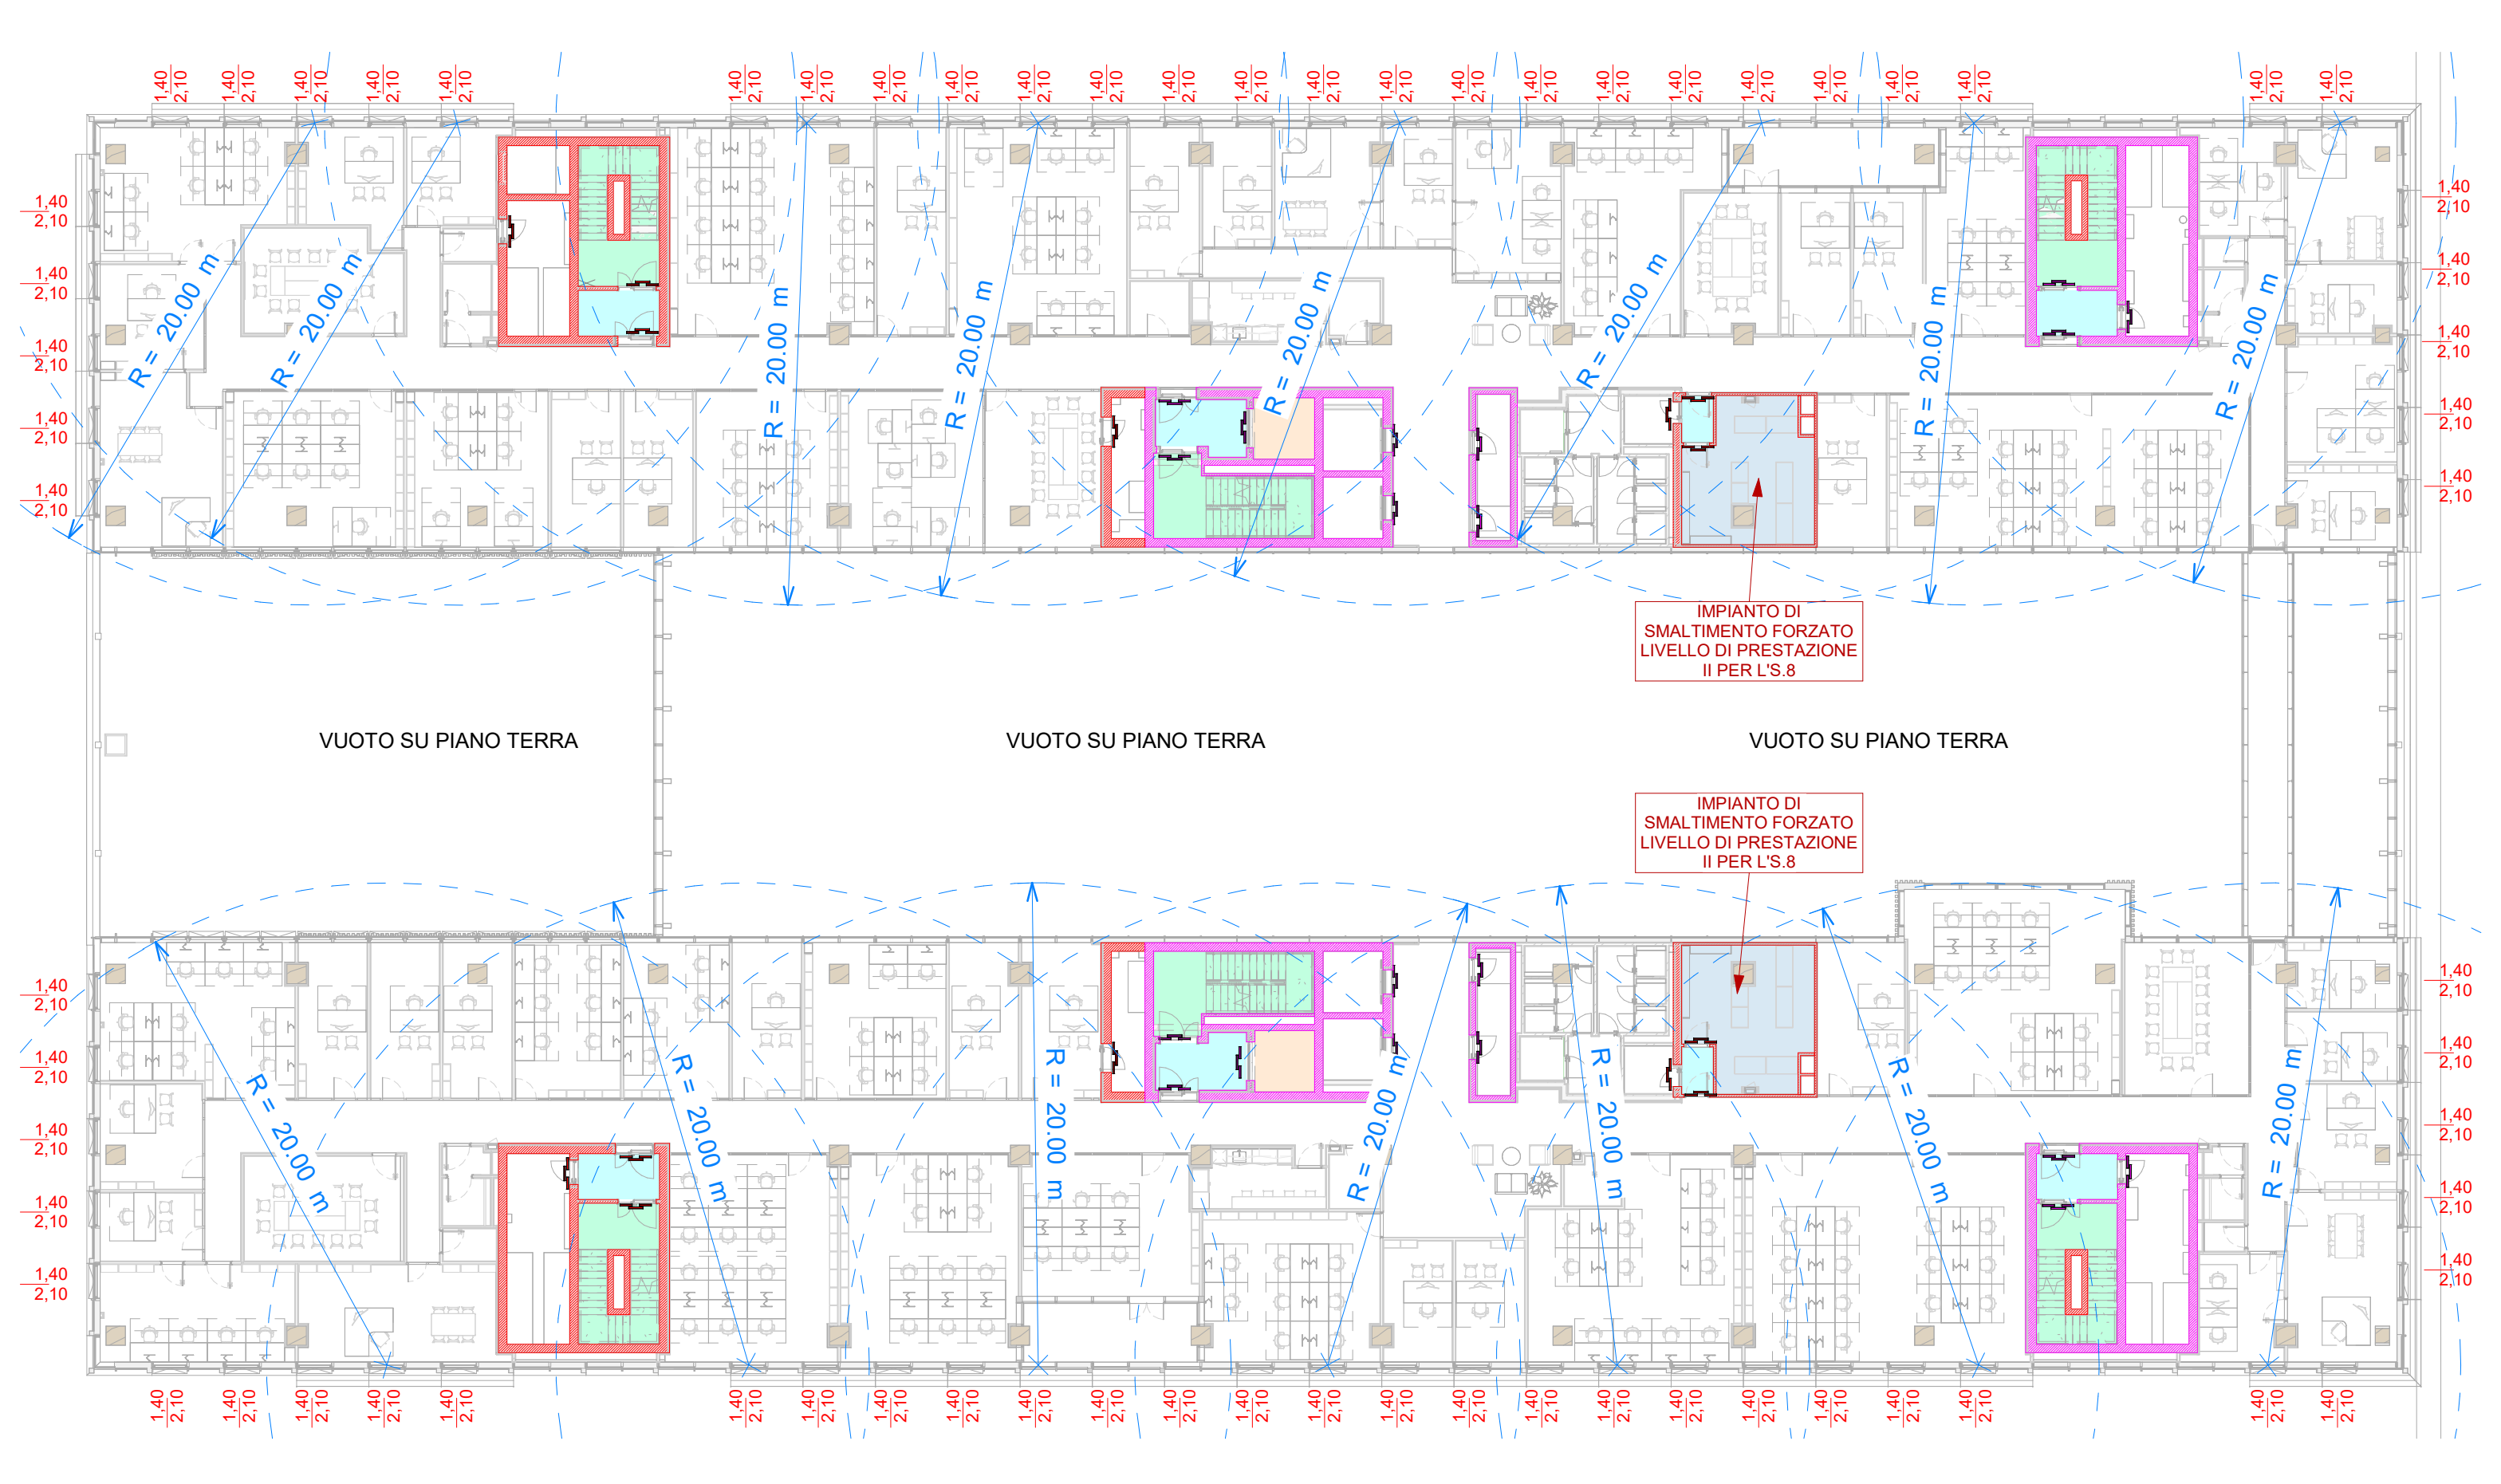

Piano secondo - Aperture di smaltimento - Scala 1 : 250

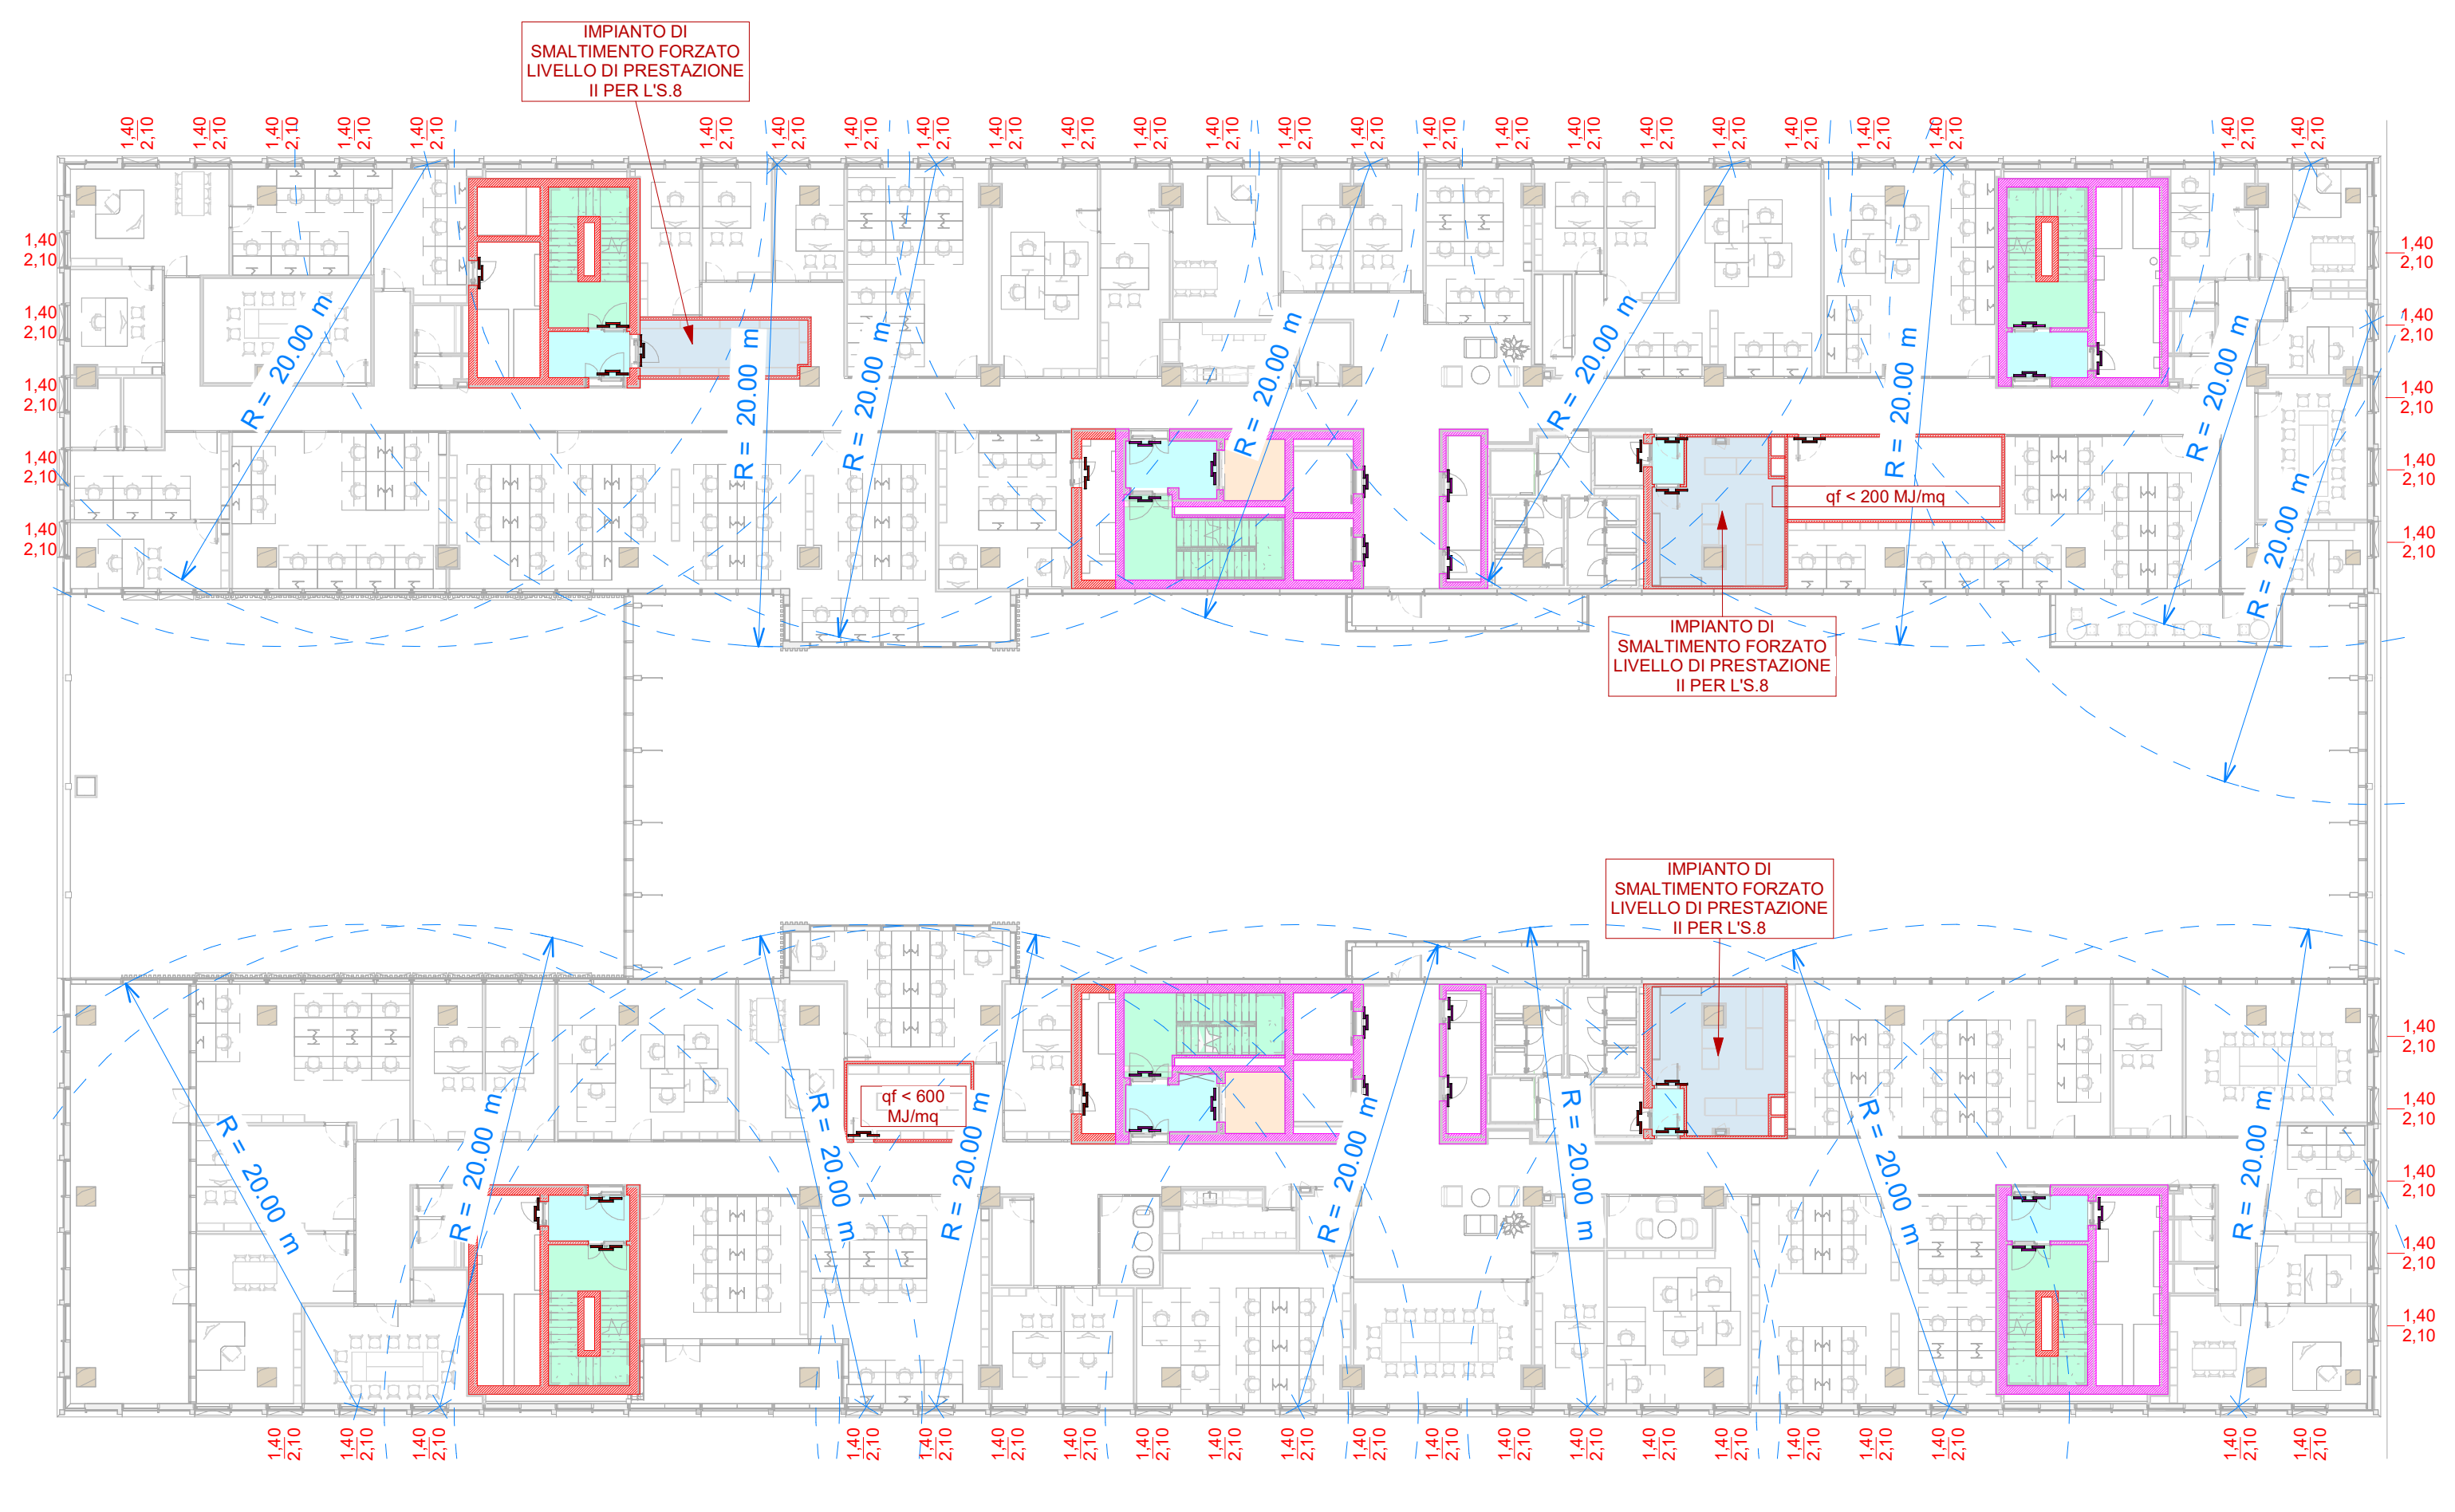
IMPIANTO DI SMALTIMENTO FORZATO LIVELLO DI PRESTAZIONE II PER L'S.8
R = 20.00 m
1,40 2,10
qf < 200 MJ/mq
qf < 600 MJ/mq

Piano quinto - Aperture di smaltimento - Scala 1 : 250

Piano mezzanino - Aperture di smaltimento - Scala 1 : 250

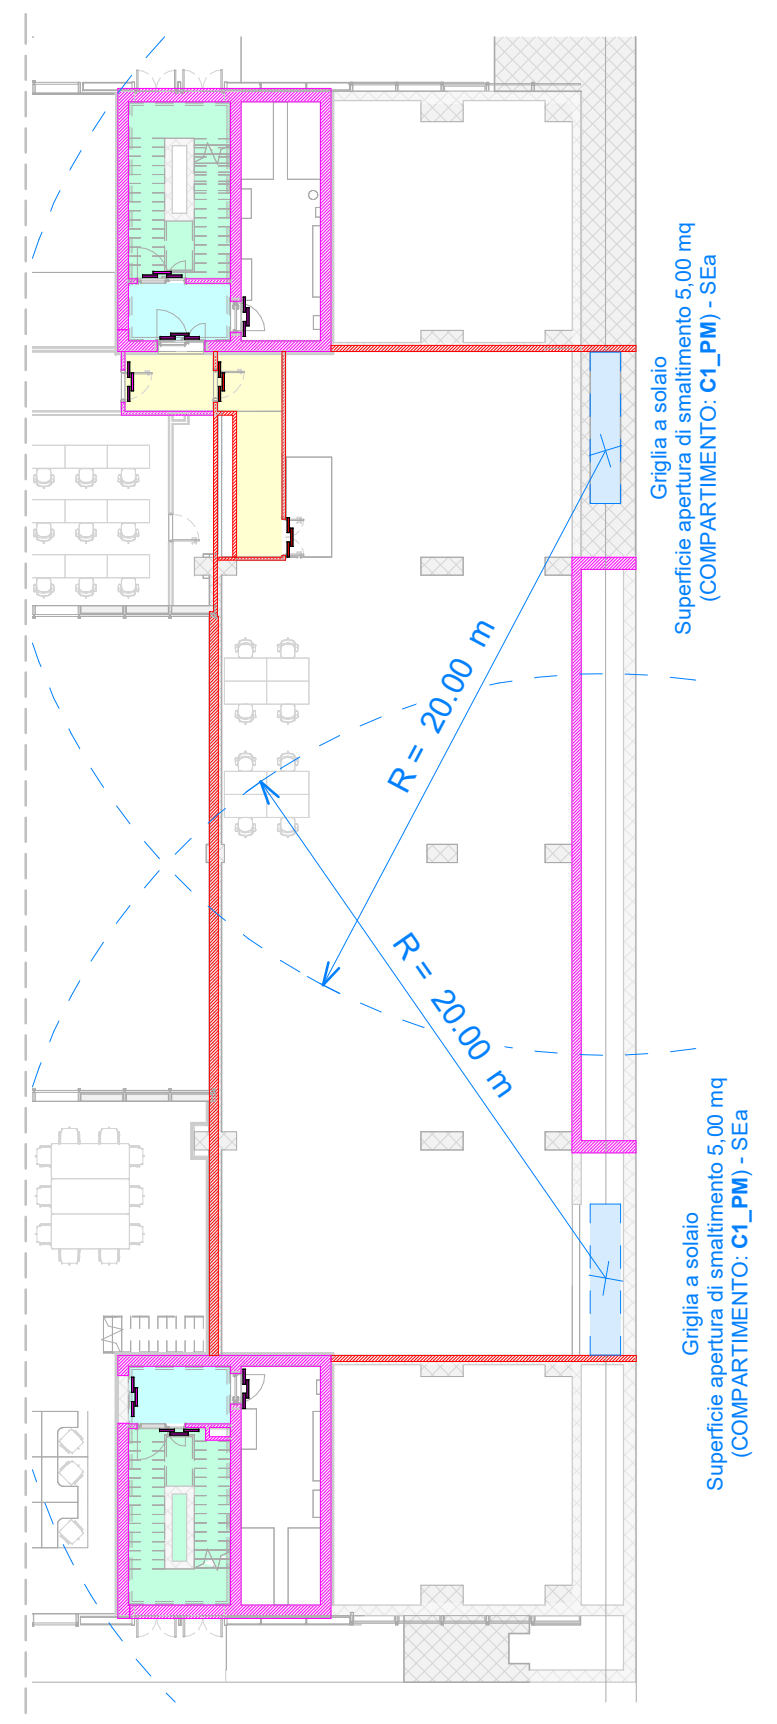
R = 20.00 m
R = 20.00 m
Griglia a solaio Superficie apertura di smaltimento 5,00 mq (COMPARTIMENTO: C1_PM) - SEa
Griglia a solaio Superficie apertura di smaltimento 5,00 mq (COMPARTIMENTO: C1_PM) - SEa

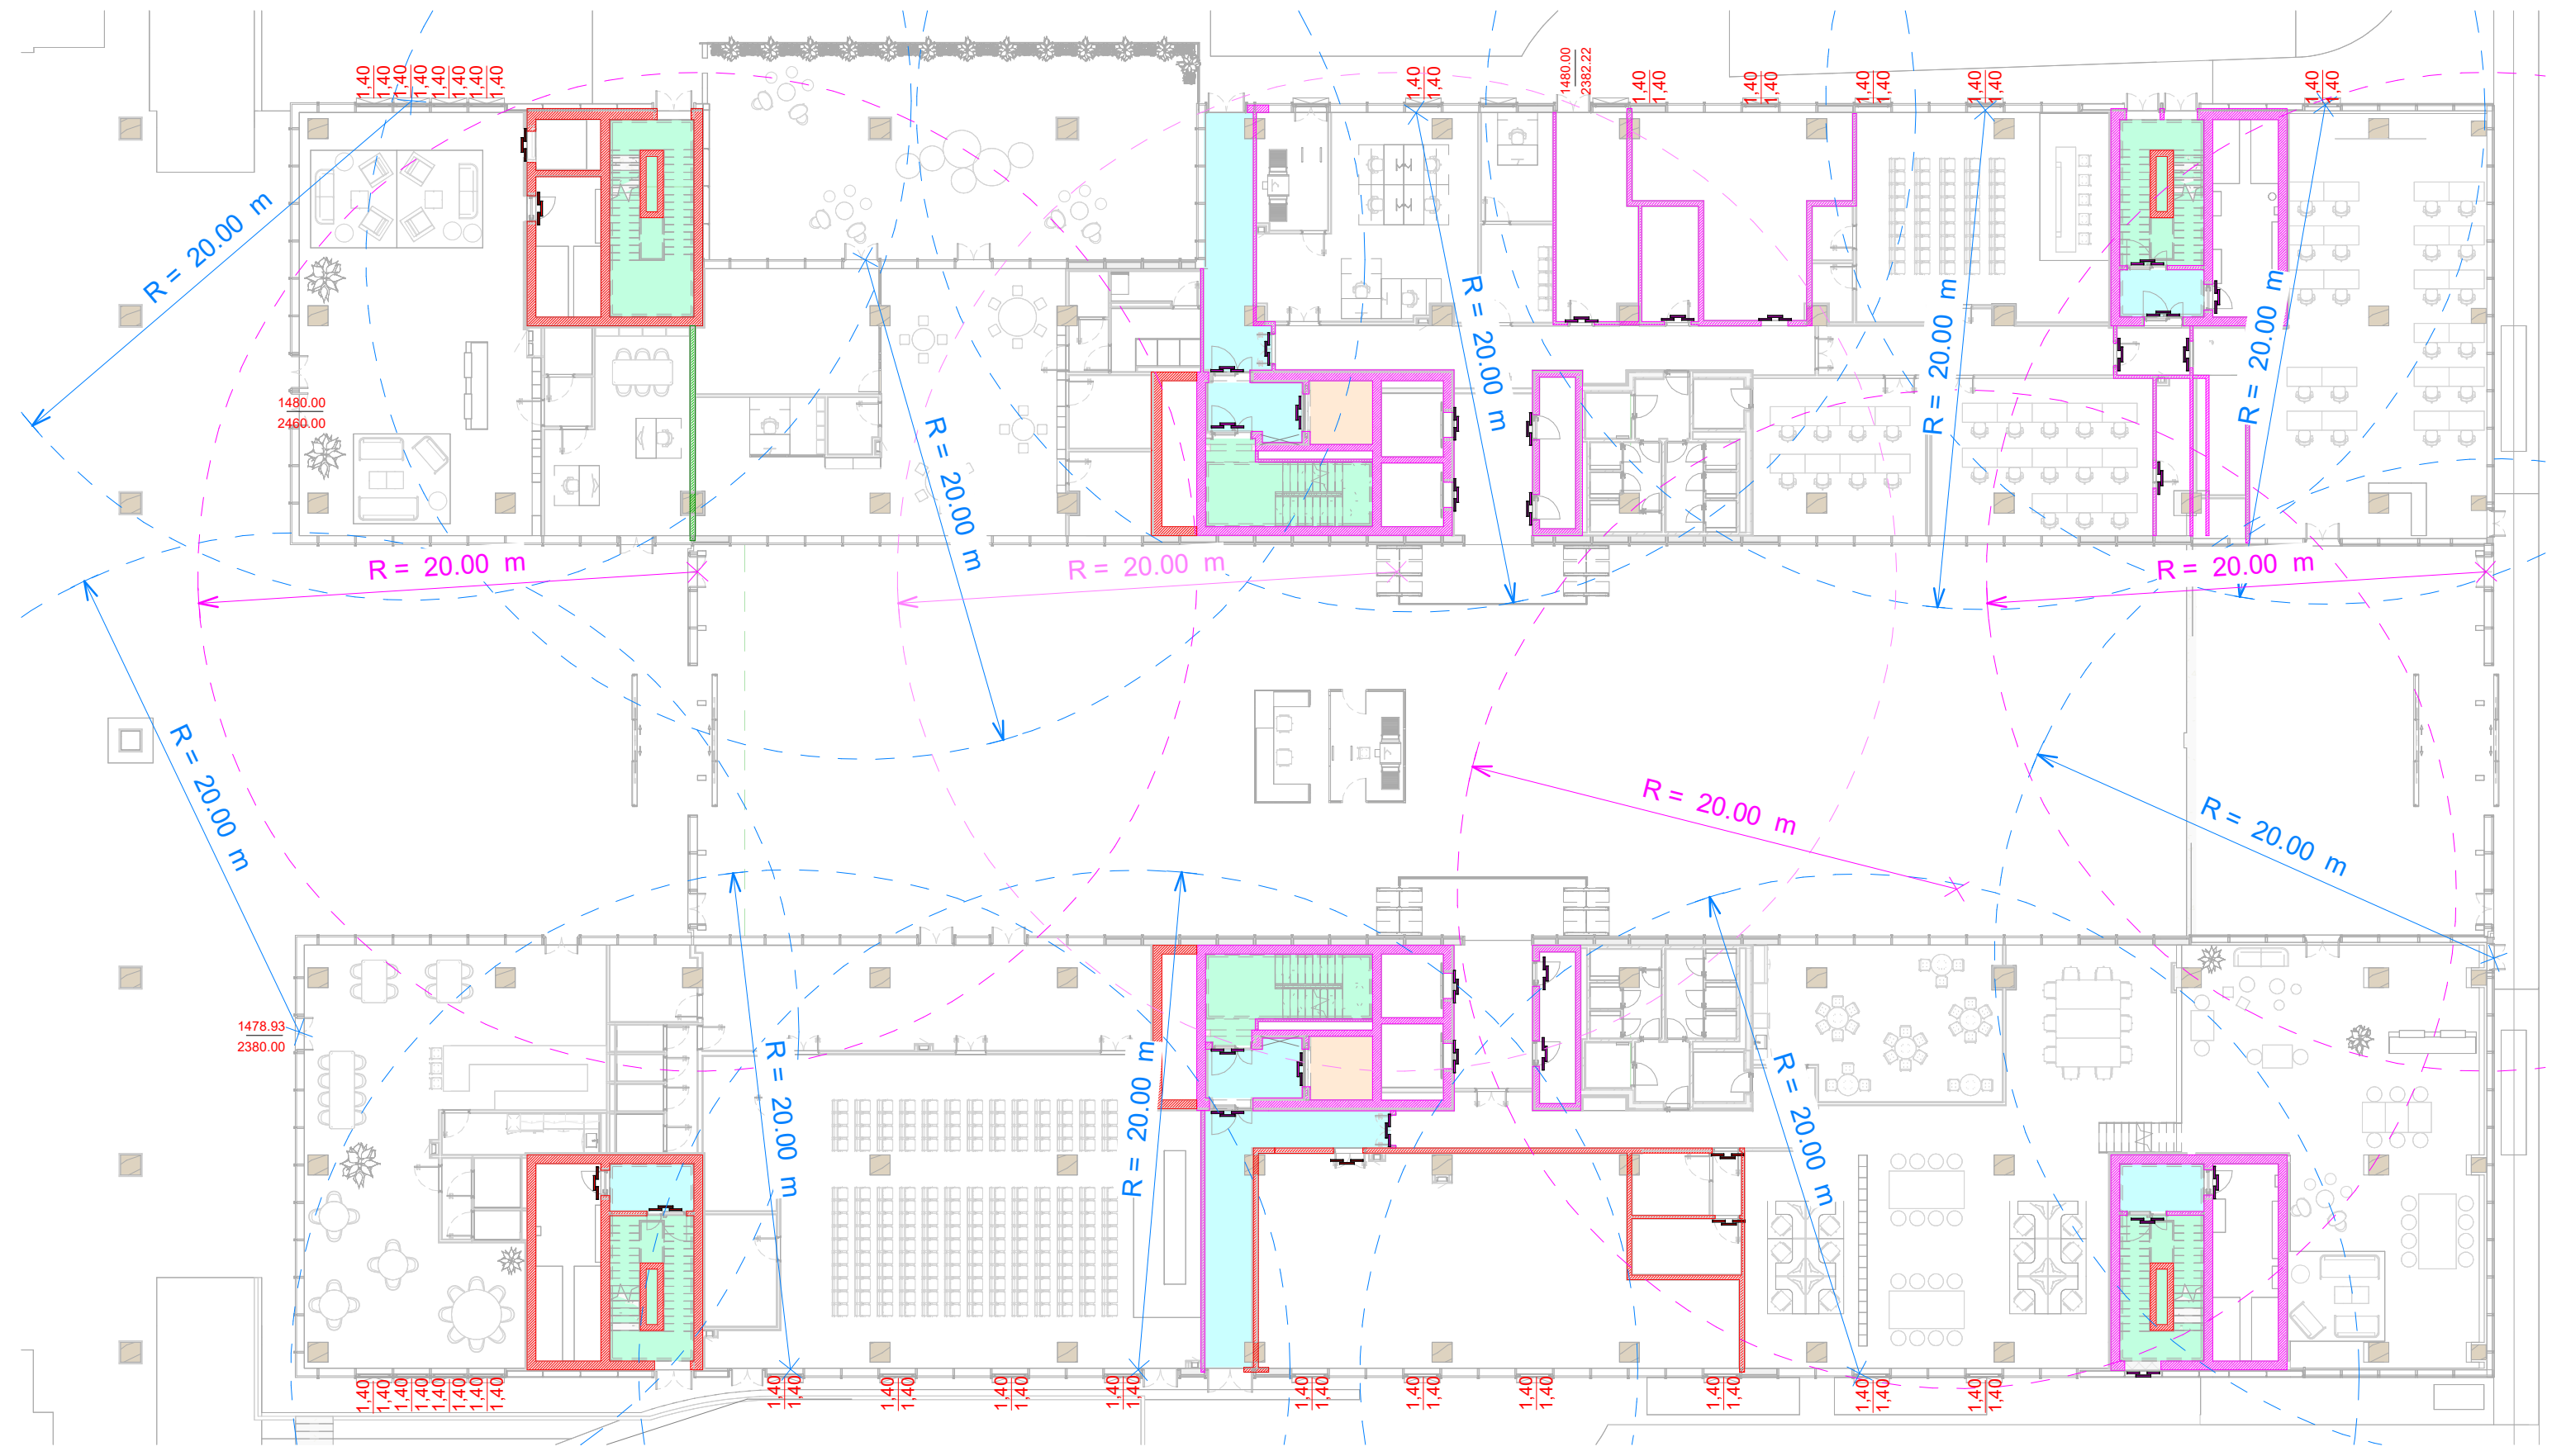

Piano terra - Aperture di smaltimento - Scala 1 : 250

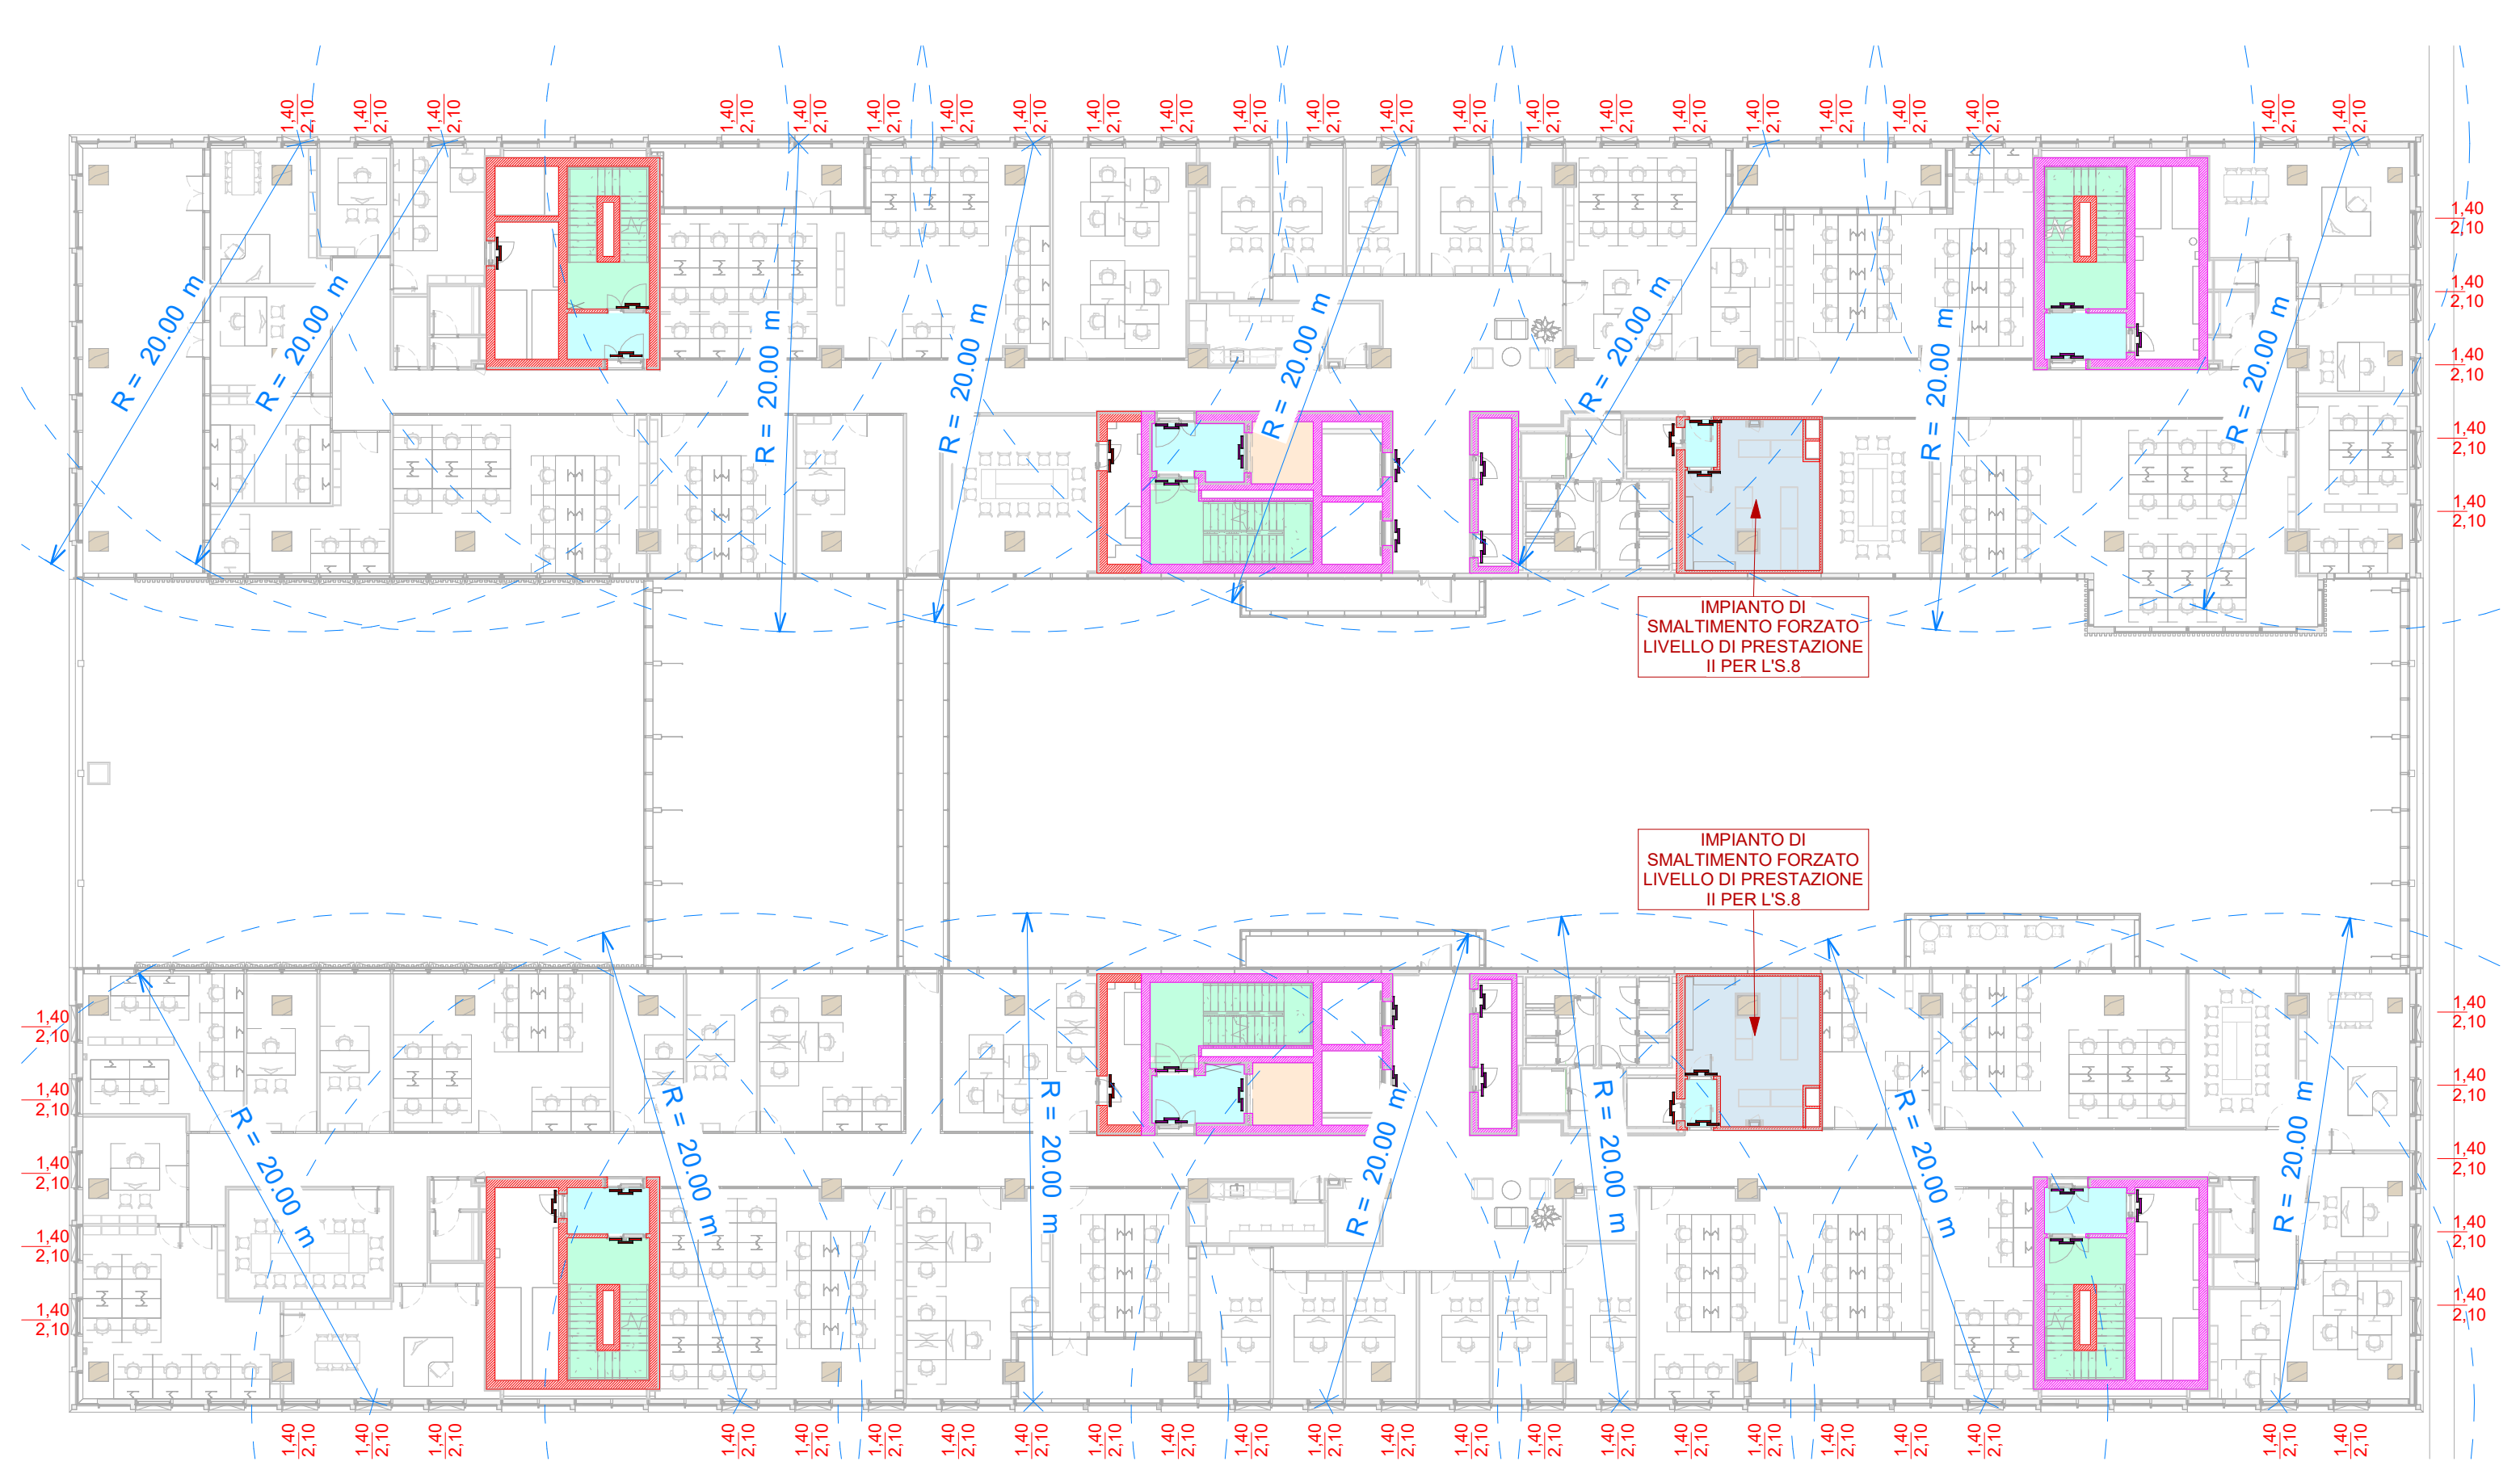
R = 20.00 m
1,40 2,10
IMPIANTO DI SMALTIMENTO FORZATO LIVELLO DI PRESTAZIONE II PER L'S.8

Piano terzo - Aperture di smaltimento - Scala 1 : 250

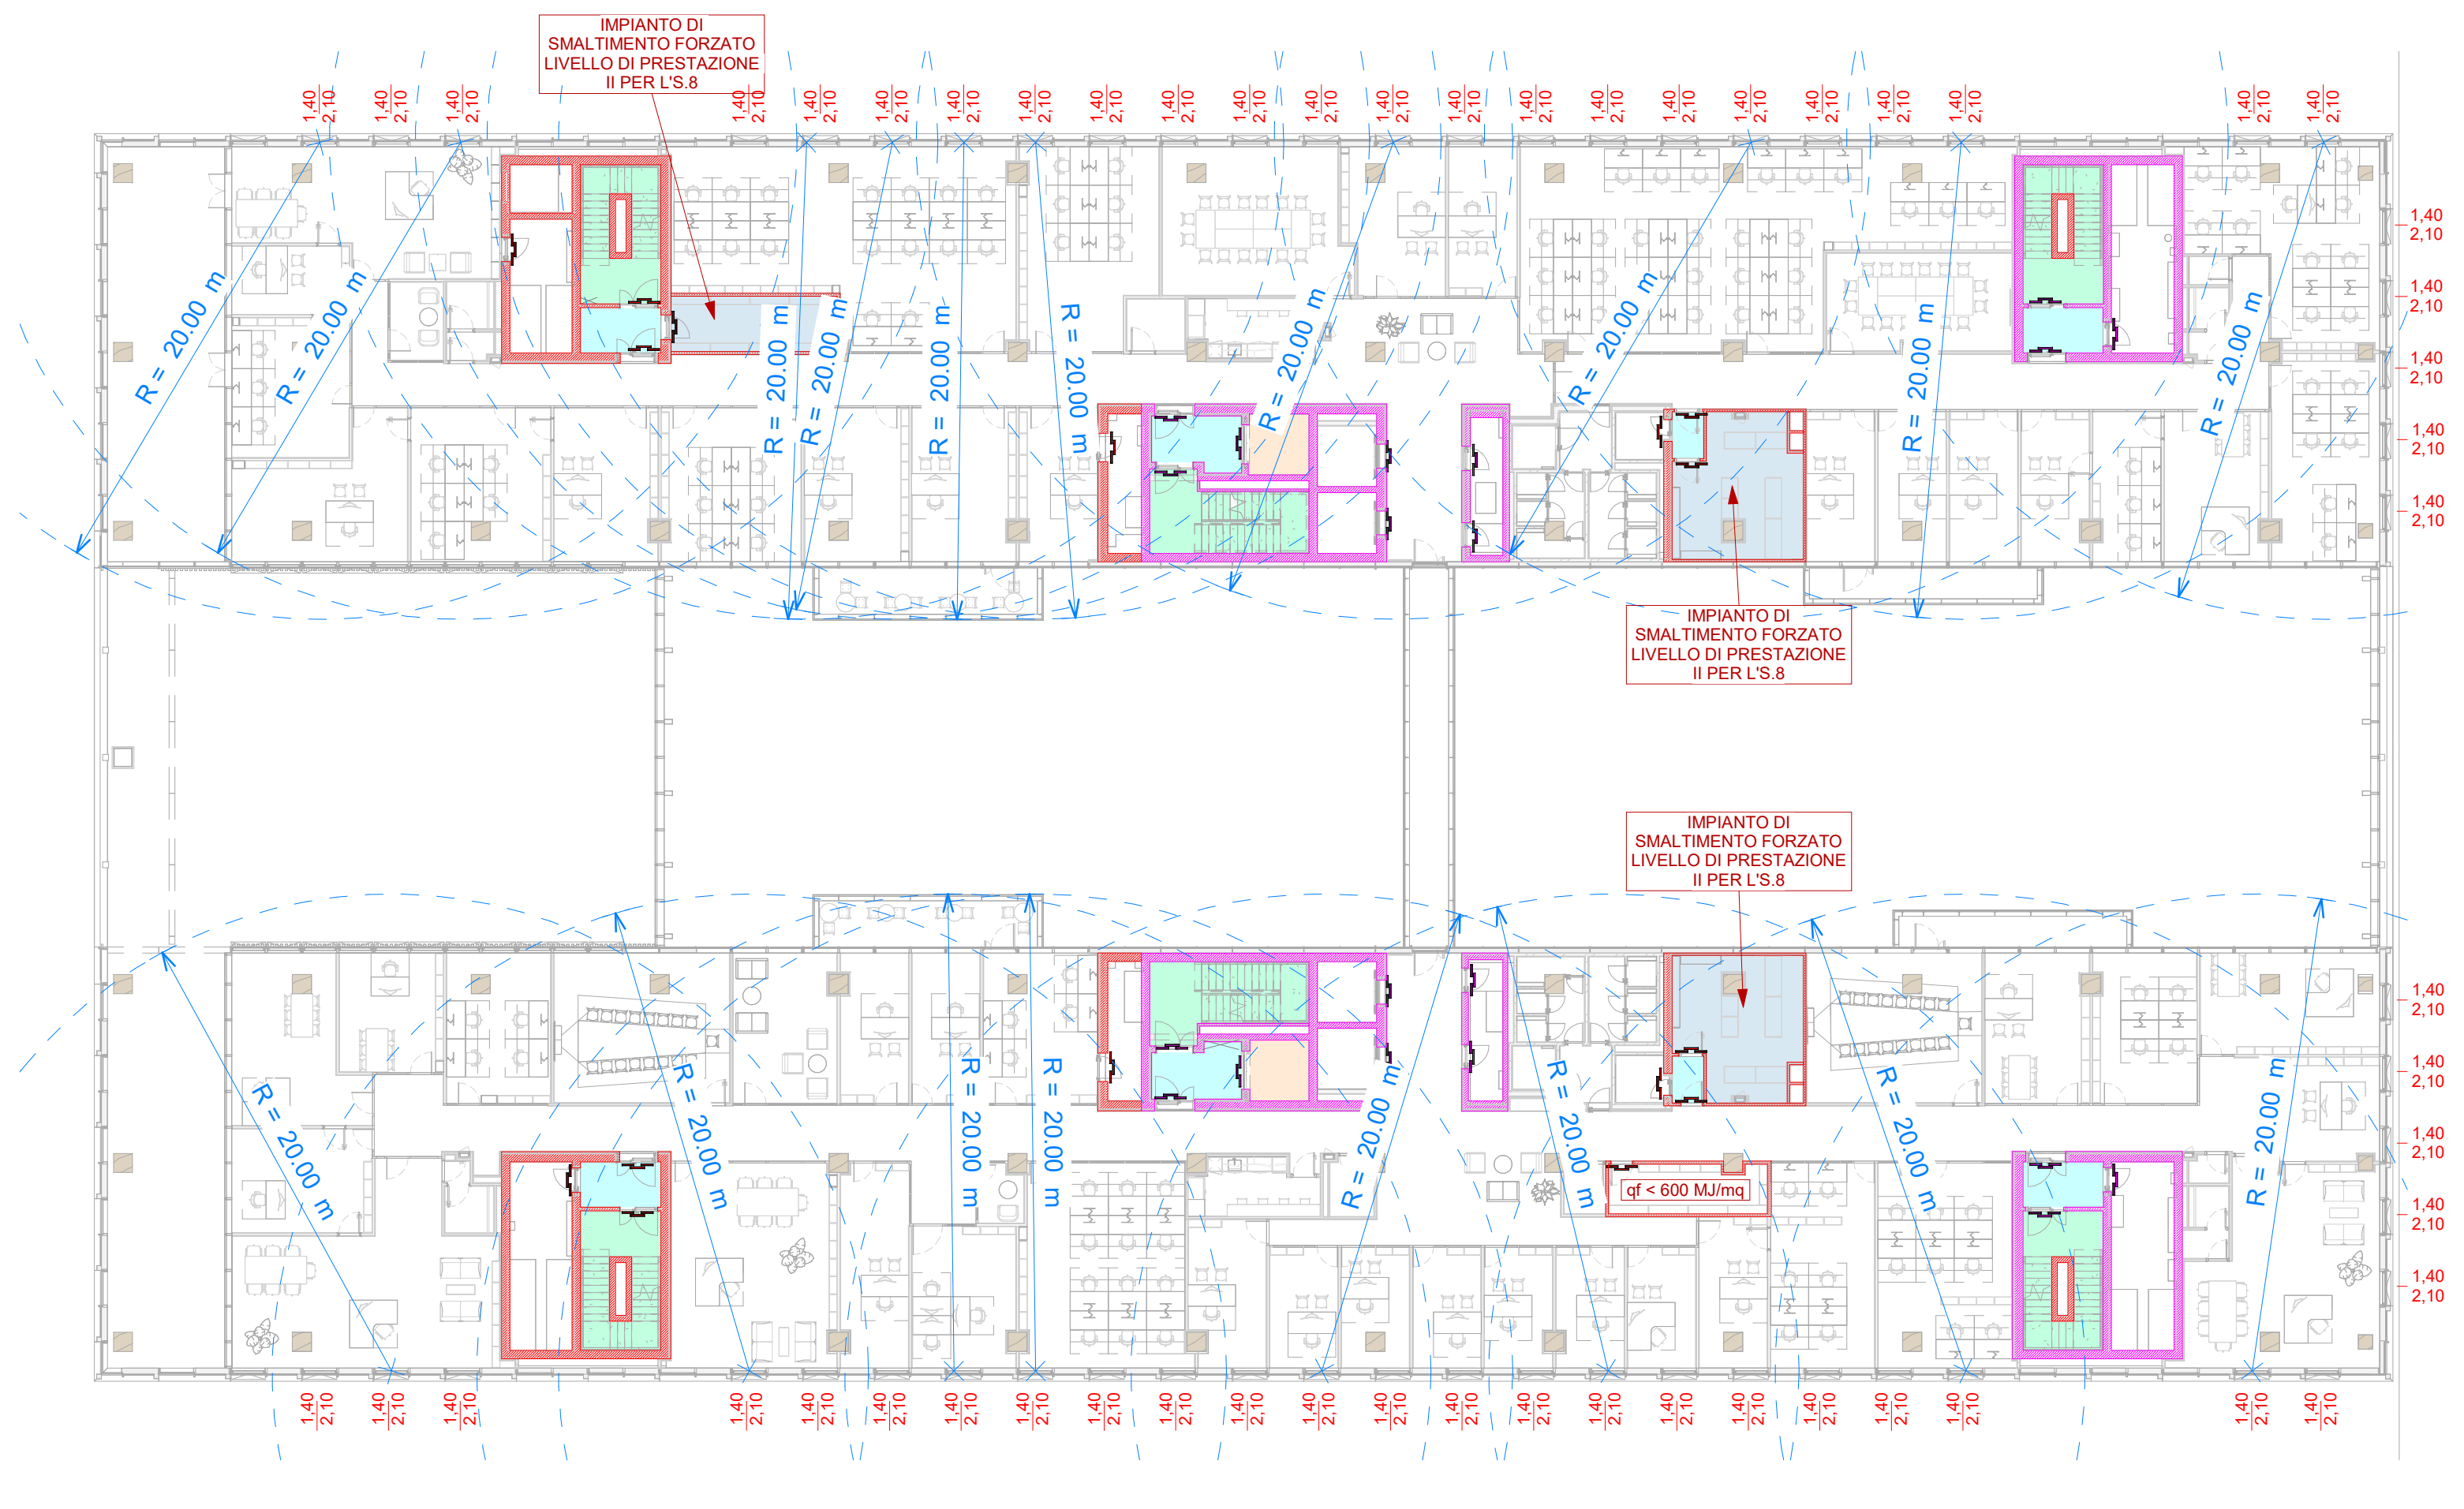
IMPIANTO DI SMALTIMENTO FORZATO LIVELLO DI PRESTAZIONE II PER L'S.8
R = 20.00 m
1,40 2,10
qf < 600 MJ/mq

Piano sesto - Aperture di smaltimento - Scala 1 : 250

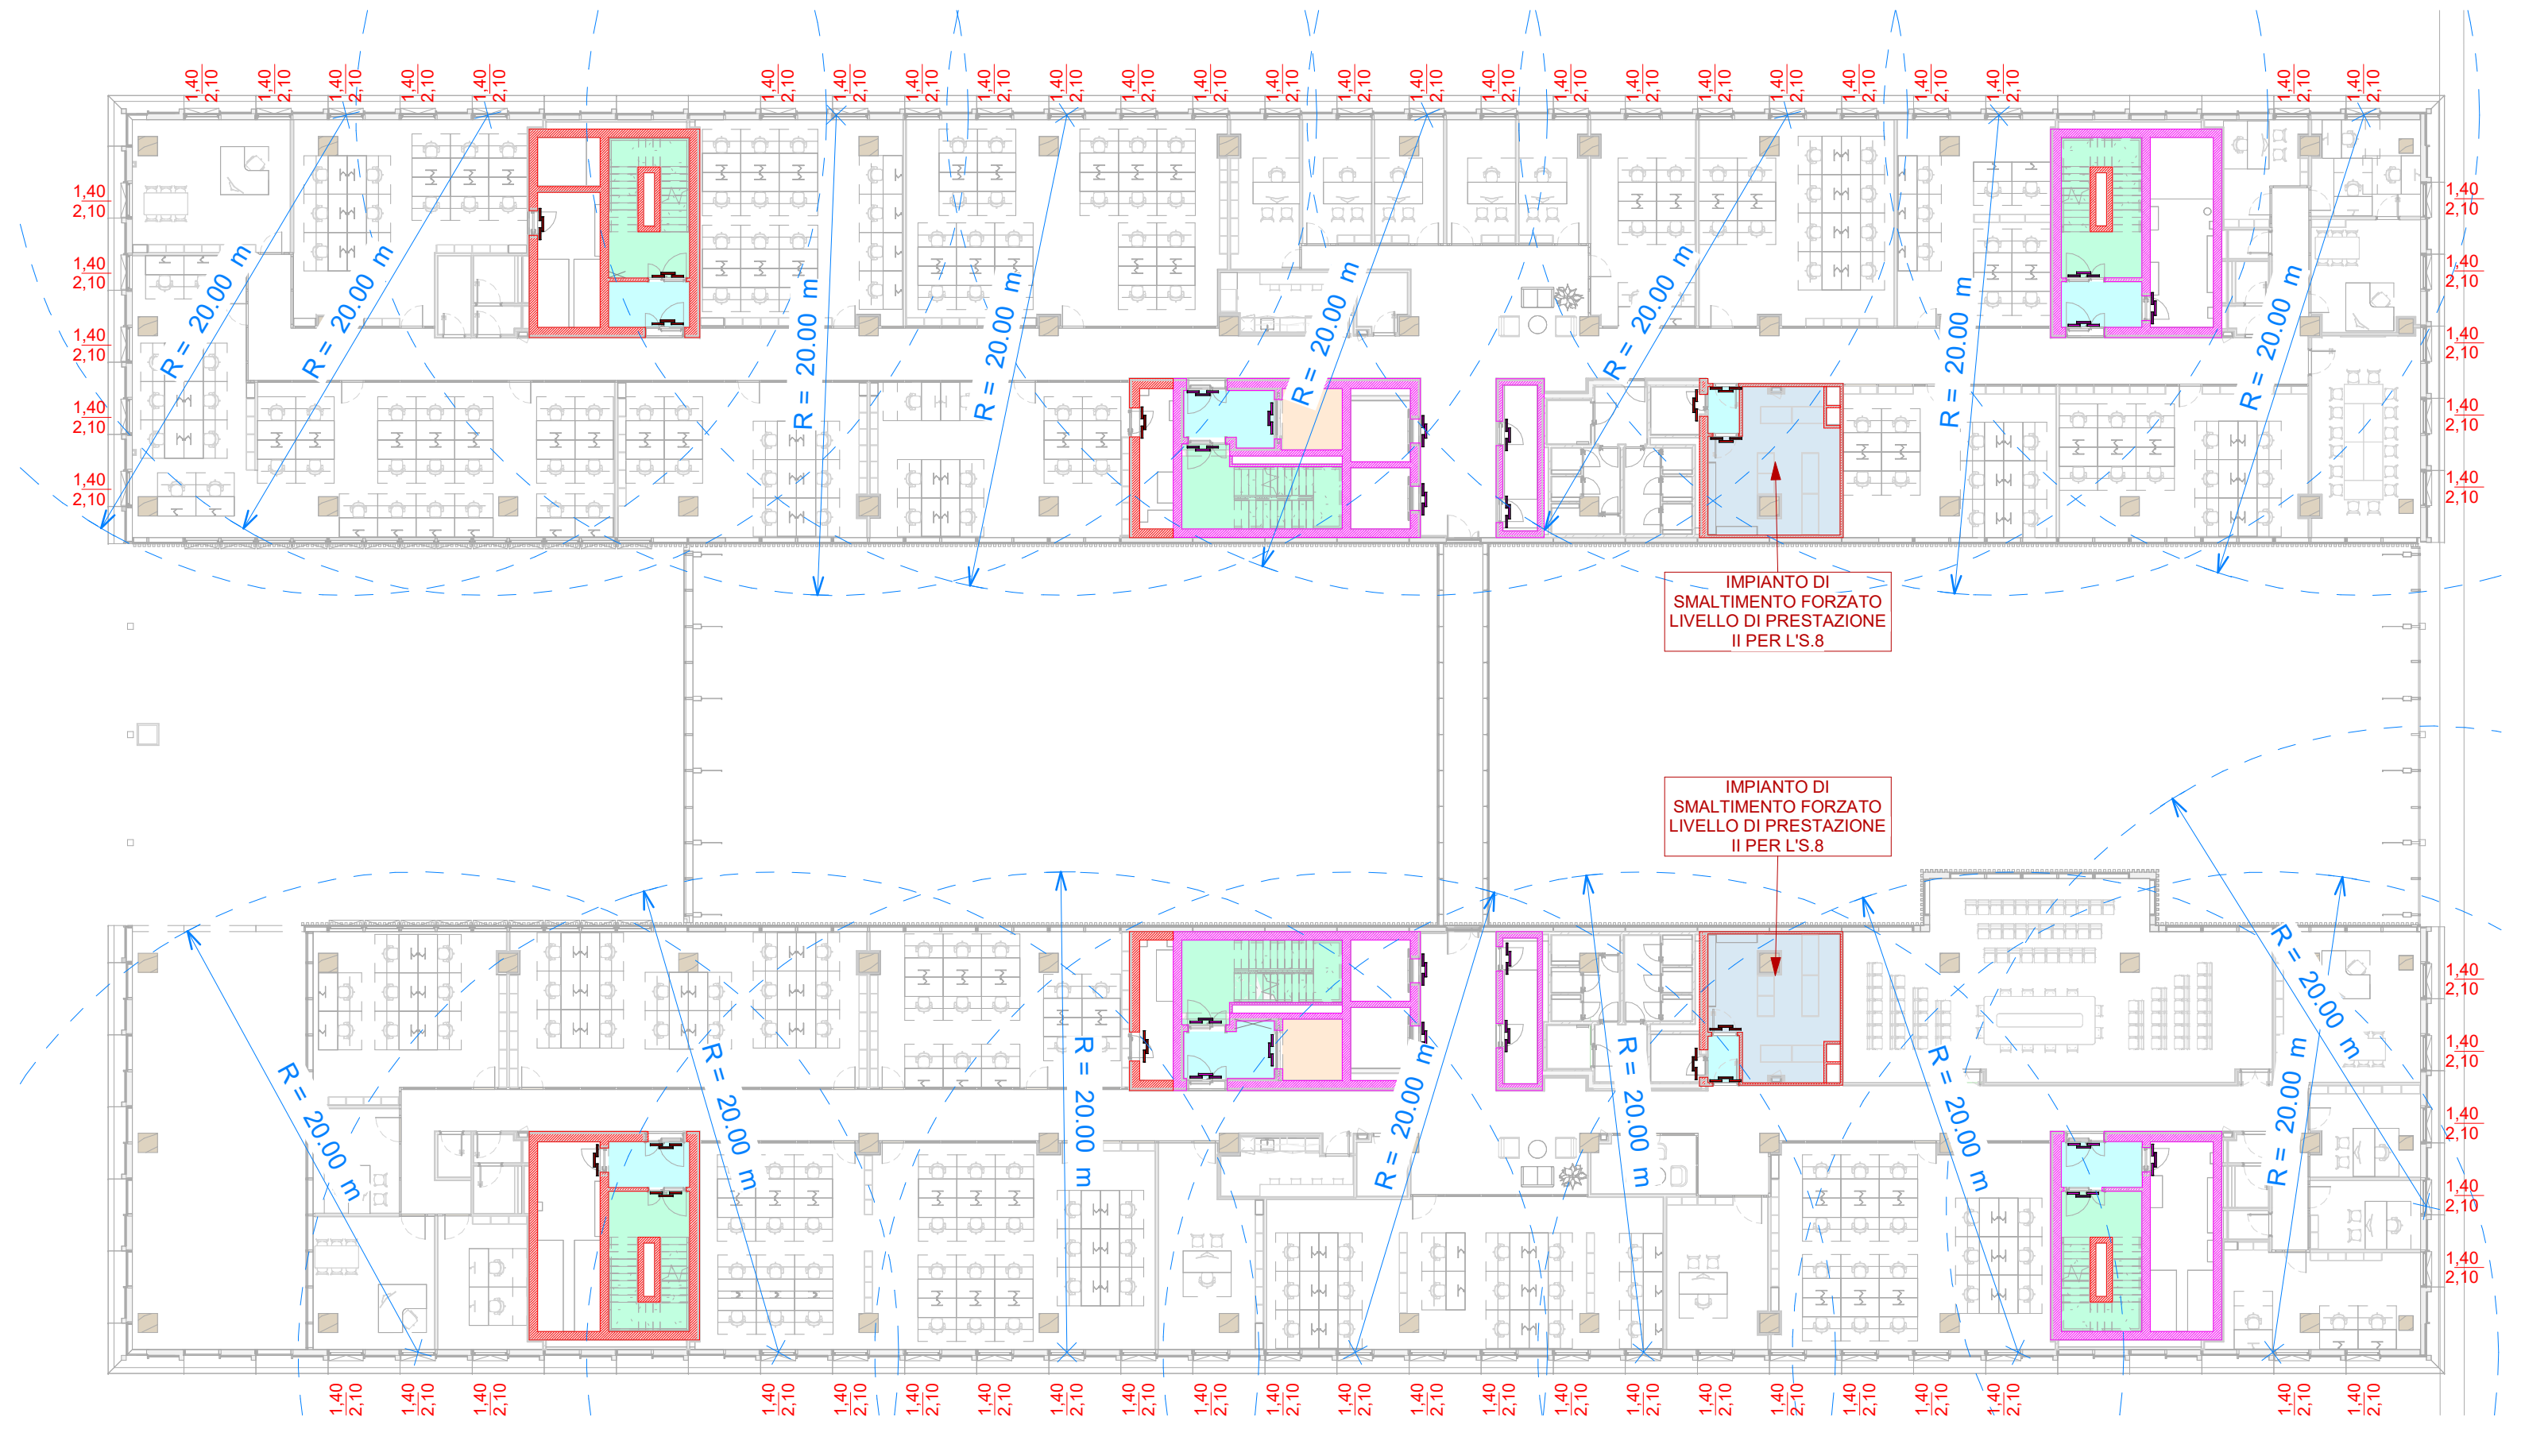
R = 20.00 m
1,40 2,10
IMPIANTO DI SMALTIMENTO FORZATO LIVELLO DI PRESTAZIONE II PER L'S.8

Piano primo - Aperture di smaltimento - Scala 1 : 250

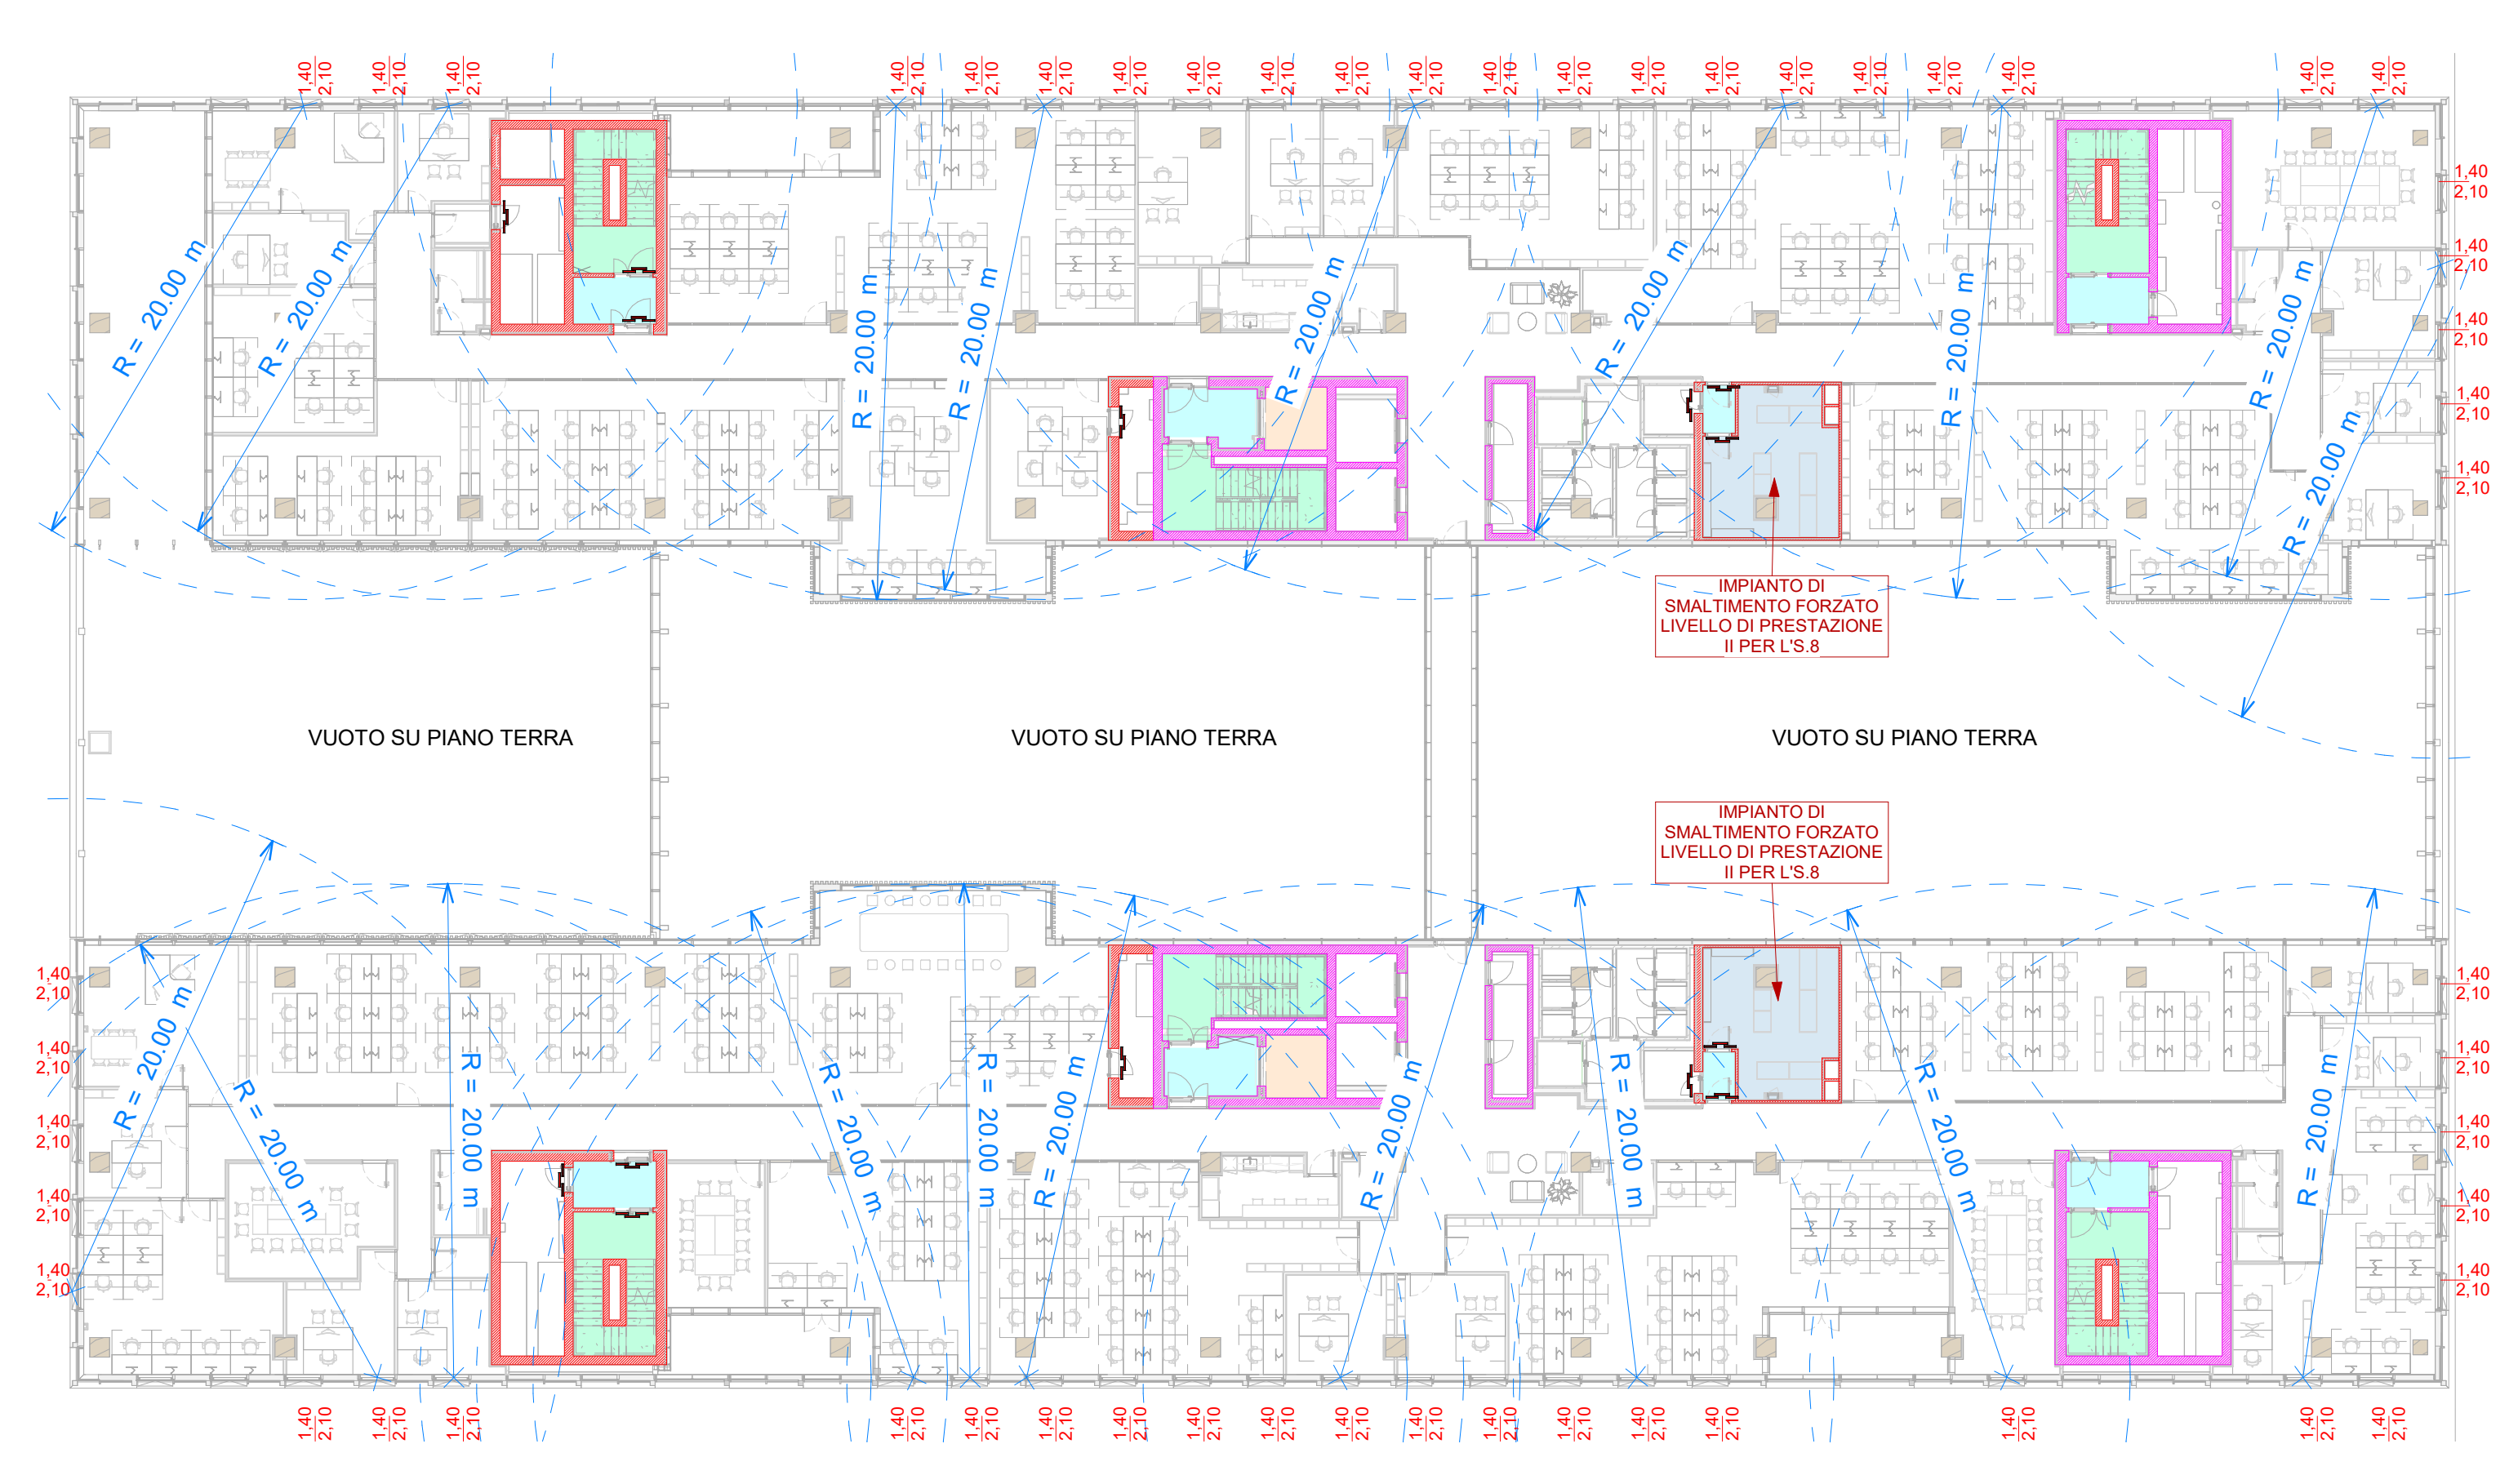

Piano quarto - Aperture di smaltimento - Scala 1 : 250

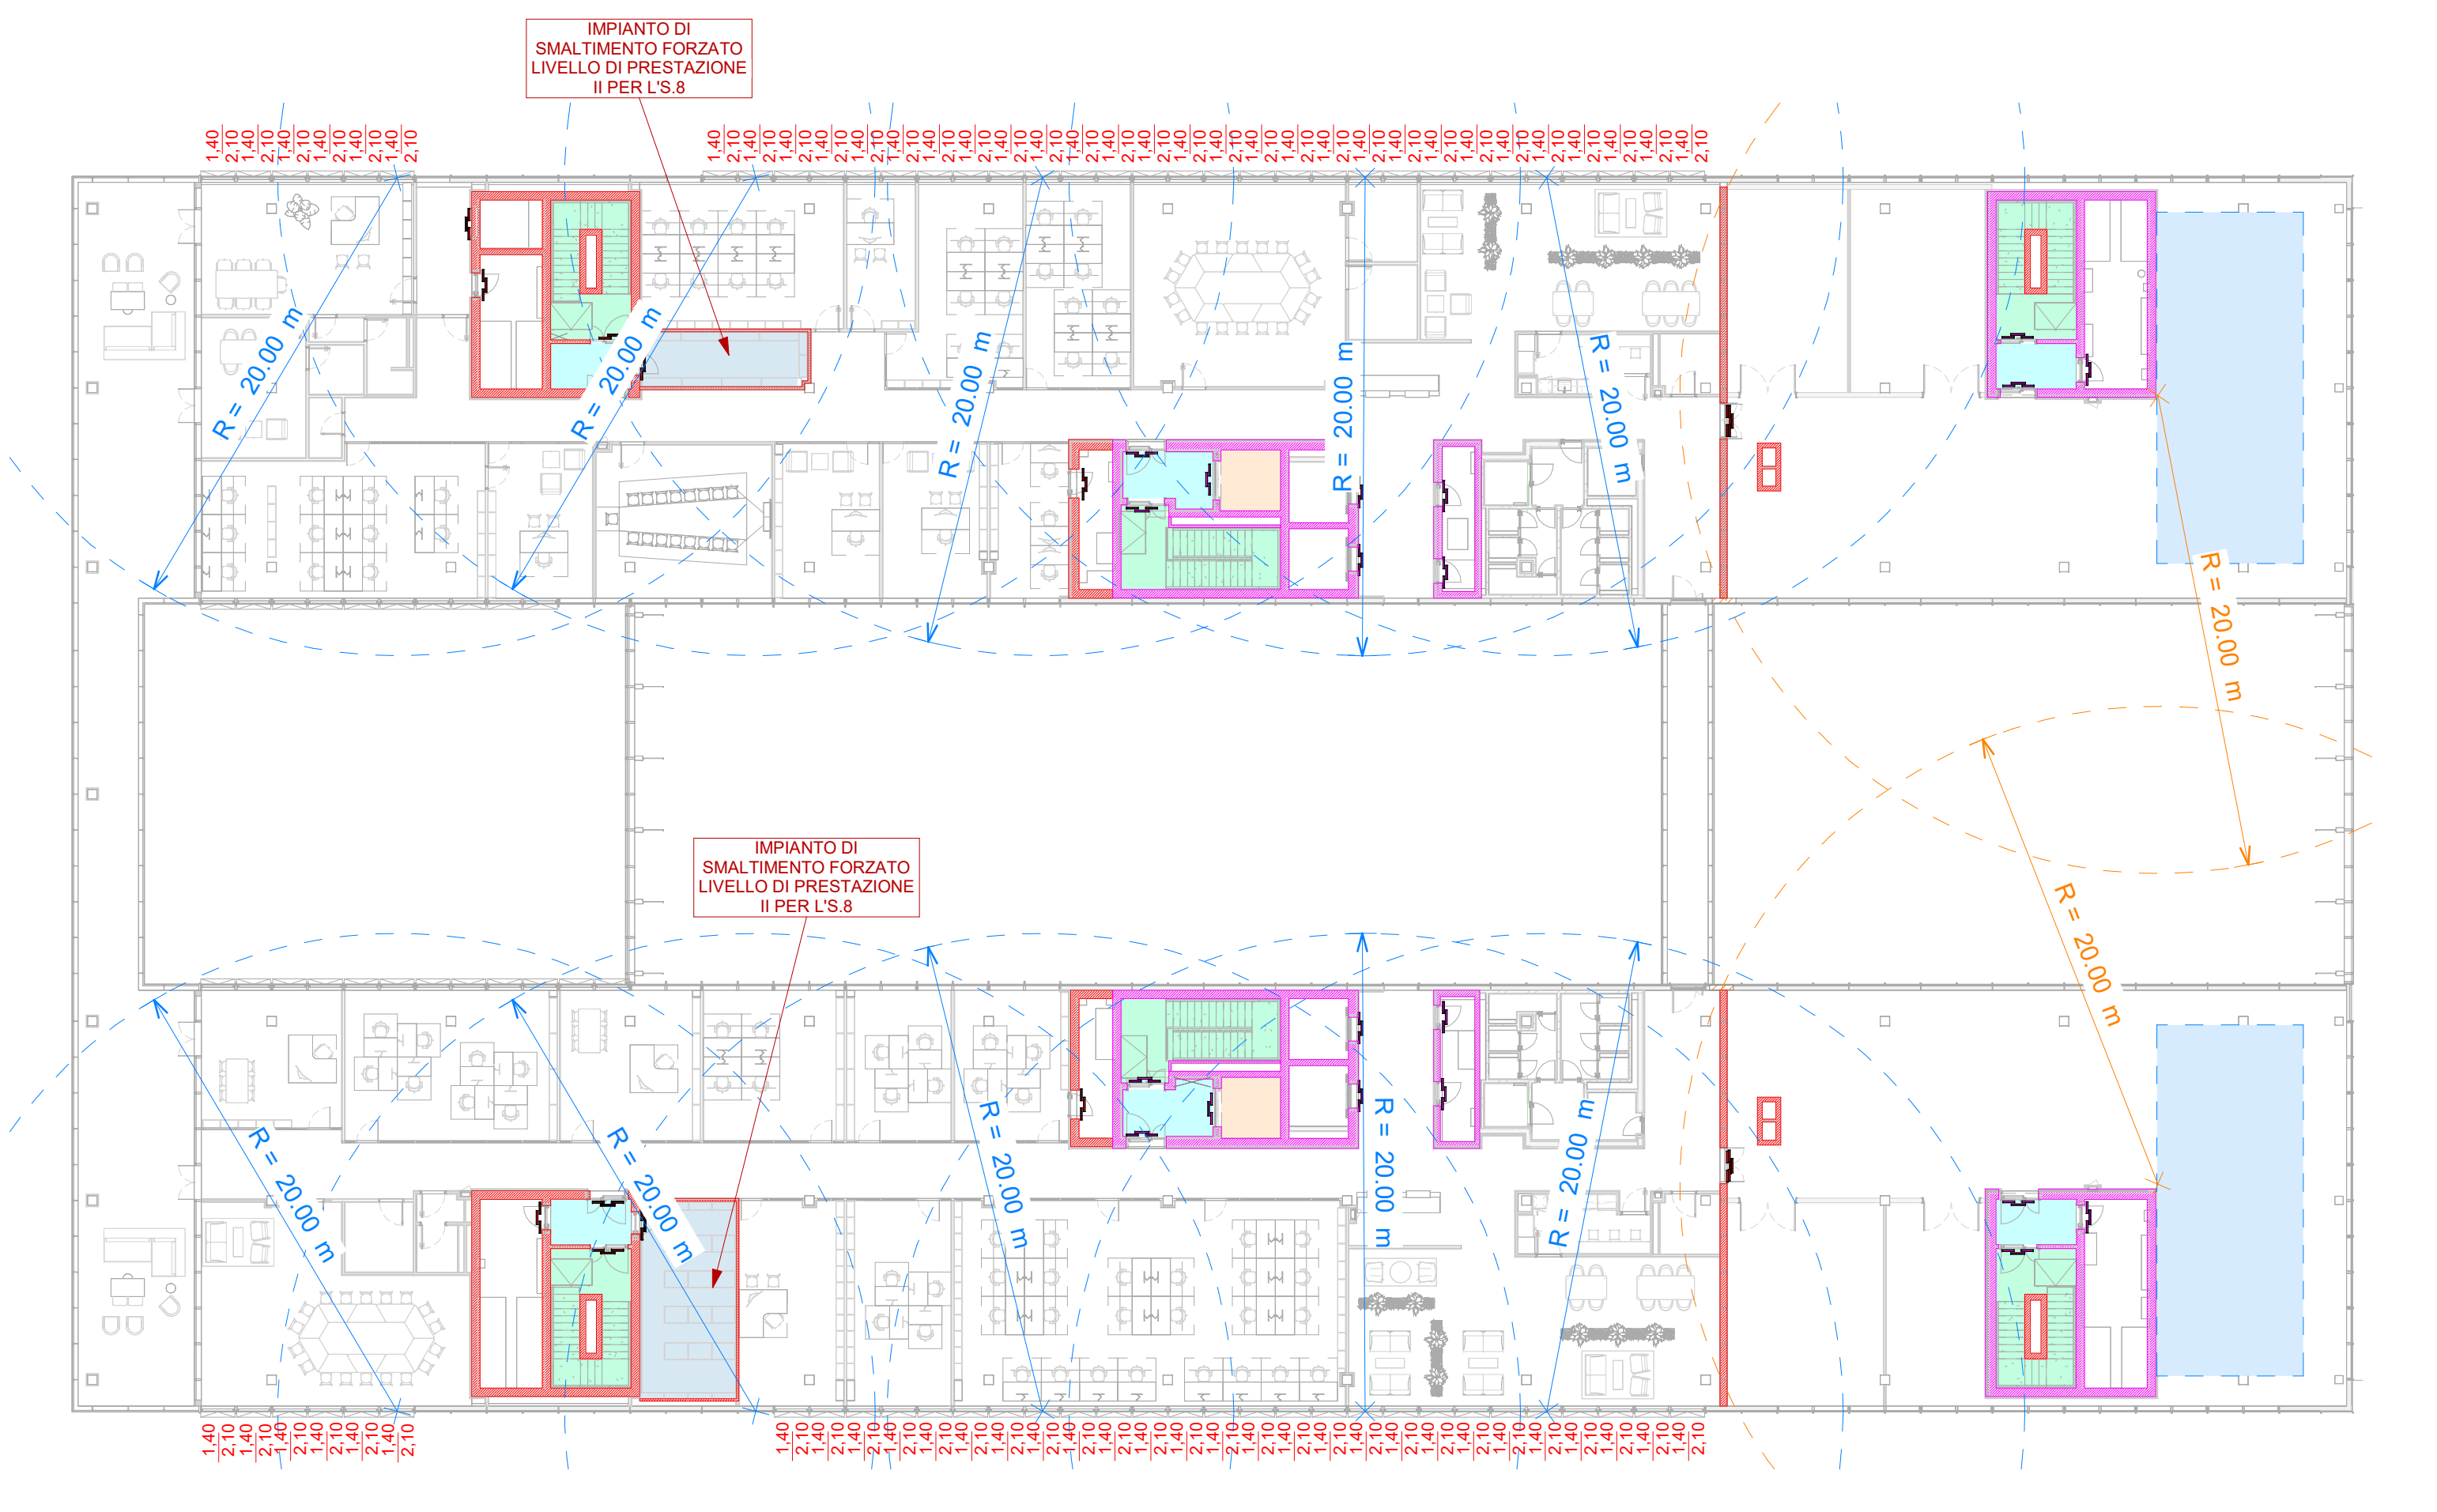
IMPIANTO DI SMALTIMENTO FORZATO LIVELLO DI PRESTAZIONE II PER L'S.8
R = 20.00 m

Piano settimo - Aperture di smaltimento - Scala 1 : 250

LEGENDA ANTINCENDIO

🟩	Parete REI 60	⇨	Percorso di esodo orizzontale
▬	Porta REI 60	➡	Percorso di esodo verticale
▨	Parete REI 30	⇨	Corridoio cieco
▬	Porta REI 30	E CO2	Estintore a CO2
▨	Parete REI 90	E	Estintore a polvere
▬	Porta REI 90	PAI	Pannello allarme incendi
🟥	Parete REI 120	◉	Pulsante antincendio
▬	Porta REI 120	FC	Rilevatore di fumo in controsoffitto
▭	Ascensore antincendio	T	Rilevatore di temperatura
▭	Filtro a prova di fumo	F	Rilevatore di fumo in ambiente
▭	Scala a prova di fumo	A	Rivelatore di fumo ad aspirazione a pavimento
▭	Filtro antincendio	OT	Rivelatore ottico - termico
▭	Aperture di smaltimento fumi e calore	C	Rivelatori ottico di fumo per canale di condizionamento
▨	Fasce di seprazione	⊗	Ripetitore luminoso
PCT◎	Pulsante di sgancio centrale tecnologica	CRI	Centrale rilevazione incendi
PFTV◎	Pulsante di sgancio impianto fotovoltaico	EVAC	Centrale EVAC
PSG◎	Pulsante di sgancio generale	▣	Impianto di comunicazione bidirezionale
☒	Illuminazione di emergenza uscita di emergenza	▣	Diffusore acustico a parete
☒	Illuminazione di emergenza	▮	Diffusore acustico a parete a colonna
◉	Pulsante blocco estinzione - Impianto aerosol	▣	Diffusore acustico a parete bidirezionale
◉	Pulsante estinzione manuale - Impianto aerosol	V	Attacco di mandata doppio
▢	Impianto di spegnimento automatico ad aerosol	●	Idrante a muro UNI 45
TX	Rilevazione fumi automatica di tipo lineare	▲	Idrante esterno UNI 70

APPROVAZIONE COMMITTENTE	
	A - APPROVATO
	B - APPROVATO CON COMMENTI
	C - NON APPROVATO

Rev.	Data	Descriz.	Red.	Ver.	App.
0	05/10/2026	PRIMA EMISSIONE			

SCALA

SEDE PROGETTO
VIALE BOSTON 25
Comune di ROMA, RM - 00144

NUMERO PROGETTO
RMB1284

STATO
P

FASE PROGETTUALE:
PFTE

RTP:

Mandataria:
Progetto strutturale
GPA PARTNERS
via Leone X 3
50129 Firenze
+39 055 468291
info@gpapartners.com

Mandante:
Progetto architettonico
PLP/ARCHITECTURE
The White Chapel Building, 10
Whitechapel High Street Londra, E1 8QS,
United Kingdom
+44 (0)20 3006 3900
info@plparchitecture.com

Mandante:
Progetto architettonico
OBLYK
Via San Vito, 26
20123 Milano, Italia
+39 328 841 0677
office@oblyk.studio

Mandante:
Progetto impianti
Via Cavour, 4
70027 Palo del Colle (BA)
+39 080 8594347
info@studioperillo.eu

Mandante:
Responsabile progettazione sostenibile dell'oopera
VALENTINI architetture
Via Giuseppe Verdi, 26
63822 Porto San Giorgio (FM)
+39 0734674423
info@valentiniarchitetture.com

Mandante:
enser
Via Beccarini, 29
48018 Faenza (RA)
+39 0546663423
ingegneria@enser.it

PROGETTO: CIG: B4C1AD81FA CUP: G84H22000360001

Realizzazione della nuova sede del Ministero dell'Ambiente e della Sicurezza Energetica
"MASE"

Codice bene: RMB1284
Codice fabbricato: RM0411001

TITOLO

APERTURE DI SMALTIMENTO - VERIFICA DISTRIBUZIONE UNIFORME

AGENZIA DEL DEMANIO
Struttura per la progettazione
Via Barberini 38, 00187, Roma
RUP: Arch. Isabella Di Marsico
DEC: Ing. Benedetto Grivo

AGENZIA DEL DEMANIO

NOME FILE
RMB1284-ADD-PLANLIVEL-ZZ-DR-I-PN0001

REV
0
05/10/2026