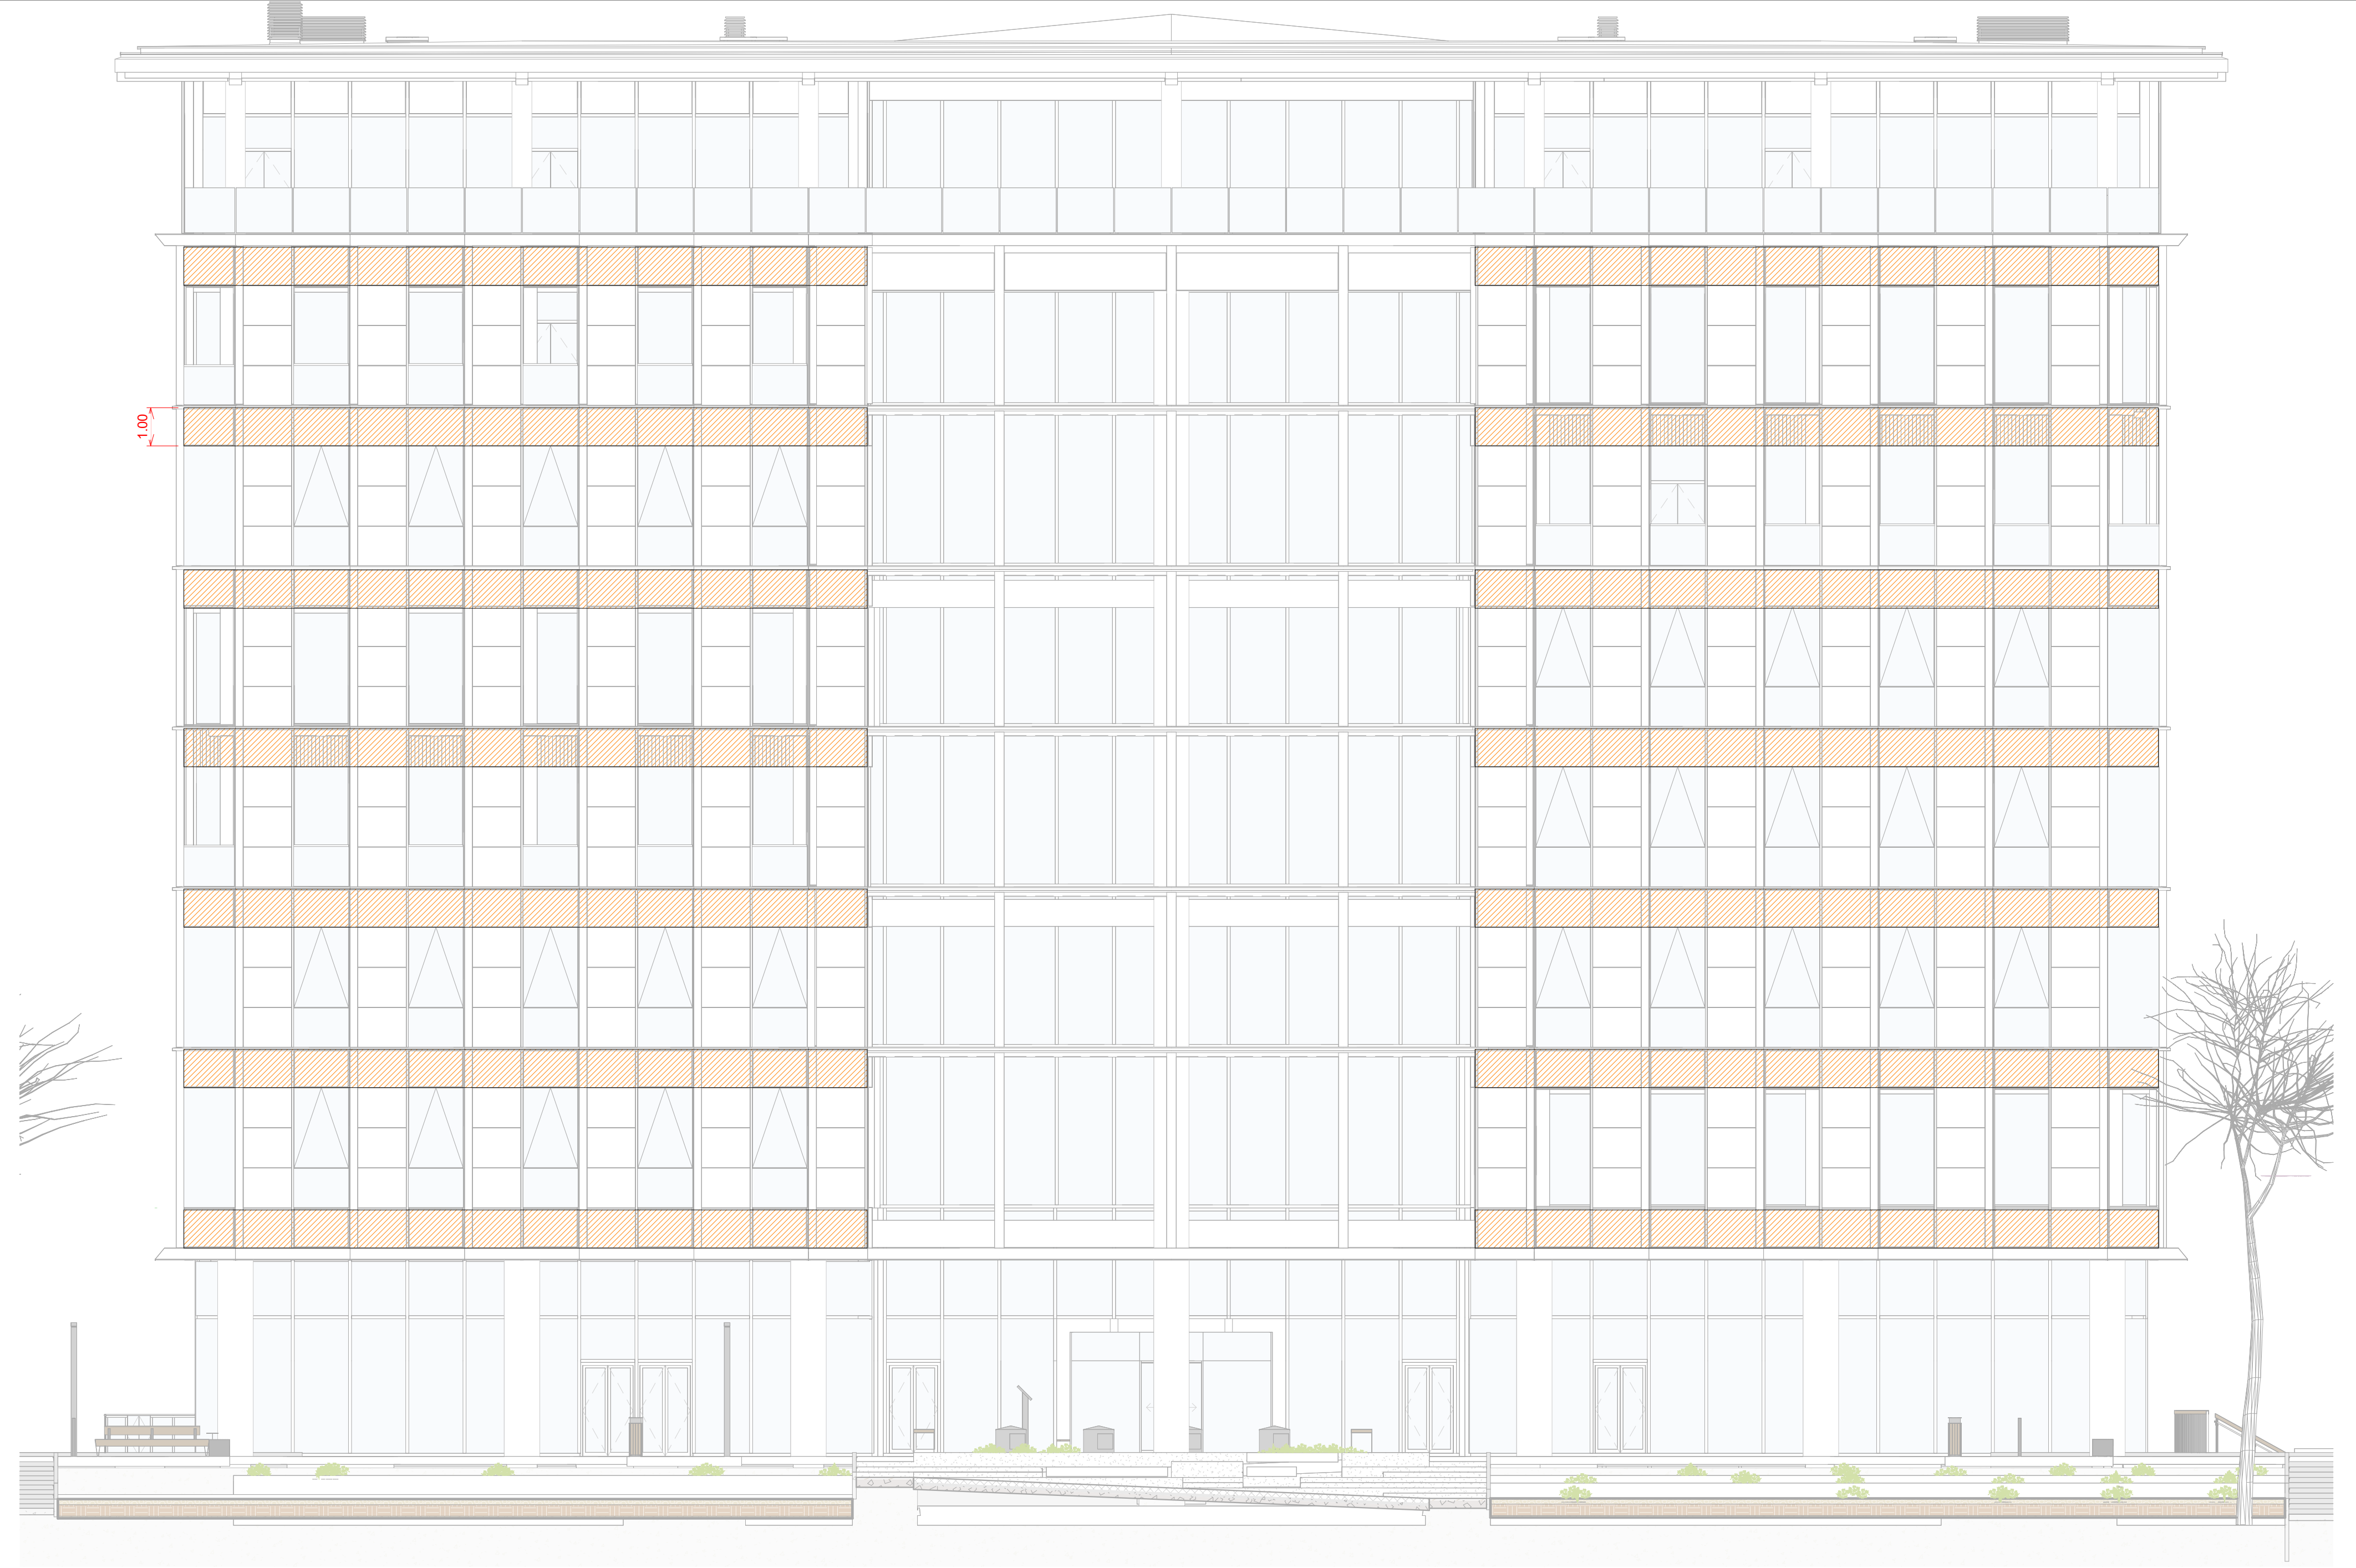

PROSPETTO VIALE AMERICA - Scala 1 : 100

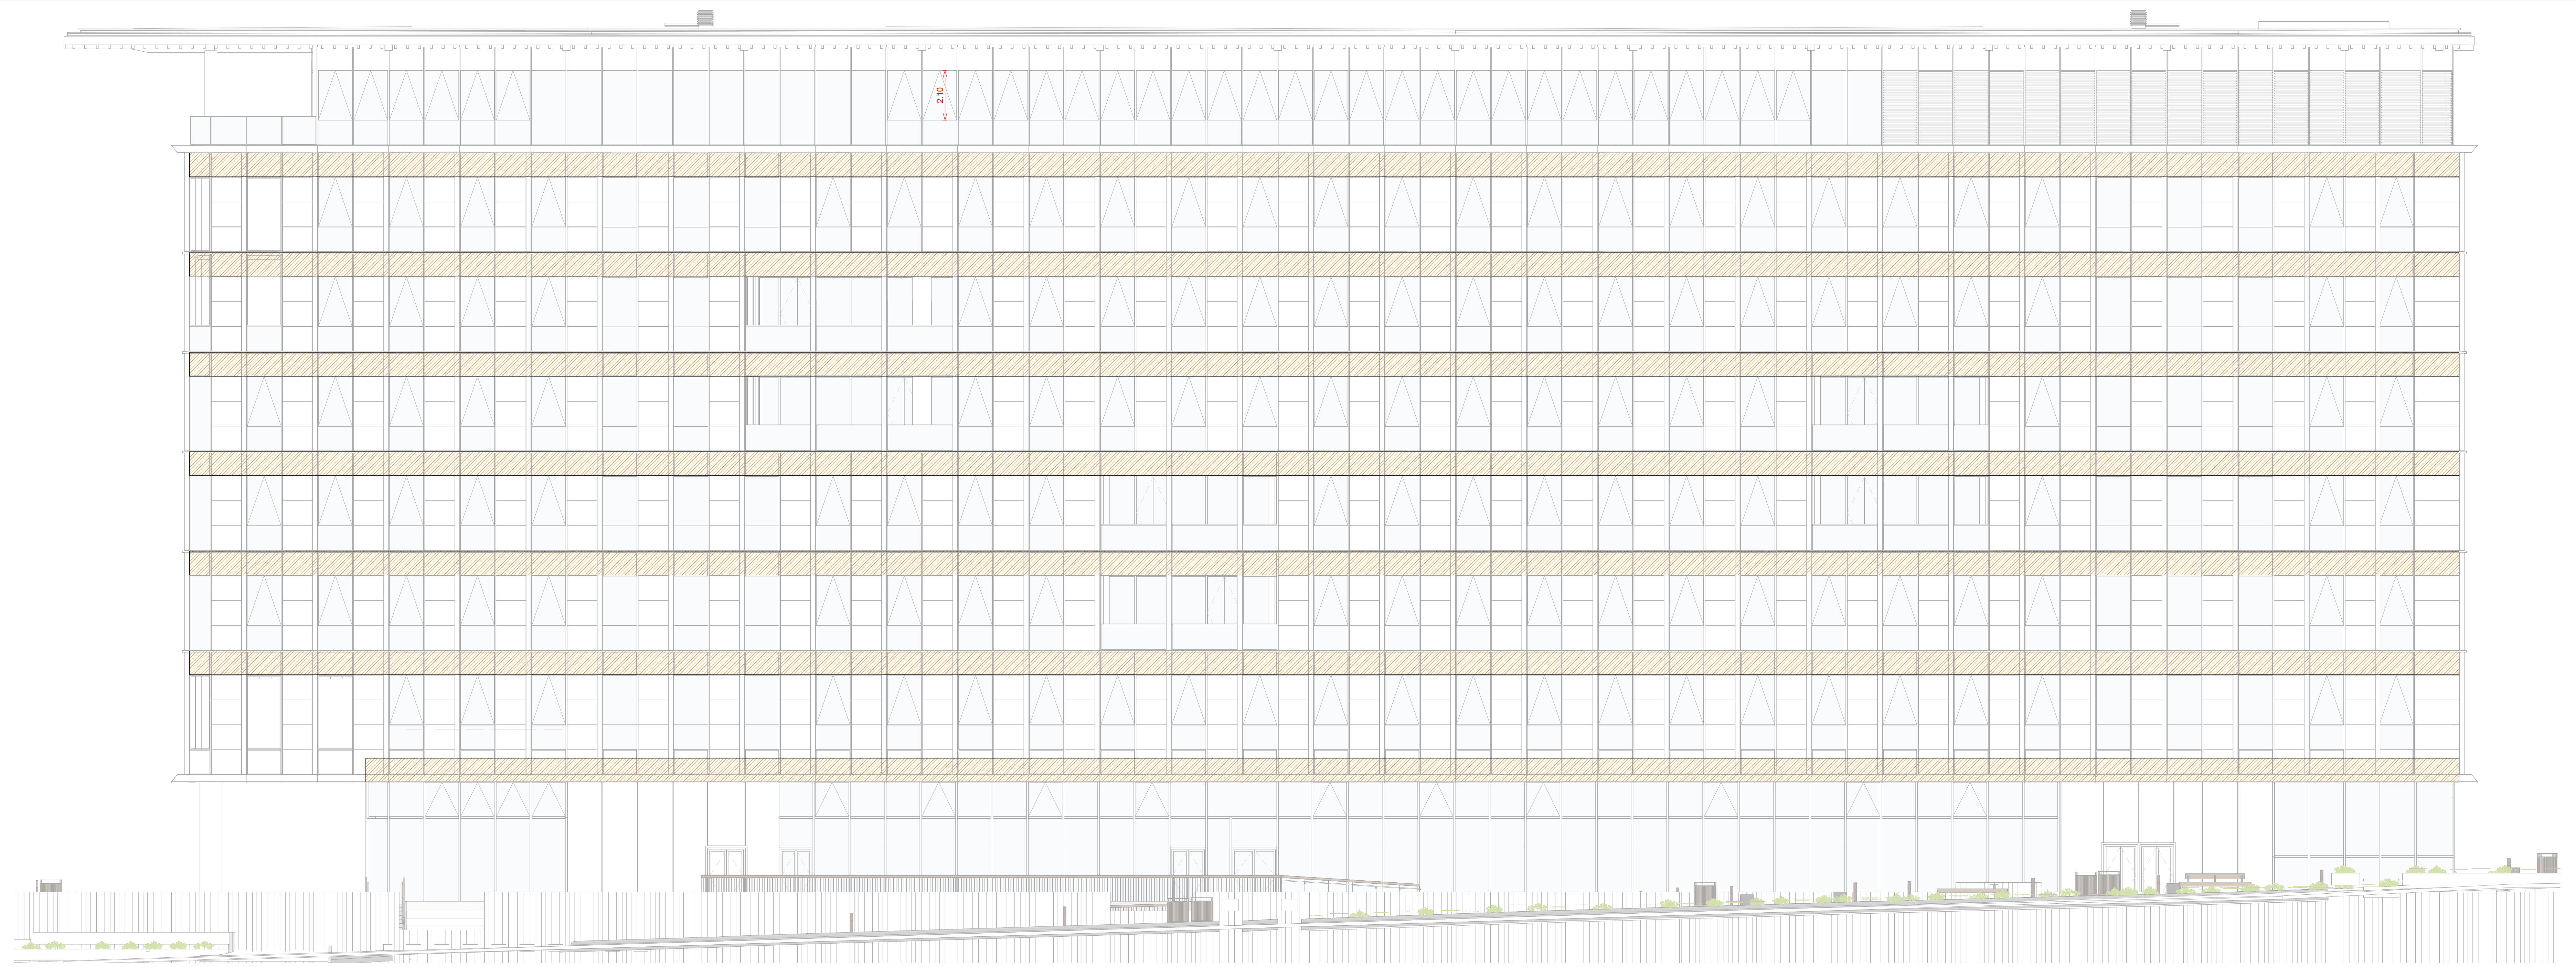

PROSPETTO VIALE SHAKESPEARE - Scala 1 : 100

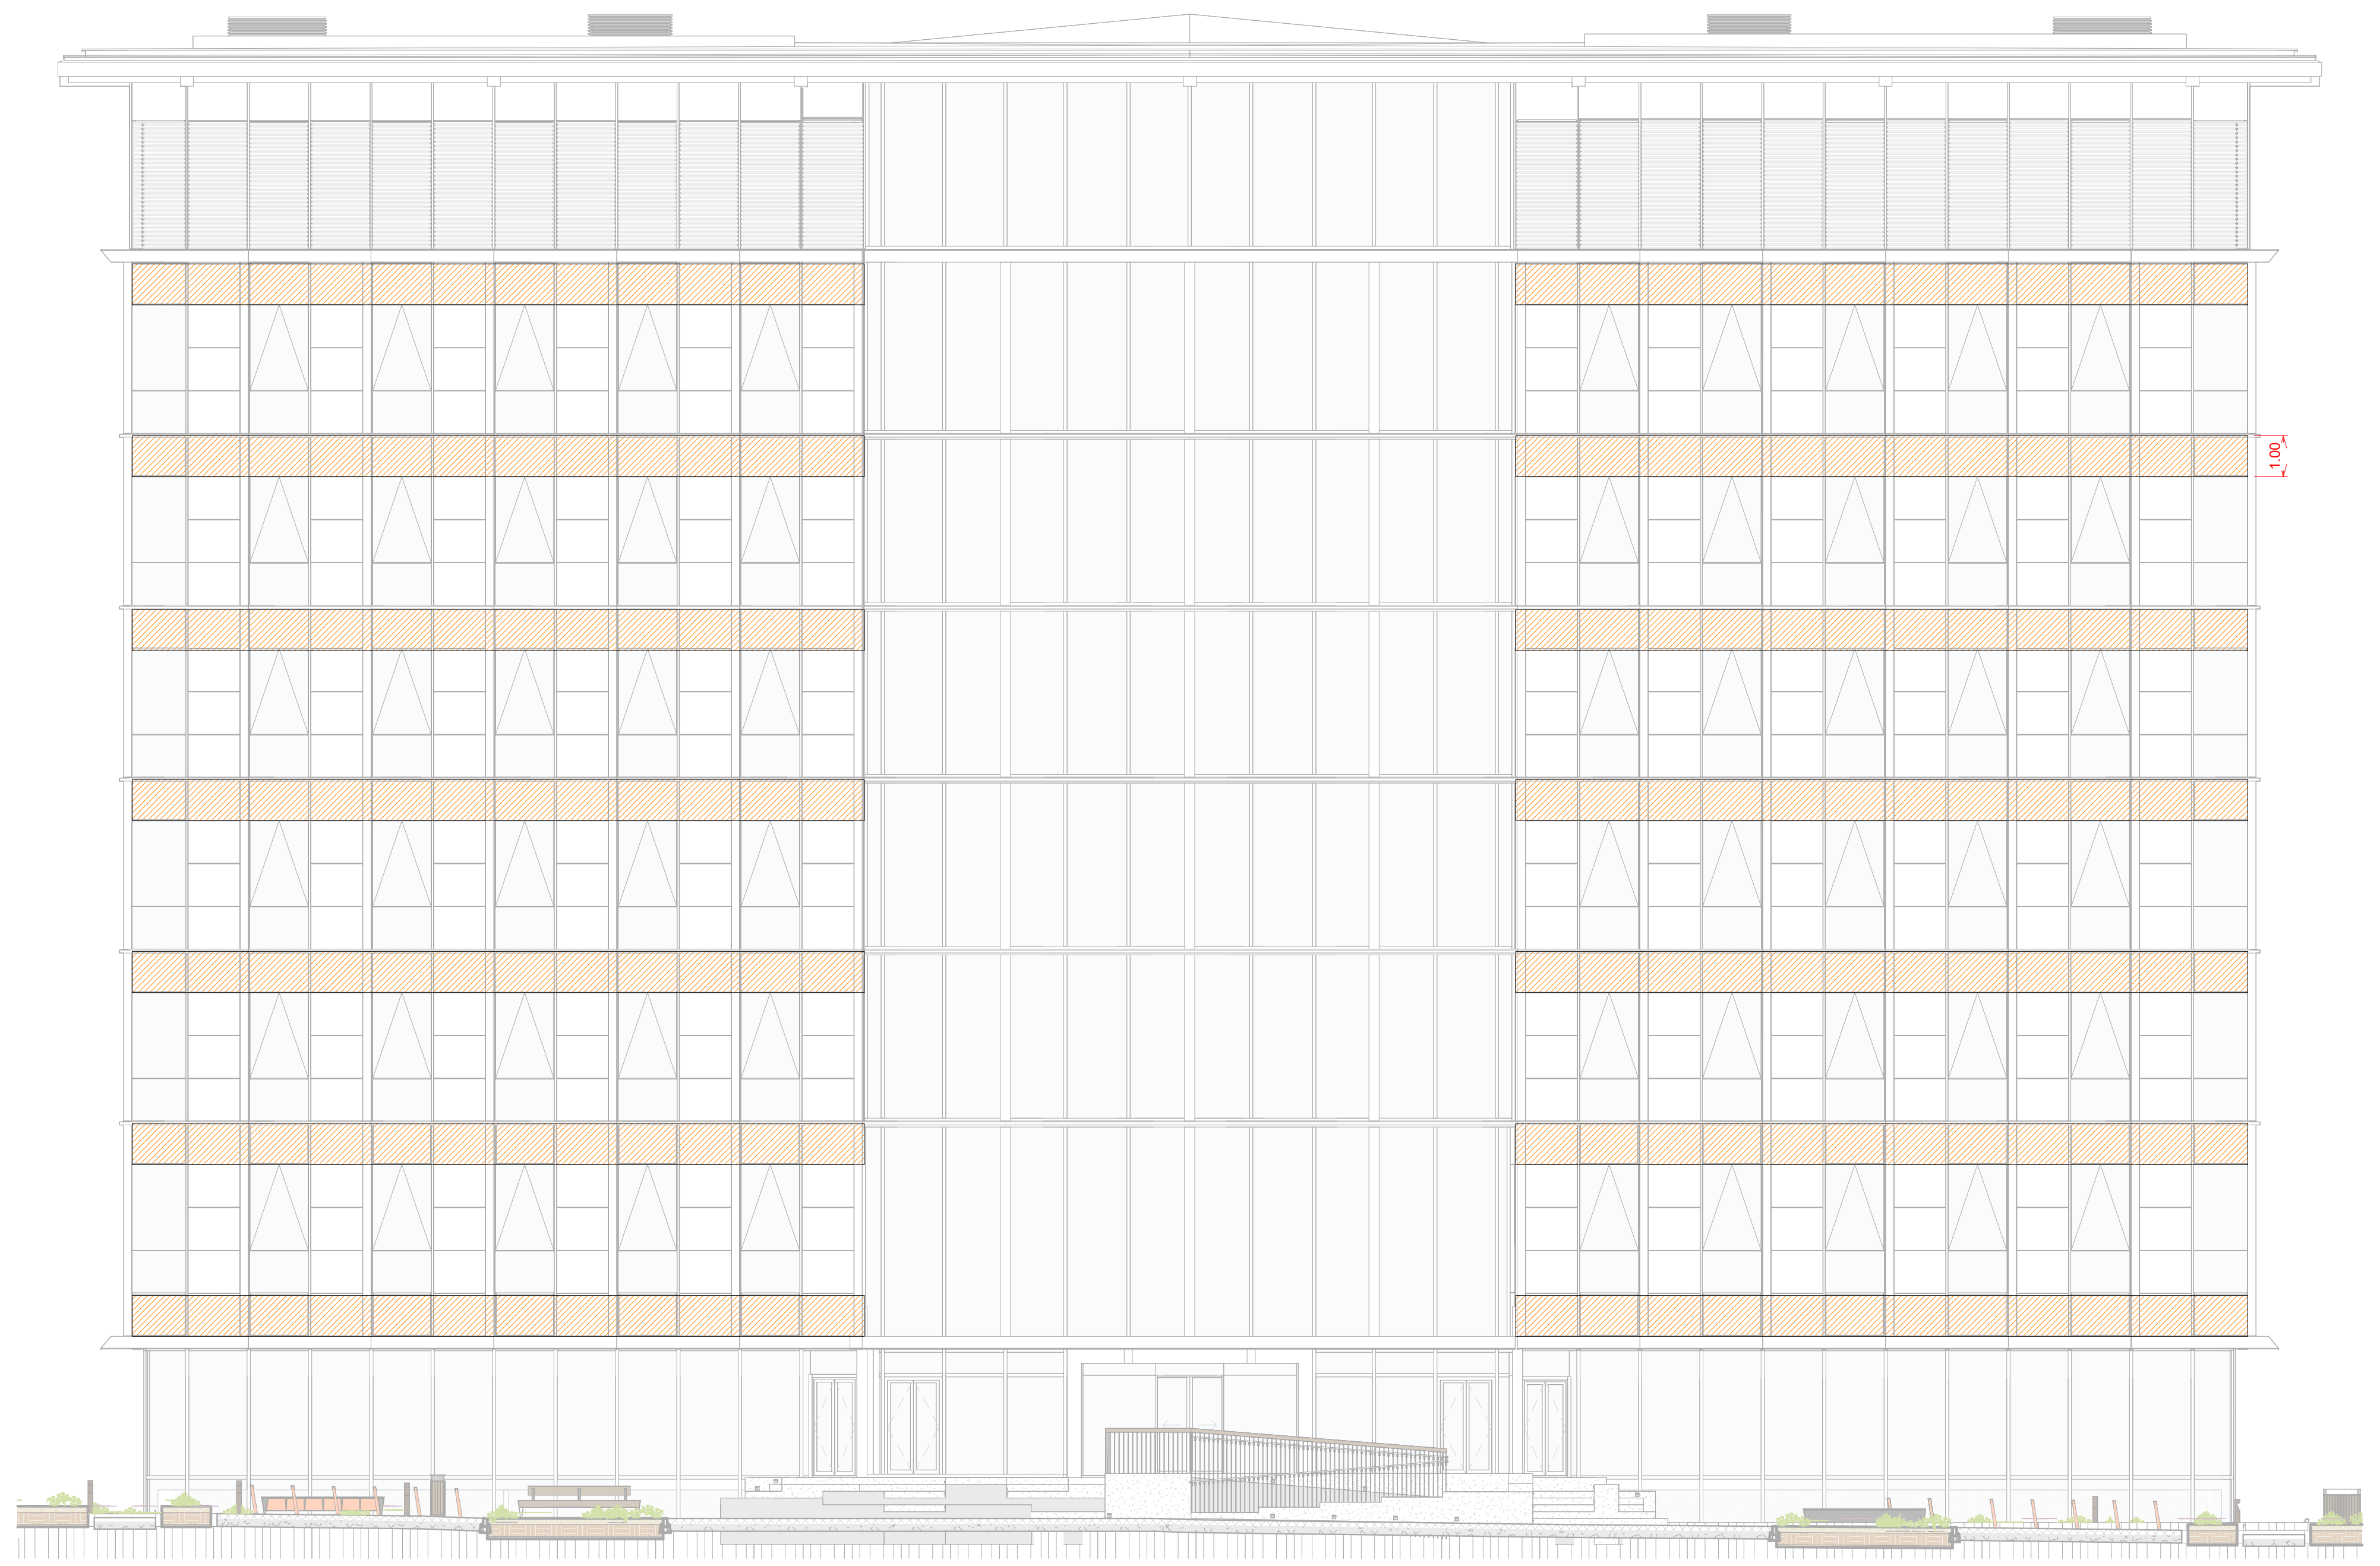

PROSPETTO VIALE EUROPA - Scala 1 : 100

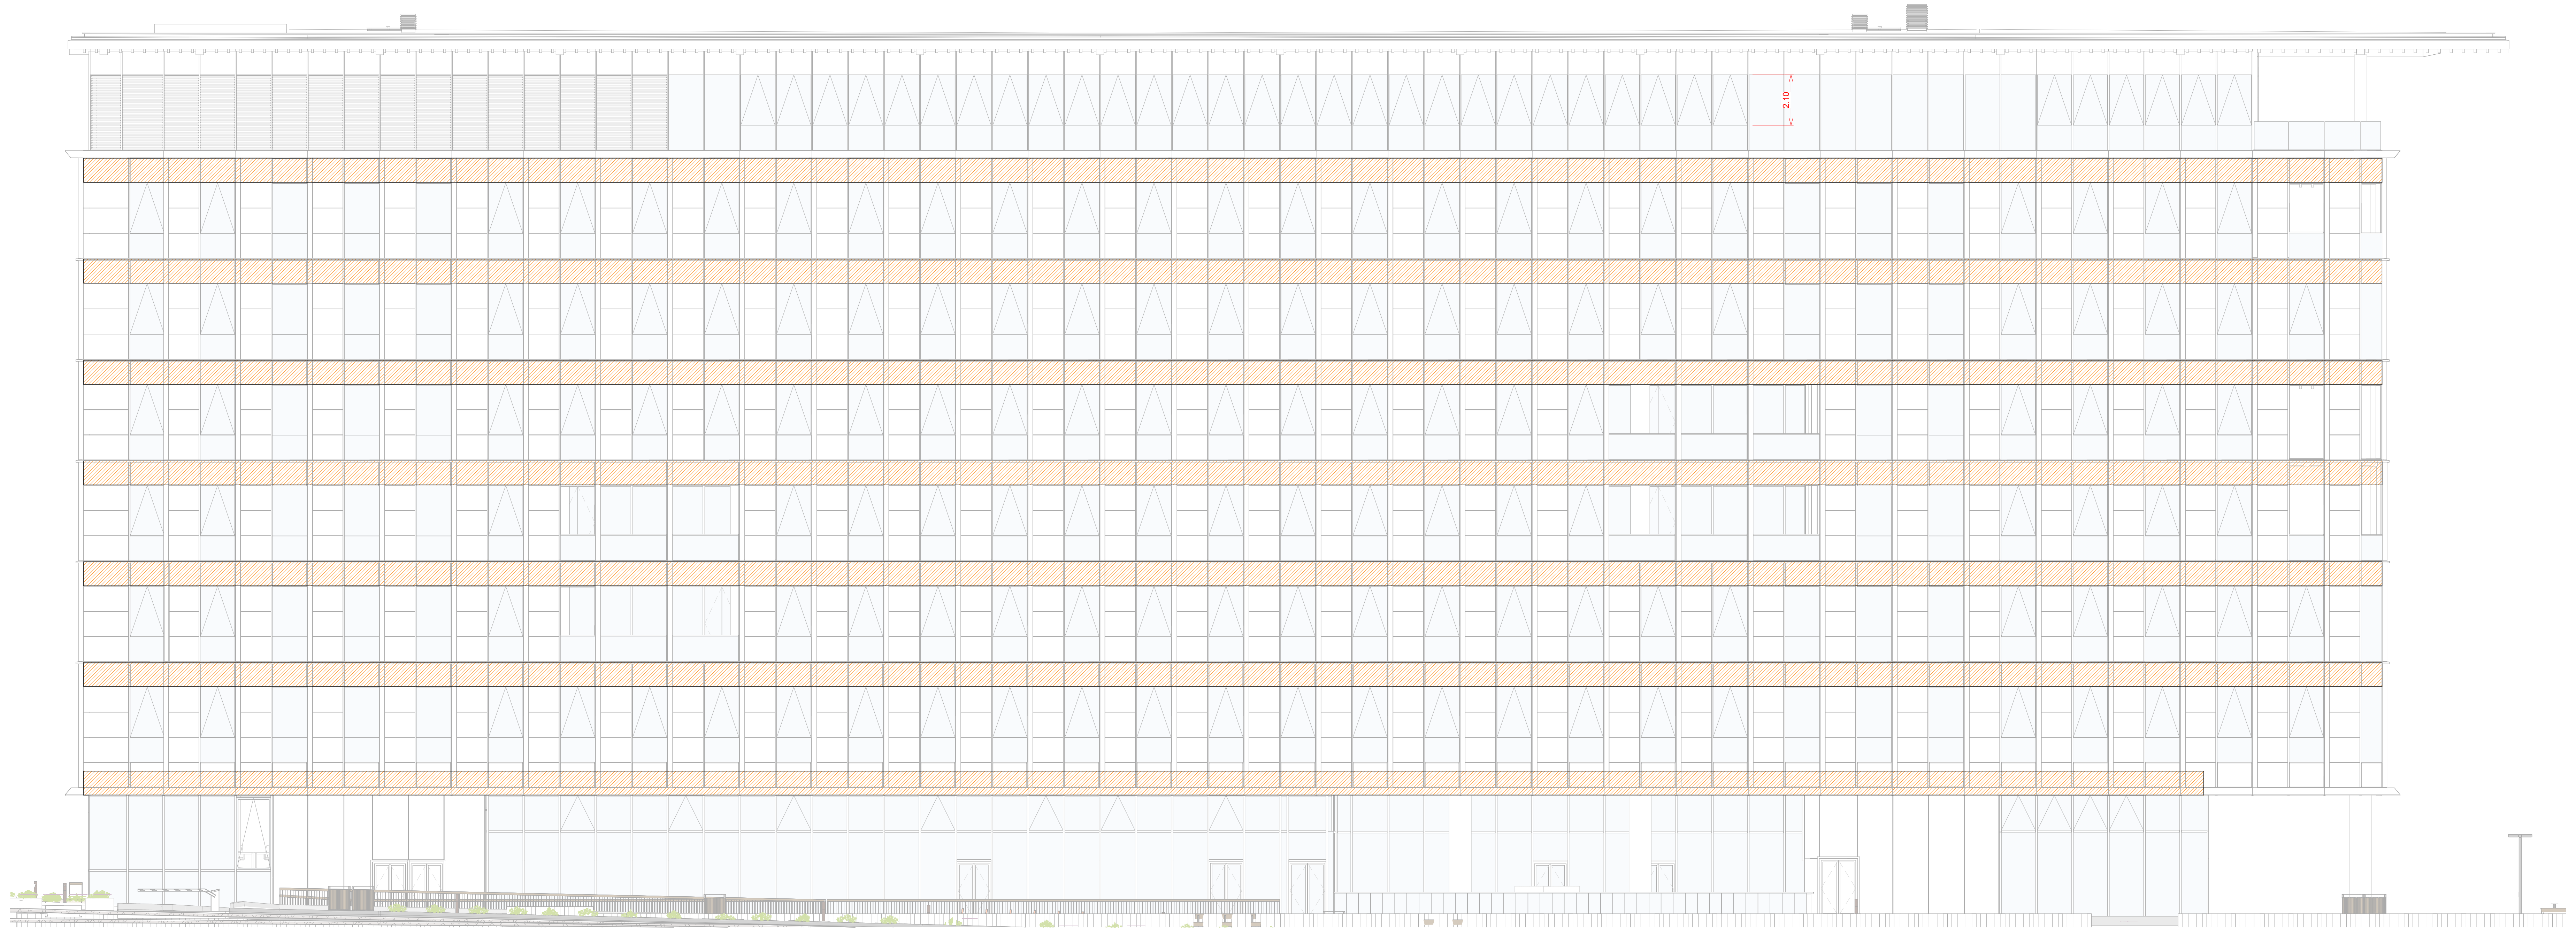

PROSPETTO VIALE BOSTON - Scala 1 : 100

LEGENDA ANTINCENDIO

▨	Parete REI 60	⇨	Percorso di esodo orizzontale
▬	Porta REI 60	➡	Percorso di esodo verticale
▨	Parete REI 30	⇨	Corridoio cieco
▬	Porta REI 30	E CO₂	Estintore a CO2
▨	Parete REI 90	E	Estintore a polvere
▬	Porta REI 90	PAI	Pannello allarme incendi
▨	Parete REI 120	◙	Pulsante antincendio
▬	Porta REI 120	FC	Rilevatore di fumo in controsoffitto
■	Ascensore antincendio	T	Rilevatore di temperatura
■	Filtro a prova di fumo	F	Rilevatore di fumo in ambiente
■	Scala a prova di fumo	A	Rivelatore di fumo ad aspirazione a pavimento
■	Filtro antincendio	OT	Rivelatore ottico - termico
■	Aperture di smaltimento fumi e calore	C	Rivelatori ottico di fumo per canale di condizionamento
▨	Fasce di seprazione	⊗	Ripetitore luminoso
PCT◎	Pulsante di sgancio centrale tecnologica	CRI	Centrale rilevazione incendi
PFTV◎	Pulsante di sgancio impianto fotovoltaico	EVAC	Centrale EVAC
PSG◎	Pulsante di sgancio generale	▣	Impianto di comunicazione bidirezionale
☒	Illuminazione di emergenza uscita di emergenza	▣	Diffusore acustico a parete
☒	Illuminazione di emergenza	▯	Diffusore acustico a parete a colonna
◙	Pulsante blocco estinzione - Impianto aerosol	▭	Diffusore acustico a parete bidirezionale
◙	Pulsante estinzione manuale - Impianto aerosol	V	Attacco di mandata doppio
☐	Impianto di spegnimento automatico ad aerosol	●	Idrante a muro UNI 45
TX	Rilevazione fumi automatica di tipo lineare	▲	Idrante esterno UNI 70

APPROVAZIONE COMMITTENTE

A - APPROVATO

B - APPROVATO CON COMMENTI

C - NON APPROVATO

Rev.	Data	Descriz.	Red.	Ver.	App.
0	05/10/2026	PRIMA EMISSIONE			

SCALA

SEDE PROGETTO
VIALE BOSTON 25
Comune di ROMA, RM - 00144

NUMERO PROGETTO
RMB1284

STATO
P

FASE PROGETTUALE:
PFTE

RTP:

Mandataria:
Progetto strutturale
via Leone X 3
50129 Firenze
+39 055 468291
info@gpapartners.com

Mandante:
Progetto architettonico
The White Chapel Building, 10
Whitechapel High Street Londra, E1 8QS,
United Kingdom
+44 (0)20 3006 3900
info@plparchitecture.com

Mandante:
Progetto architettonico
Via San Vito, 26
20123 Milano, Italia
+39 328 841 0677
office@oblyk.studio

Mandante:
Progetto impianti
Via Cavour, 4
70027 Palo del Colle (BA)
+39 080 8594347
info@studioperillo.eu

Mandante:
Responsabile progettazione sostenibile dell'oopera
Via Giuseppe Verdi, 26
63822 Porto San Giorgio (FM)
+39 0734674423
info@valentiniarchitetture.com

Mandante:
Via Beccarini, 29
48018 Faenza (RA)
+39 0546663423
ingegneria@enser.it

PROGETTO:
CIG: B4C1AD81FA CUP: G84H22000360001

Realizzazione della nuova sede del Ministero dell'Ambiente e della Sicurezza Energetica "MASE"

Codice bene: RMB1284
Codice fabbricato: RM0411001

TITOLO

PROSPETTI

AGENZIA DEL DEMANIO
Struttura per la progettazione
Via Barberini 38, 00187, Roma
RUP: Arch. Isabella Di Marsico
DEC: Ing. Benedetto Grivo

AGENZIA DEL DEMANIO

NOME FILE
RMB1284-ADD-PROSPETTI-ZZ-DR-I-PN0001

REV
0
05/10/2026