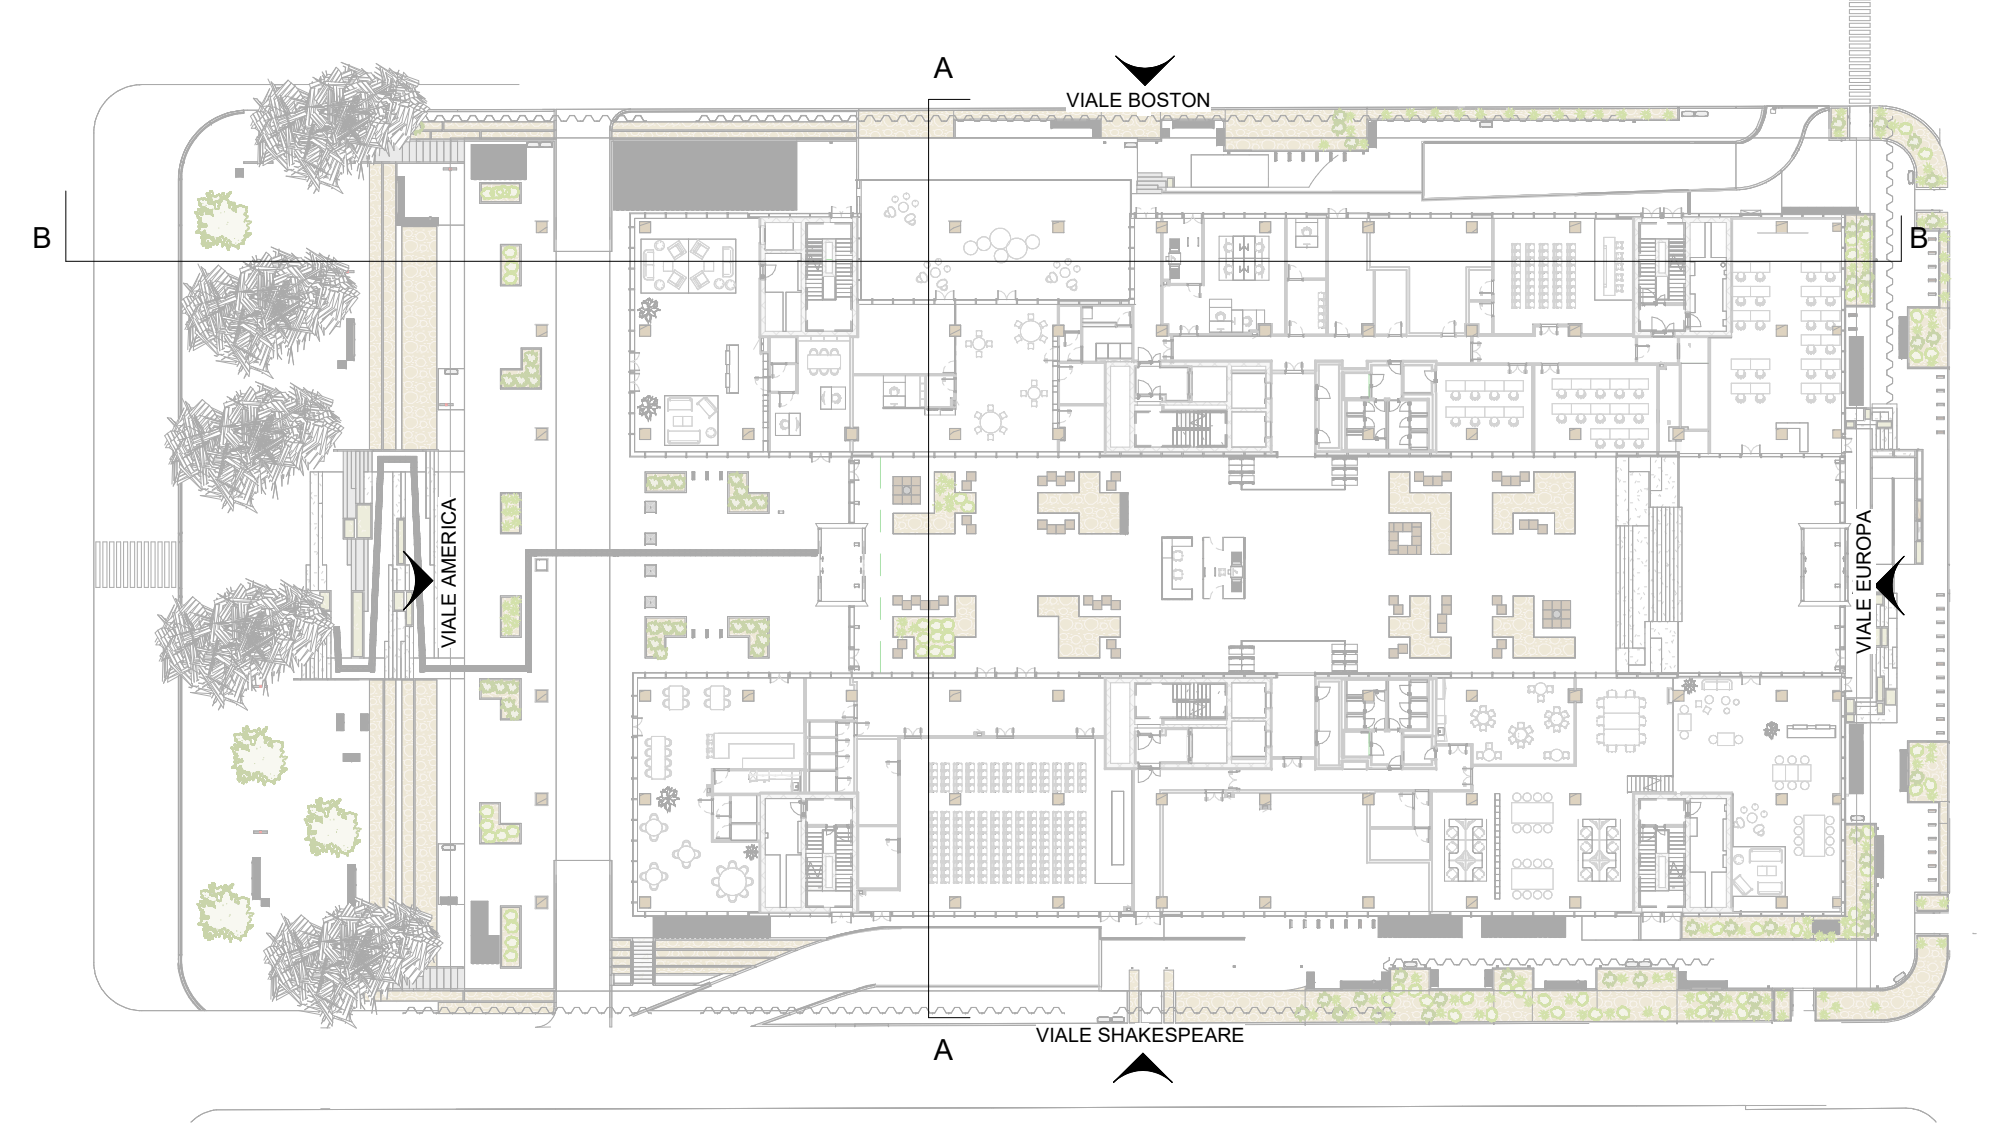

KEYPLAN SEZIONI - Scala 1 : 500

LEGENDA ANTINCENDIO			
🟩	Parete REI 60	⇨	Percorso di esodo orizzontale
🟩	Porta REI 60	➡	Percorso di esodo verticale
🟦	Parete REI 30	⇨	Corridoio cieco
🟦	Porta REI 30	E CO2	Estintore a CO2
🟪	Parete REI 90	E	Estintore a polvere
🟪	Porta REI 90	PAI	Pannello allarme incendi
🟥	Parete REI 120	◉	Pulsante antincendio
🟥	Porta REI 120	FC	Rilevatore di fumo in controsoffitto
🟧	Ascensore antincendio	T	Rilevatore di temperatura
🟦	Filtro a prova di fumo	F	Rilevatore di fumo in ambiente
🟩	Scala a prova di fumo	A	Rivelatore di fumo ad aspirazione a pavimento
🟨	Filtro antincendio	OT	Rivelatore ottico - termico
🟦	Aperture di smaltimento fumi e calore	C	Rivelatori ottico di fumo per canale di condizionamento
▨	Fasce di seprazione	⊗	Ripetitore luminoso
PCT◎	Pulsante di sgancio centrale tecnologica	CRI	Centrale rilevazione incendi
PFTV◎	Pulsante di sgancio impianto fotovoltaico	EVAC	Centrale EVAC
PSG◎	Pulsante di sgancio generale	▣	Impianto di comunicazione bidirezionale
⊠	Illuminazione di emergenza uscita di emergenza	▣	Diffusore acustico a parete
⊠	Illuminazione di emergenza	▯	Diffusore acustico a parete a colonna
◉	Pulsante blocco estinzione - Impianto aerosol	▭	Diffusore acustico a parete bidirezionale
◉	Pulsante estinzione manuale - Impianto aerosol	⊻	Attacco di mandata doppio
▢	Impianto di spegnimento automatico ad aerosol	●	Idrante a muro UNI 45
TX	Rilevazione fumi automatica di tipo lineare	▲	Idrante esterno UNI 70

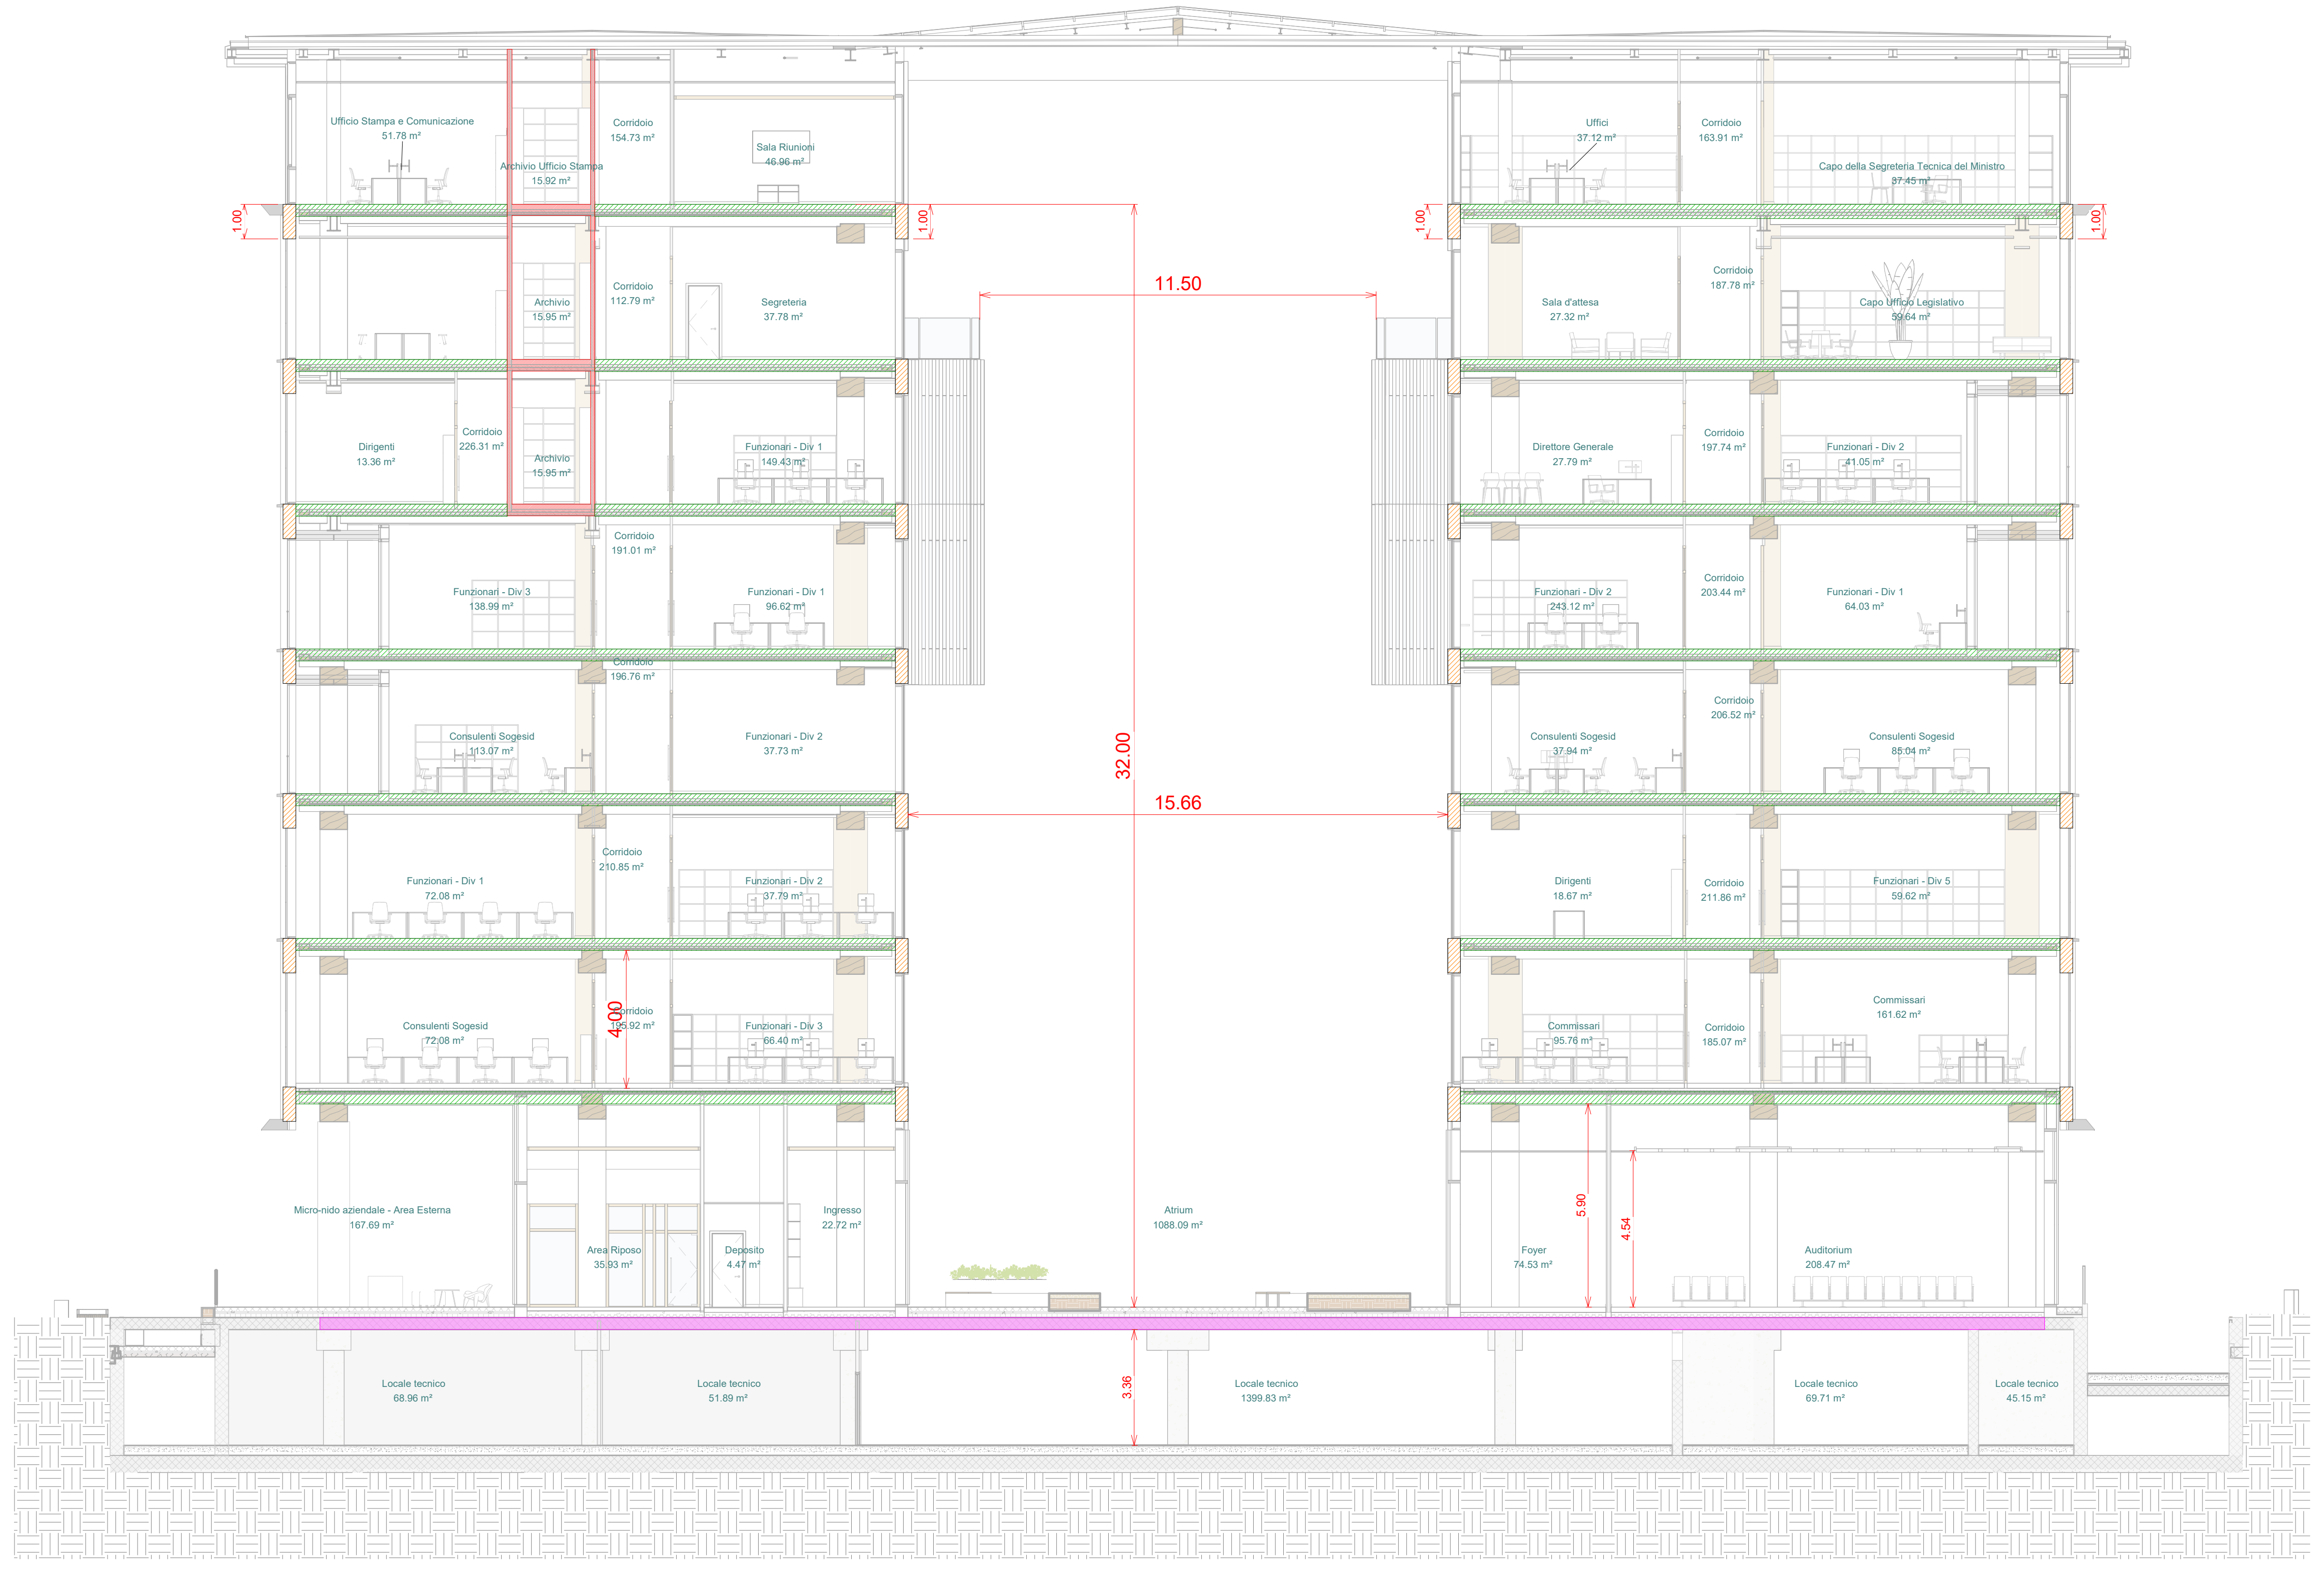

SEZIONE A-A - Scala 1 : 100

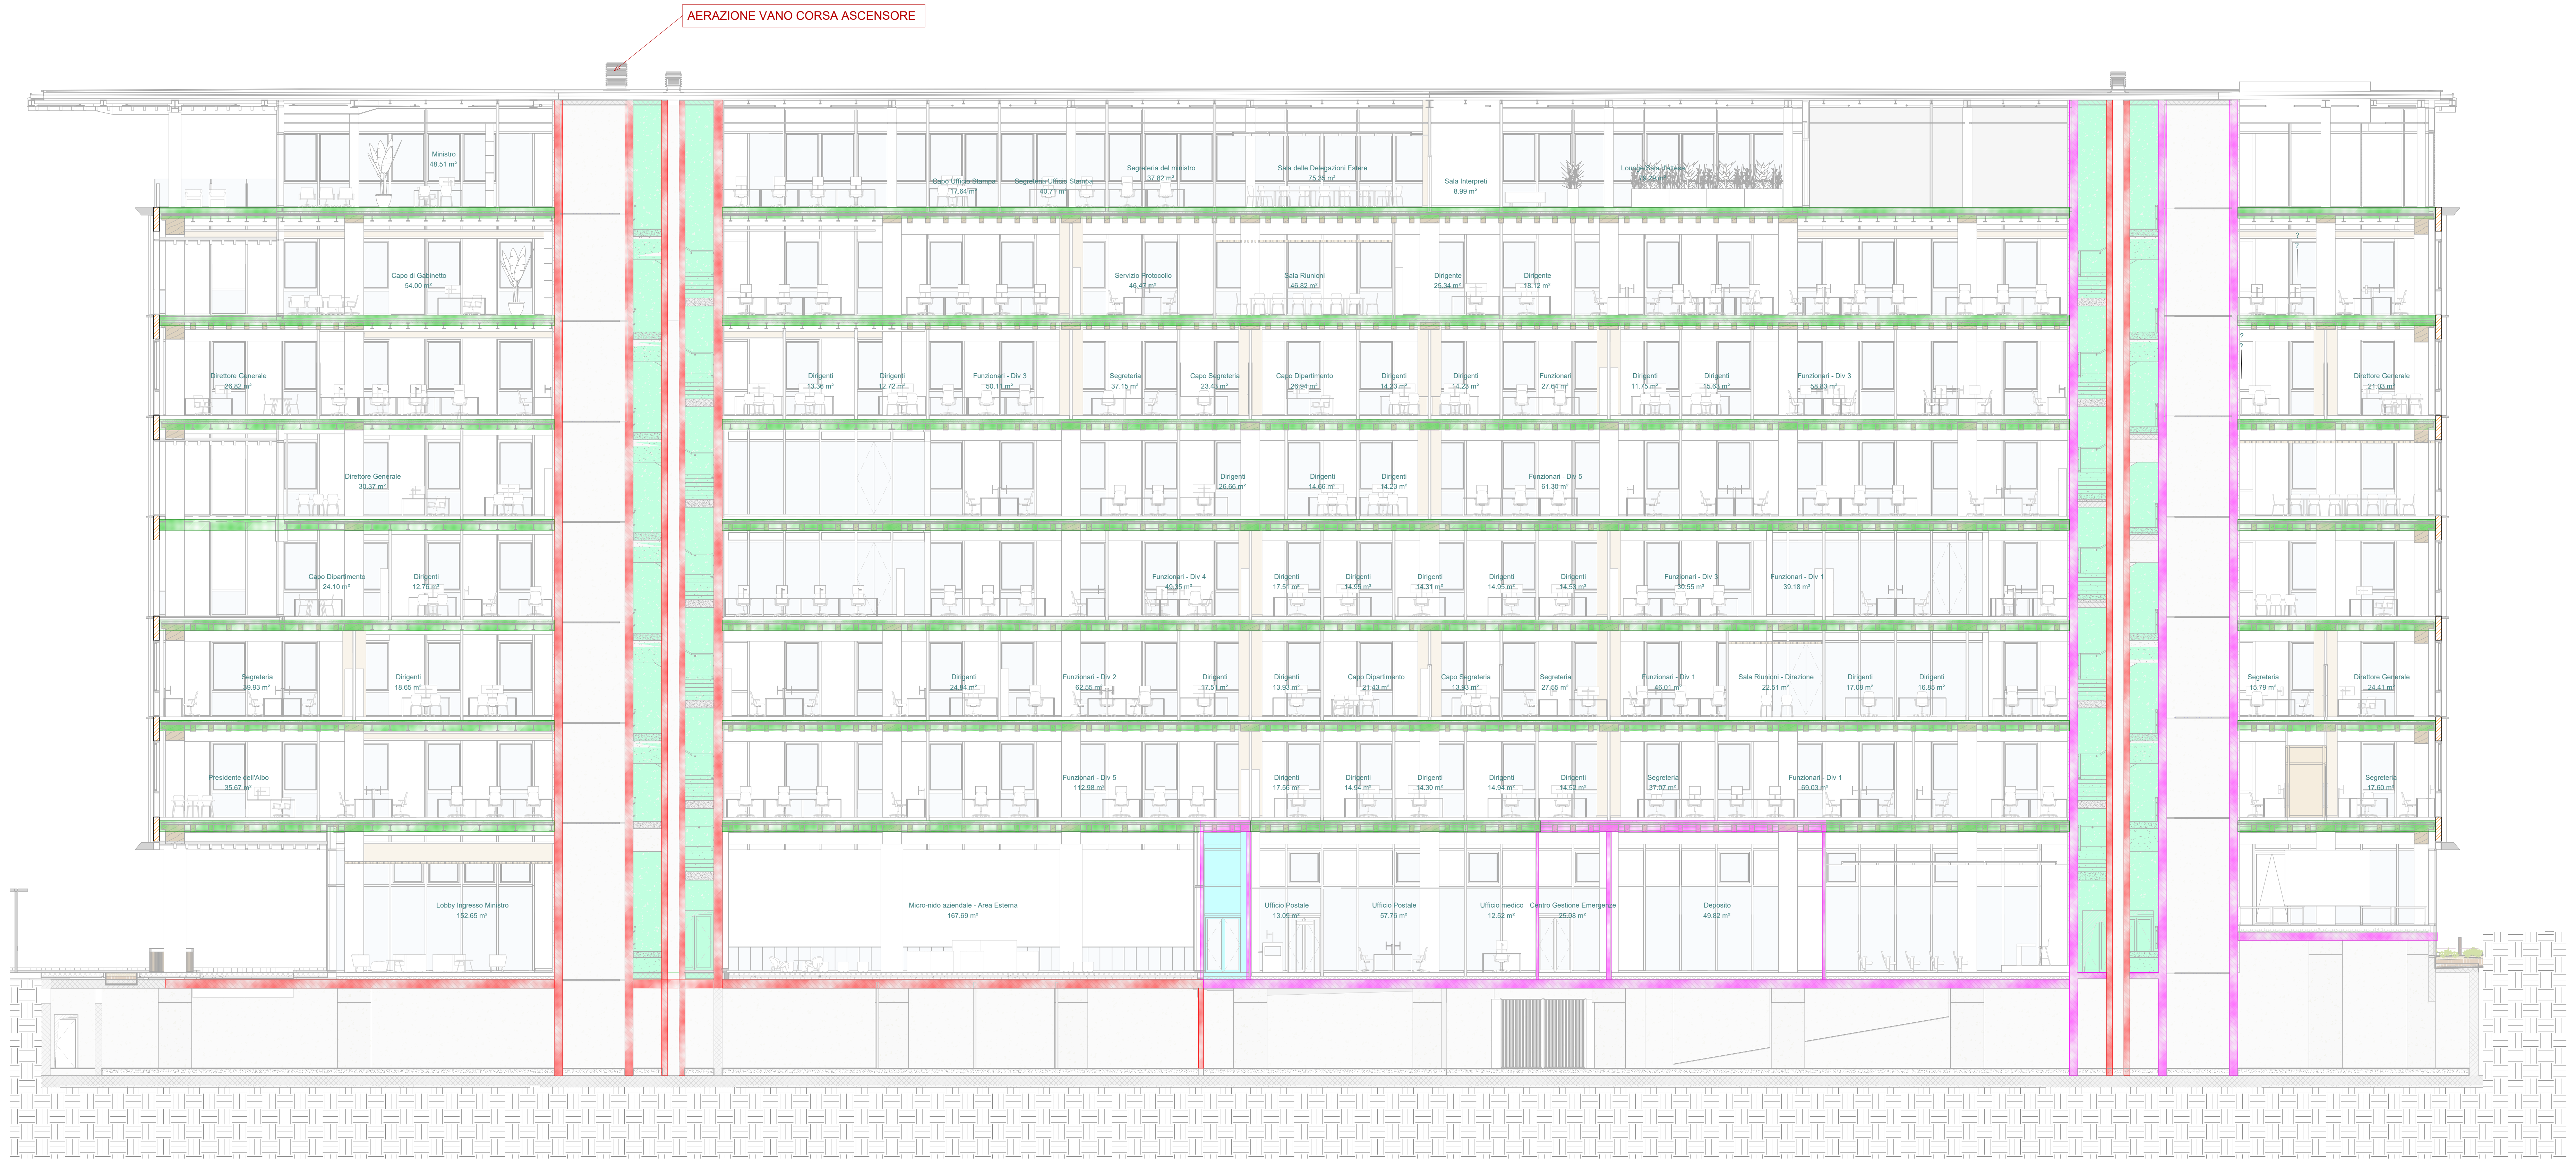

SEZIONE B-B - Scala 1 : 100

APPROVAZIONE COMMITTENTE	
	A - APPROVATO
	B - APPROVATO CON COMMENTI
	C - NON APPROVATO

Rev.	Data	Descriz.	Red.	Ver.	App.
0	05/10/2026	PRIMA EMISSIONE			

SCALA

SEDE PROGETTO
VIALE BOSTON 25
Comune di ROMA, RM - 00144

NUMERO PROGETTO
RMB1284

STATO
P

FASE PROGETTUALE:
PFTE

RTP:

Mandataria:	**Mandante:**	**Mandante:**	**Mandante:**	**Mandante:**	**Mandante:**
Progetto strutturale	Progetto architettonico	Progetto architettonico	Progetto impianti	Responsabile progettazione sostenibile dell'oopera	
GPA PARTNERS	PLP/ARCHITECTURE	OBLYK		VALENTINI architetture	enser
via Leone X 3 50129 Firenze +39 055 468291 info@gpapartners.com	The White Chapel Building, 10 Whitechapel High Street Londra, E1 8QS, United Kingdom +44 (0)20 3006 3900 info@plparchitecture.com	Via San Vito, 26 20123 Milano, Italia +39 328 841 0677 office@oblyk.studio	Via Cavour, 4 70027 Palo del Colle (BA) +39 080 8594347 info@studioperillo.eu	Via Giuseppe Verdi, 26 63822 Porto San Giorgio (FM) +39 0734674423 info@valentiniarchitetture.com	Via Beccarini, 29 48018 Faenza (RA) +39 0546663423 ingegneria@enser.it

PROGETTO: CIG: B4C1AD81FA CUP: G84H22000360001

Realizzazione della nuova sede del Ministero dell'Ambiente e della Sicurezza Energetica
“MASE”

Codice bene: RMB1284
Codice fabbricato: RM0411001

TITOLO

SEZIONI

AGENZIA DEL DEMANIO
Struttura per la progettazione
Via Barberini 38, 00187, Roma
RUP: Arch. Isabella Di Marsico
DEC: Ing. Benedetto Grivo

AGENZIA DEL DEMANIO

NOME FILE
RMB1284-ADD-SEZIONEIS-ZZ-DR-I-PN0001

REV
0
05/10/2026