
VIABILITA' DI CANTIERE
Scala 1:200

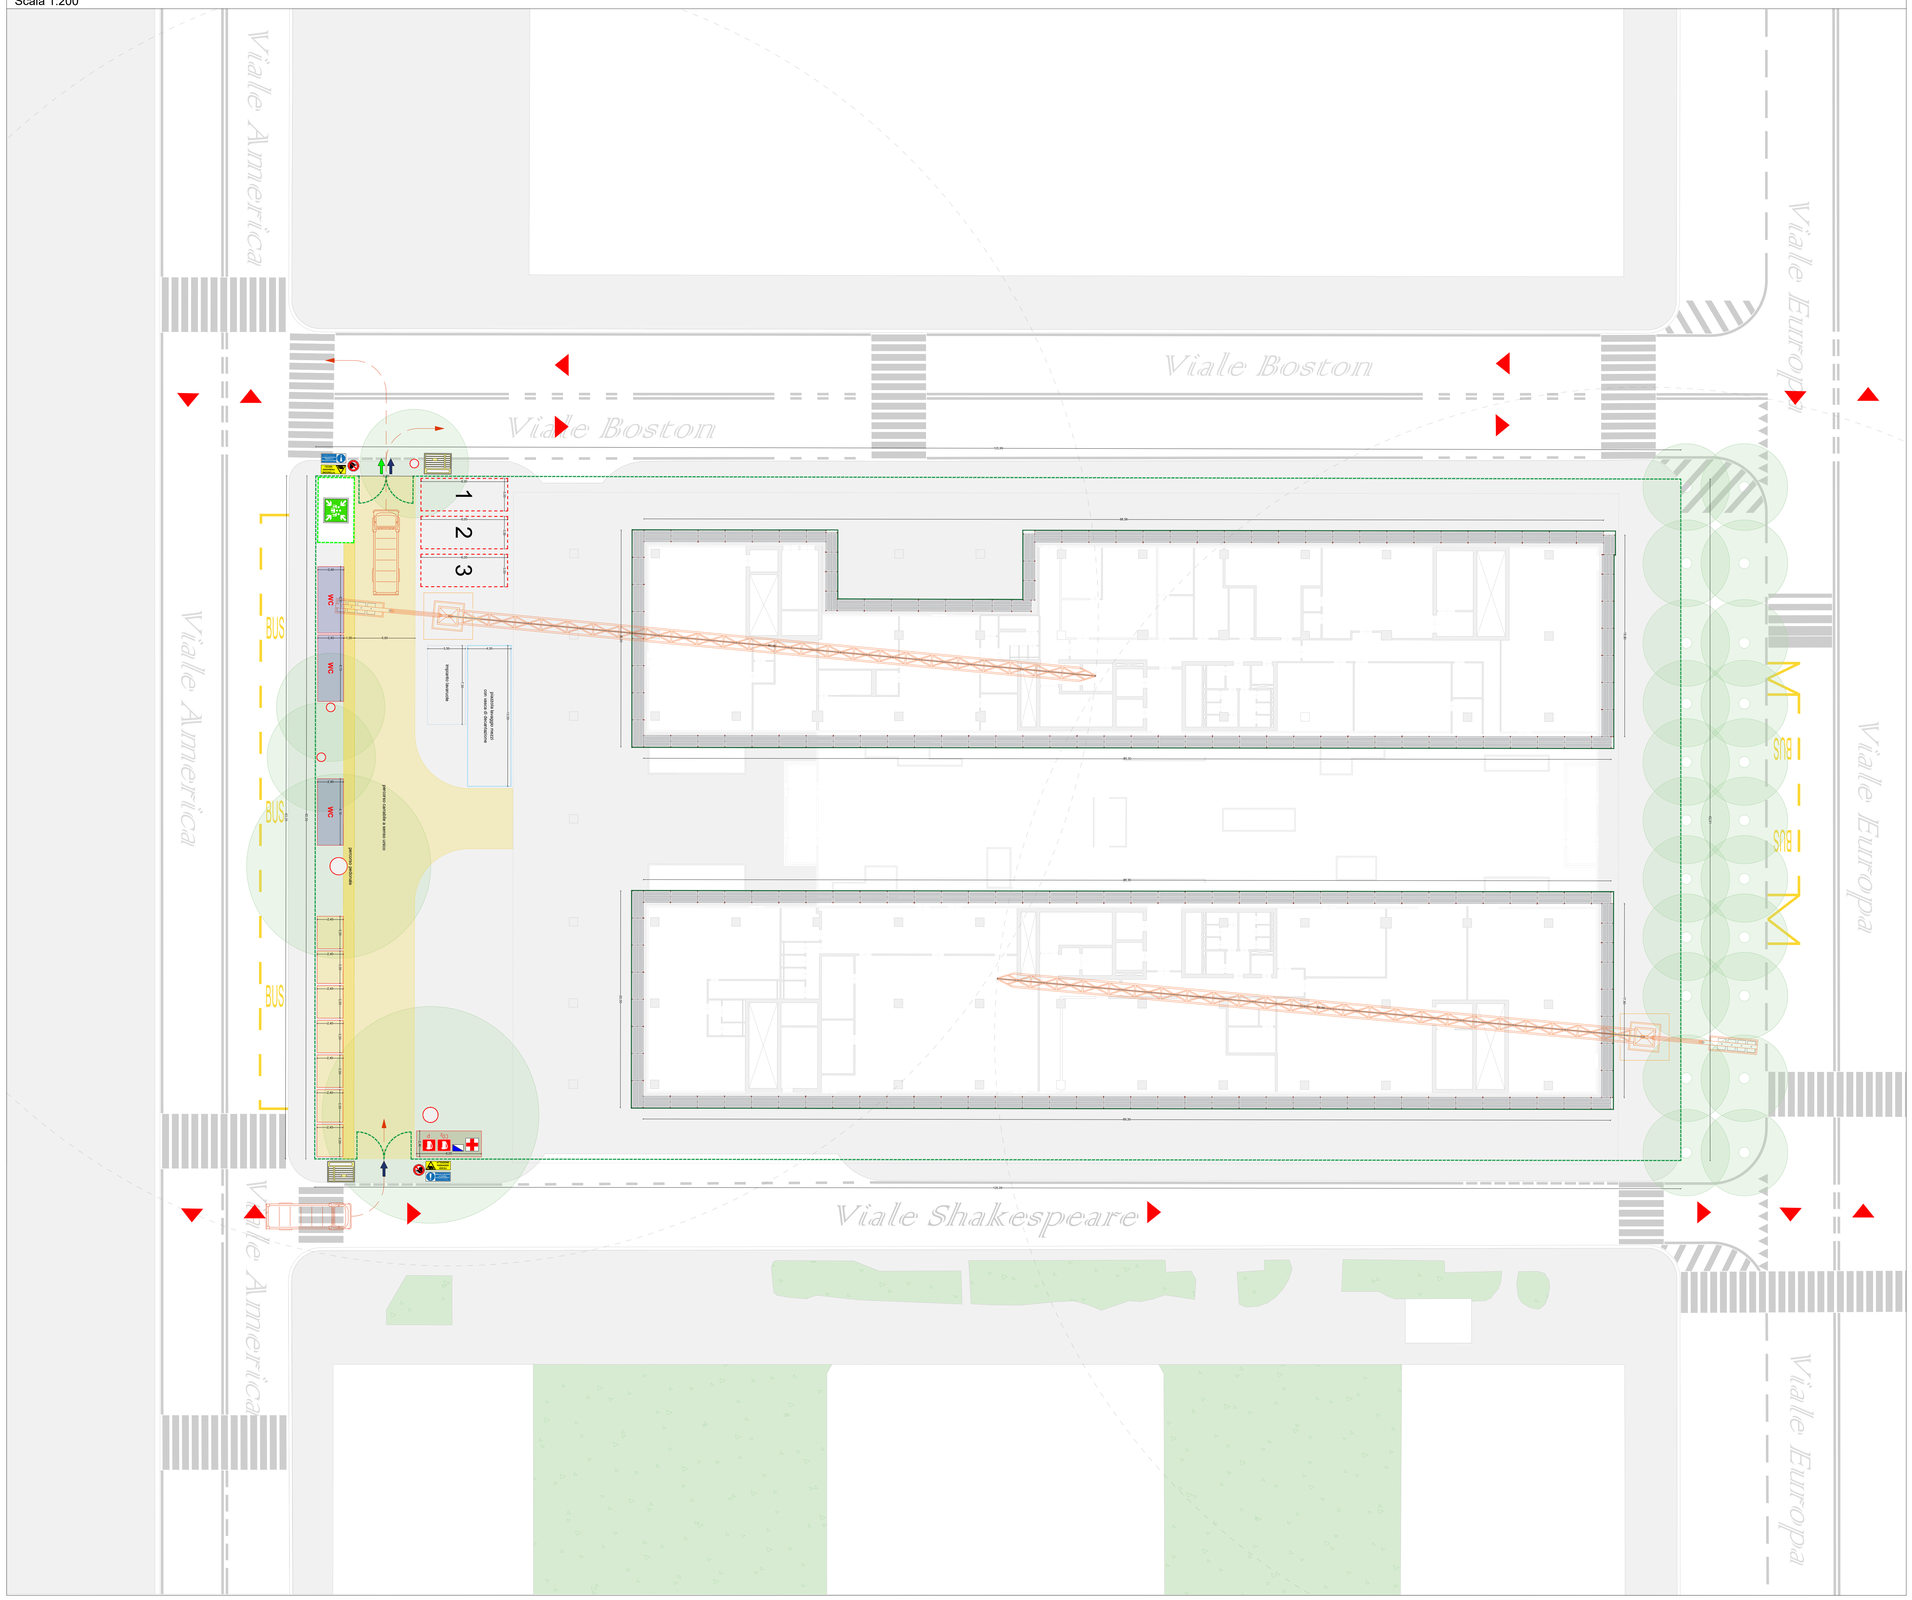

LEGENDA

	Chiusura perimetrale di cantiere - *Pannelli ciechi in legno e metallo per aree urbane, predisposte ad allestimenti pubblicitari o disegni da arredo urbano*
	Accesso al cantiere - *Dovrà obbligatoriamente essere dotato di serratura o di lucchetto di sicurezza corazzato con chiave non riproducibile*
	Quadro elettrico di cantiere
WC	Bagni M/F di cantiere [n. 3] - *Dimensioni (L × P × H): 6,10 × 2,40 × 2,30 mt*
	Box di cantiere uso UFFICIO [n. 1] - *Dimensioni (L × P × H): 6,00 × 2,40 × 2,40 mt*
	Box di cantiere uso SPOGLIATOIO [n. 7] - *Dimensioni (L x P x H): 3,00 x 2,40 x 2,40 mt*
	Ponteggio metallico a telaio prefabbricato
	Rete di contenimento polveri per ponteggi
1	Isola ecologica - Tettoia realizzata con elementi tubolari di ponteggio con copertura in tavole di legno
2	Deposito materiali pericolosi - Tettoia realizzata con elementi tubolari di ponteggio con copertura in tavole di legno
3	Isola materiali da posare - Tettoia realizzata con elementi tubolari di ponteggio con copertura in tavole di legno
	Area destinata a punto di raccolta
	Ingresso / uscita di cantiere
	Direzione da seguire in caso di emergenza
	Cartellone informativo dei lavori
	Cartello di segnalazione: PERICOLO
ATTENZIONE PASSAGGIO VEICOLI	Cartello di segnalazione: PERICOLO PASSAGGIO VEICOLI
	Cartello di segnalazione: DIVIETO DI ACCESSO AI NON ADDETTI AI LAVORI
	Cartello di segnalazione: CONTROLLO ACCESSI
	Protezione alberature con gabbia in tavole in legno con interposto materiale cuscinetto
	Senso di marcia

APPROVAZIONE COMMITTENTE

	A - APPROVATO
	B - APPROVATO CON COMMENTI
	C - NON APPROVATO

Rev.	Data	Descriz.	Red.	Ver.	App.
00	05/10/2026	Prima Emissione			

SCALA

SEDE PROGETTO
VIALE BOSTON 25
Comune di ROMA, RM - 00144

NUMERO PROGETTO
RMB1284

STATO
P

FASE PROGETTUALE:
PFTE

RTP:

Mandataria: Progetto strutturale	Mandante: Progetto architettonico	Mandante: Progetto architettonico	Mandante: Progetto impianti	Mandante: Responsabile progettazione sostenibile dell'opera	Mandante:
GPA PARTNERS Via Leone X 3 00135 Firenze +39 055 490070 info@gpapartners.com	PLP/ARCHITECTURE The White Chapel Building, 10 Whitechapel High Street, E1 8QS, United Kingdom +44 (0)20 3006 3900 info@plparchitecture.com	OBLVK Via San Vito, 26 20123 Milano, MI +39 328 841 4077 office@oblvk.studio	Via Cavour, 4 70027 Palo del Colle (BA) +39 080 8594347 info@ecodoorello.eu	Via Giuseppe Verdi, 26 63822 Porto San Giorgio (FM) +39 0734074423 info@valentinarchitetture.com	enser Via Beccarini, 29 48018 Faenza (RA) +39 0546660423 ingegneria@enser.it

PROGETTO:
CIG: B4C1AD81FA CUP: G84H22000360001

Realizzazione della nuova sede del Ministero dell'Ambiente e della Sicurezza Energetica "MASE"

Codice bene: RMB1284
Codice fabbricato: RM0411001

TITOLO

VIABILITÀ DI CANTIERE

AGENZIA DEL DEMANIO
Struttura per la progettazione
Via Barberini 38, 00187, Roma
RUP: Arch. Isabella Di Marsico
DEC: Ing. Benedetto Grivo

AGENZIA DEL DEMANIO

NOME FILE
RMB1284-ADD-PLANGENER-XX-DR-H-PN0001

REV
00
05/10/2026