LAYOUT DI CANTIERE - FASE SCAVI
Scala 1:200

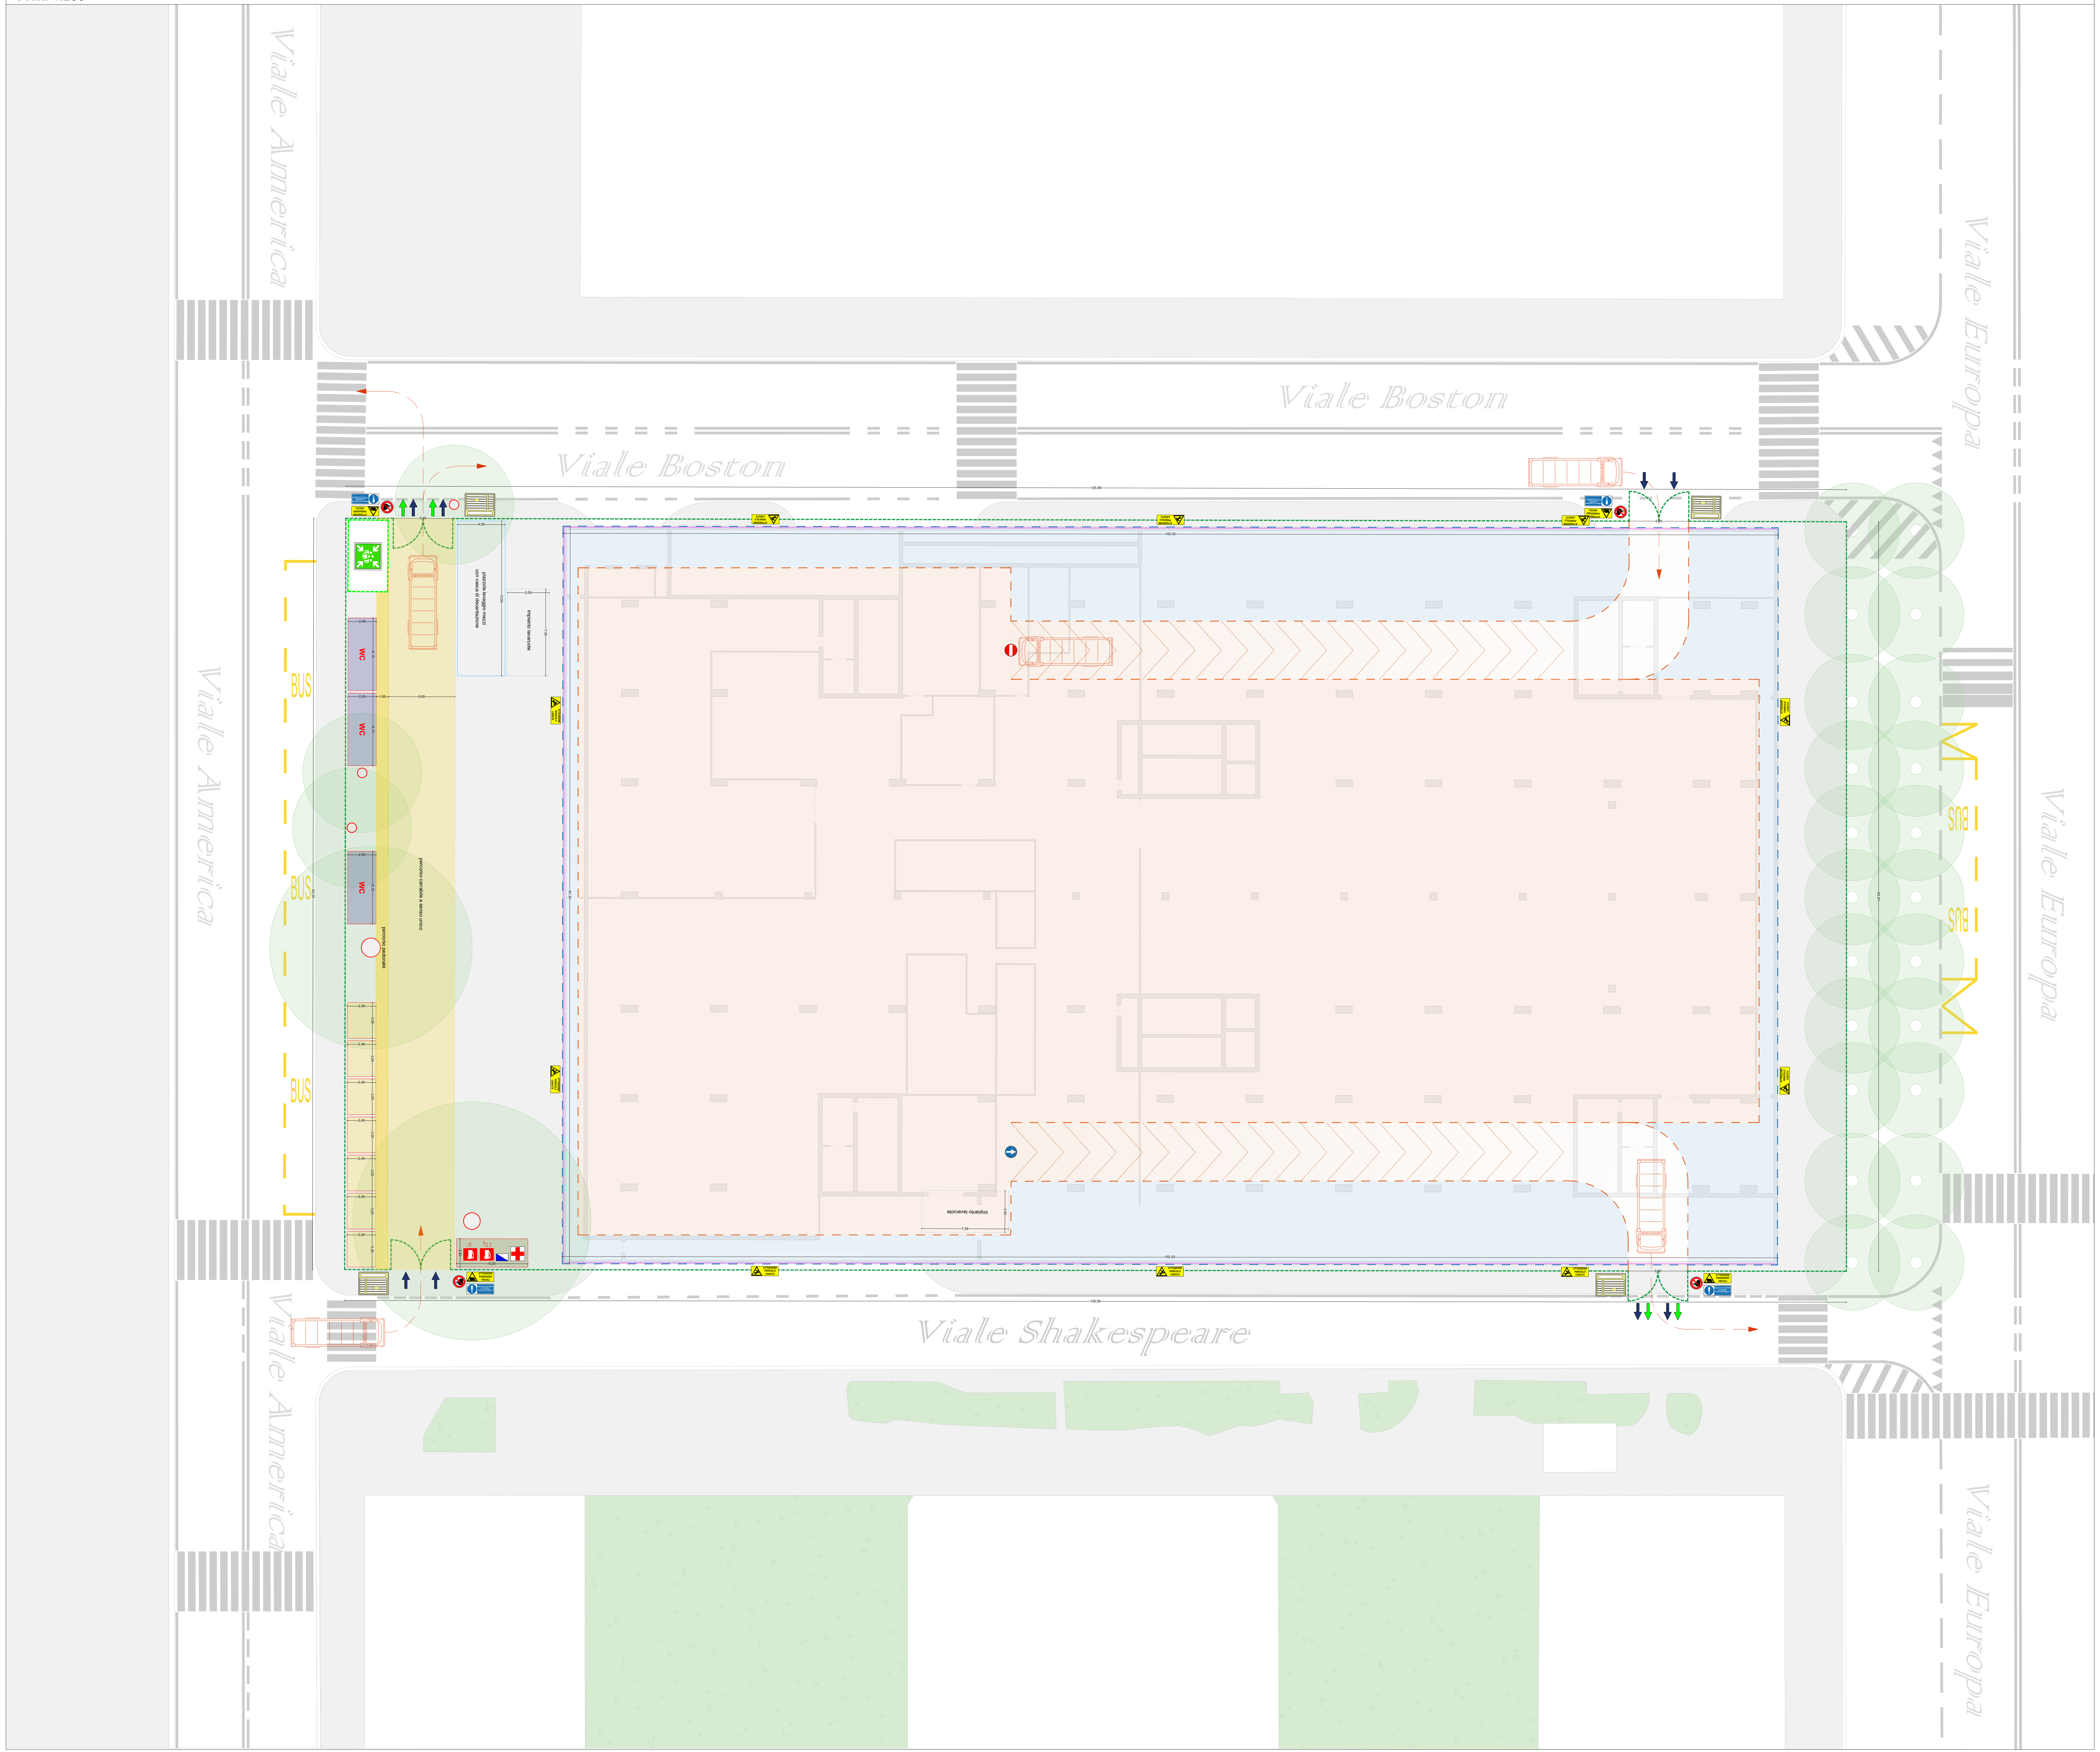

LEGENDA

- - - - -	Chiusura perimetrale di cantiere - *Pannelli ciechi in legno e metallo per aree urbane, predisposte ad allestimenti pubblicitari o disegni da arredo urbano*
◜	Accesso al cantiere - *Dovrà obbligatoriamente essere dotato di serratura o di lucchetto di sicurezza corazzato con chiave non riproducibile*
- - - - -	Parapetto provvisorio su bordo scavo rinveniente dalle demolizioni del vecchio fabbricato - *Esistente*
▭	Area di scavo rinveniente dalla demolizione del vecchio fabbricato - *Esistente*
≫	Rampa di accesso / uscita scavo rinveniente dalla demolizione del vecchio fabbricato - *Esistente*
▭	Area di scavo per realizzazione nuovo fabbricato
- - - - -	Parapetto provvisorio su bordo scavo per realizzazione nuovo fabbricato
∿∿∿∿∿	Palancolato provvisorio mediante infissione di palancole metalliche
◩	Quadro elettrico di cantiere
WC	Bagni M/F di cantiere [n. 3] - *Dimensioni 6,10 × 2,40 × 2,30 mt*
▭	Box di cantiere uso UFFICIO [n. 1] - *Dimensioni (L × P × H): 6,00 × 2,40 × 2,40 mt*
▭	Box di cantiere uso SPOGLIATOIO [n. 7] - *Dimensioni (L × P × H): 3,00 × 2,40 × 2,40 mt*
▣	Area destinata a punto di raccolta
➡	Ingresso / uscita di cantiere
➡	Direzione da seguire in caso di emergenza
▤	Cartellone informativo dei lavori
⚠	Cartello di segnalazione: PERICOLO
⚠ ATTENZIONE PERICOLO CADUTA	Cartello di segnalazione: PERICOLO CADUTA DALL'ALTO
⚠ ATTENZIONE PASSAGGIO VEICOLI	Cartello di segnalazione: PERICOLO PASSAGGIO VEICOLI
⛔	Cartello di segnalazione: DIVIETO DI ACCESSO
🚫	Cartello di segnalazione: DIVIETO DI ACCESSO AI NON ADDETTI AI LAVORI
⬆	Cartello di segnalazione: DIREZIONE OBBLIGATORIA
! OBBLIGO DI ESPORRE LA TESSERA DI RICONOSCIMENTO Art. 20 D.Lgs. 81 del 09/04/08	Cartello di segnalazione: CONTROLLO ACCESSI
○	Protezione alberature con gabbia in tavole in legno con interposto materiale cuscinetto

APPROVAZIONE COMMITTENTE	
	A - APPROVATO
	B - APPROVATO CON COMMENTI
	C - NON APPROVATO

Rev.	Data	Descriz.	Red.	Ver.	App.
00	05/10/2026	Prima Emissione			

SCALA

SEDE PROGETTO
VIALE BOSTON 25
Comune di ROMA, RM - 00144

NUMERO PROGETTO
RMB1284

STATO
P

FASE PROGETTUALE:
PFTE

RTP:

Mandataria:	**Mandante:**	**Mandante:**	**Mandante:**	**Mandante:**	**Mandante:**
Progetto strutturale	Progetto architettonico	Progetto architettonico	Progetto impianti	Responsabile progettazione sostenibile dell'oopera	
GPA PARTNERS	PLP/ARCHITECTURE	OBLYK			enser
via Leone X 3 50129 Firenze +39 055 468291 info@gpapartners.com	The White Chapel Building, 10 Whitechapel High Street Londra, E1 8QS, United Kingdom +44 (0)20 3006 3900 info@plparchitecture.com	Via San Vito, 26 20123 Milano, Italia +39 328 841 0677 office@oblyk.studio	Via Cavour, 4 70027 Palo del Colle (BA) +39 080 8594347 info@studioperillo.eu	Via Giuseppe Verdi, 26 63822 Porto San Giorgio (FM) +39 0734674423 info@valentiniarchitetture.com	Via Beccarini, 29 48018 Faenza (RA) +39 0546663423 ingegneria@enser.it

PROGETTO: CIG: B4C1AD81FA CUP: G84H22000360001

Realizzazione della nuova sede del Ministero dell'Ambiente e della Sicurezza Energetica "MASE"

Codice bene: RMB1284
Codice fabbricato: RM0411001

TITOLO

LAYOUT DI CANTIERE - FASE SCAVI, PIANO TERRA, PIANO TIPO, COPERTURA

AGENZIA DEL DEMANIO
Struttura per la progettazione
Via Barberini 38, 00187, Roma
RUP: Arch. Isabella Di Marsico
DEC: Ing. Benedetto Grivo

AGENZIA DEL DEMANIO

NOME FILE
RMB1284-ADD-PLANLIVEL-ZZ-DR-H-PN0001

REV
00
05/10/2026

LAYOUT DI CANTIERE - FASE REALIZZAZIONE PIANO TERRA
Scala 1:200

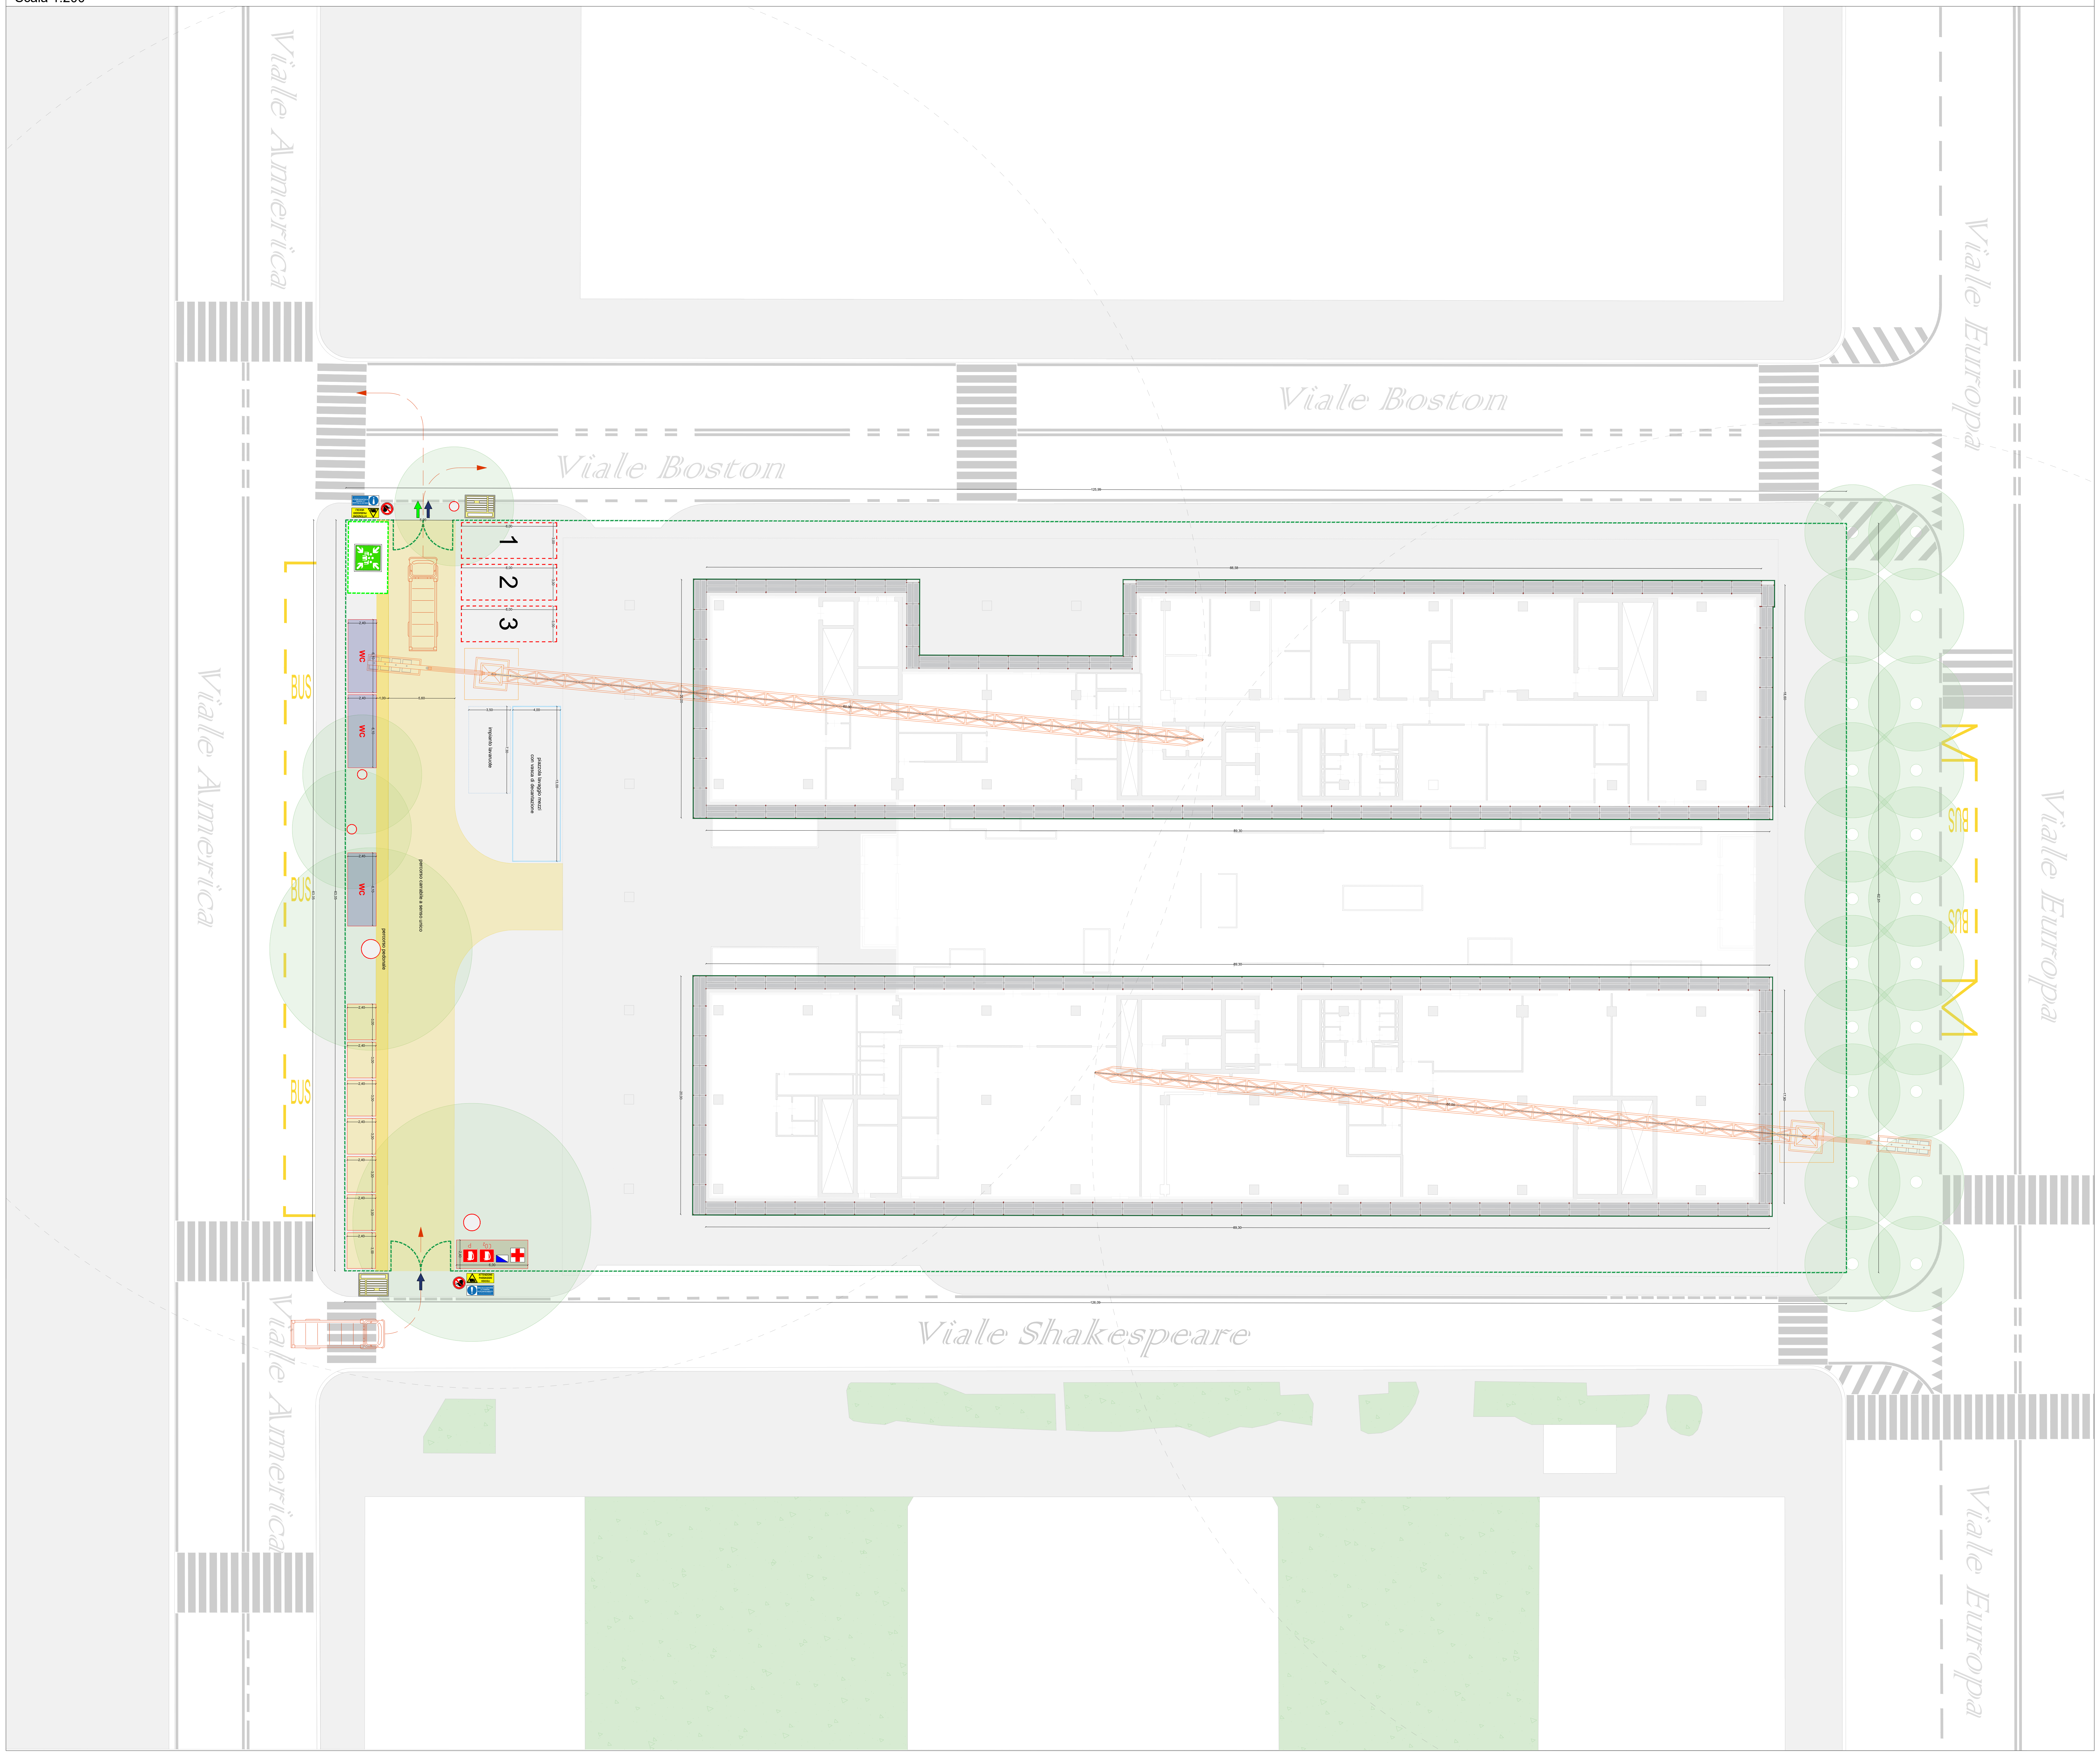

LEGENDA

- - - - - -	Chiusura perimetrale di cantiere - *Pannelli ciechi in legno e metallo per aree urbane, predisposte ad allestimenti pubblicitari o disegni da arredo urbano*
◜	Accesso al cantiere - *Dovrà obbligatoriamente essere dotato di serratura o di lucchetto di sicurezza corazzato con chiave non riproducibile*
◩	Quadro elettrico di cantiere
WC	Bagni M/F di cantiere [n. 3] - *Dimensioni (L × P × H): 6,10 × 2,40 × 2,30 mt*
▭	Box di cantiere uso UFFICIO [n. 1] - *Dimensioni (L × P × H): 6,00 × 2,40 × 2,40 mt*
▭	Box di cantiere uso SPOGLIATOIO [n. 7] - *Dimensioni (L x P x H): 3,00 x 2,40 x 2,40 mt*
▤	Ponteggio metallico a telaio prefabbricato
———	Rete di contenimento polveri per ponteggi
1	Isola ecologica - Tettoia realizzata con elementi tubolari di ponteggio con copertura in tavole di legno
2	Deposito materiali pericolosi - Tettoia realizzata con elementi tubolari di ponteggio con copertura in tavole di legno
3	Isola materiali da posare - Tettoia realizzata con elementi tubolari di ponteggio con copertura in tavole di legno
🟩	Area destinata a punto di raccolta
➡	Ingresso / uscita di cantiere
➡	Direzione da seguire in caso di emergenza
▤	Cartellone informativo dei lavori
⚠	Cartello di segnalazione: PERICOLO
⚠ ATTENZIONE PASSAGGIO VEICOLI	Cartello di segnalazione: PERICOLO PASSAGGIO VEICOLI
🛇	Cartello di segnalazione: DIVIETO DI ACCESSO AI NON ADDETTI AI LAVORI
! OBBLIGO DI ESPORRE LA TESSERA DI RICONOSCIMENTO Art. 20 D.Lgs. 81 del 09/04/08	Cartello di segnalazione: CONTROLLO ACCESSI
○	Protezione alberature con gabbia in tavole in legno con interposto materiale cuscinetto

APPROVAZIONE COMMITTENTE	
	A - APPROVATO
	B - APPROVATO CON COMMENTI
	C - NON APPROVATO

Rev.	Data	Descriz.	Red.	Ver.	App.
00	05/10/2026	Prima Emissione			

SCALA

SEDE PROGETTO
VIALE BOSTON 25
Comune di ROMA, RM - 00144

NUMERO PROGETTO
RMB1284

STATO
P

FASE PROGETTUALE:
PFTE

RTP:

Mandataria:
Progetto strutturale
GPA PARTNERS
via Leone X 3
50129 Firenze
+39 055 468291
info@gpapartners.com

Mandante:
Progetto architettonico
PLP/ARCHITECTURE
The White Chapel Building, 10
Whitechapel High Street Londra, E1 8QS,
United Kingdom
+44 (0)20 3006 3900
info@plparchitecture.com

Mandante:
Progetto architettonico
OBLYK
Via San Vito, 26
20123 Milano, Italia
+39 328 841 0677
office@oblyk.studio

Mandante:
Progetto impianti
Via Cavour, 4
70027 Palo del Colle (BA)
+39 080 8594347
info@studioperillo.eu

Mandante:
Responsabile progettazione sostenibile dell'oopera
Via Giuseppe Verdi, 26
63822 Porto San Giorgio (FM)
+39 0734674423
info@valentiniarchitetture.com

Mandante:
enser
Via Beccarini, 29
48018 Faenza (RA)
+39 0546663423
ingegneria@enser.it

PROGETTO:
CIG: B4C1AD81FA CUP: G84H22000360001

Realizzazione della nuova sede del Ministero dell'Ambiente e della Sicurezza Energetica "MASE"

Codice bene: RMB1284
Codice fabbricato: RM0411001

TITOLO

LAYOUT DI CANTIERE - FASE SCAVI, PIANO TERRA, PIANO TIPO, COPERTURA

AGENZIA DEL DEMANIO
Struttura per la progettazione
Via Barberini 38, 00187, Roma
RUP: Arch. Isabella Di Marsico
DEC: Ing. Benedetto Grivo

AGENZIA DEL DEMANIO

NOME FILE
RMB1284-ADD-PLANLIVEL-ZZ-DR-H-PN0001

REV
00
05/10/2026

LEGENDA

▨	Ponteggio metallico a telaio prefabbricato
—	Rete di contenimento polveri per ponteggi

LAYOUT DI CANTIERE - FASE REALIZZAZIONI PIANO TIPO
Scala 1:200

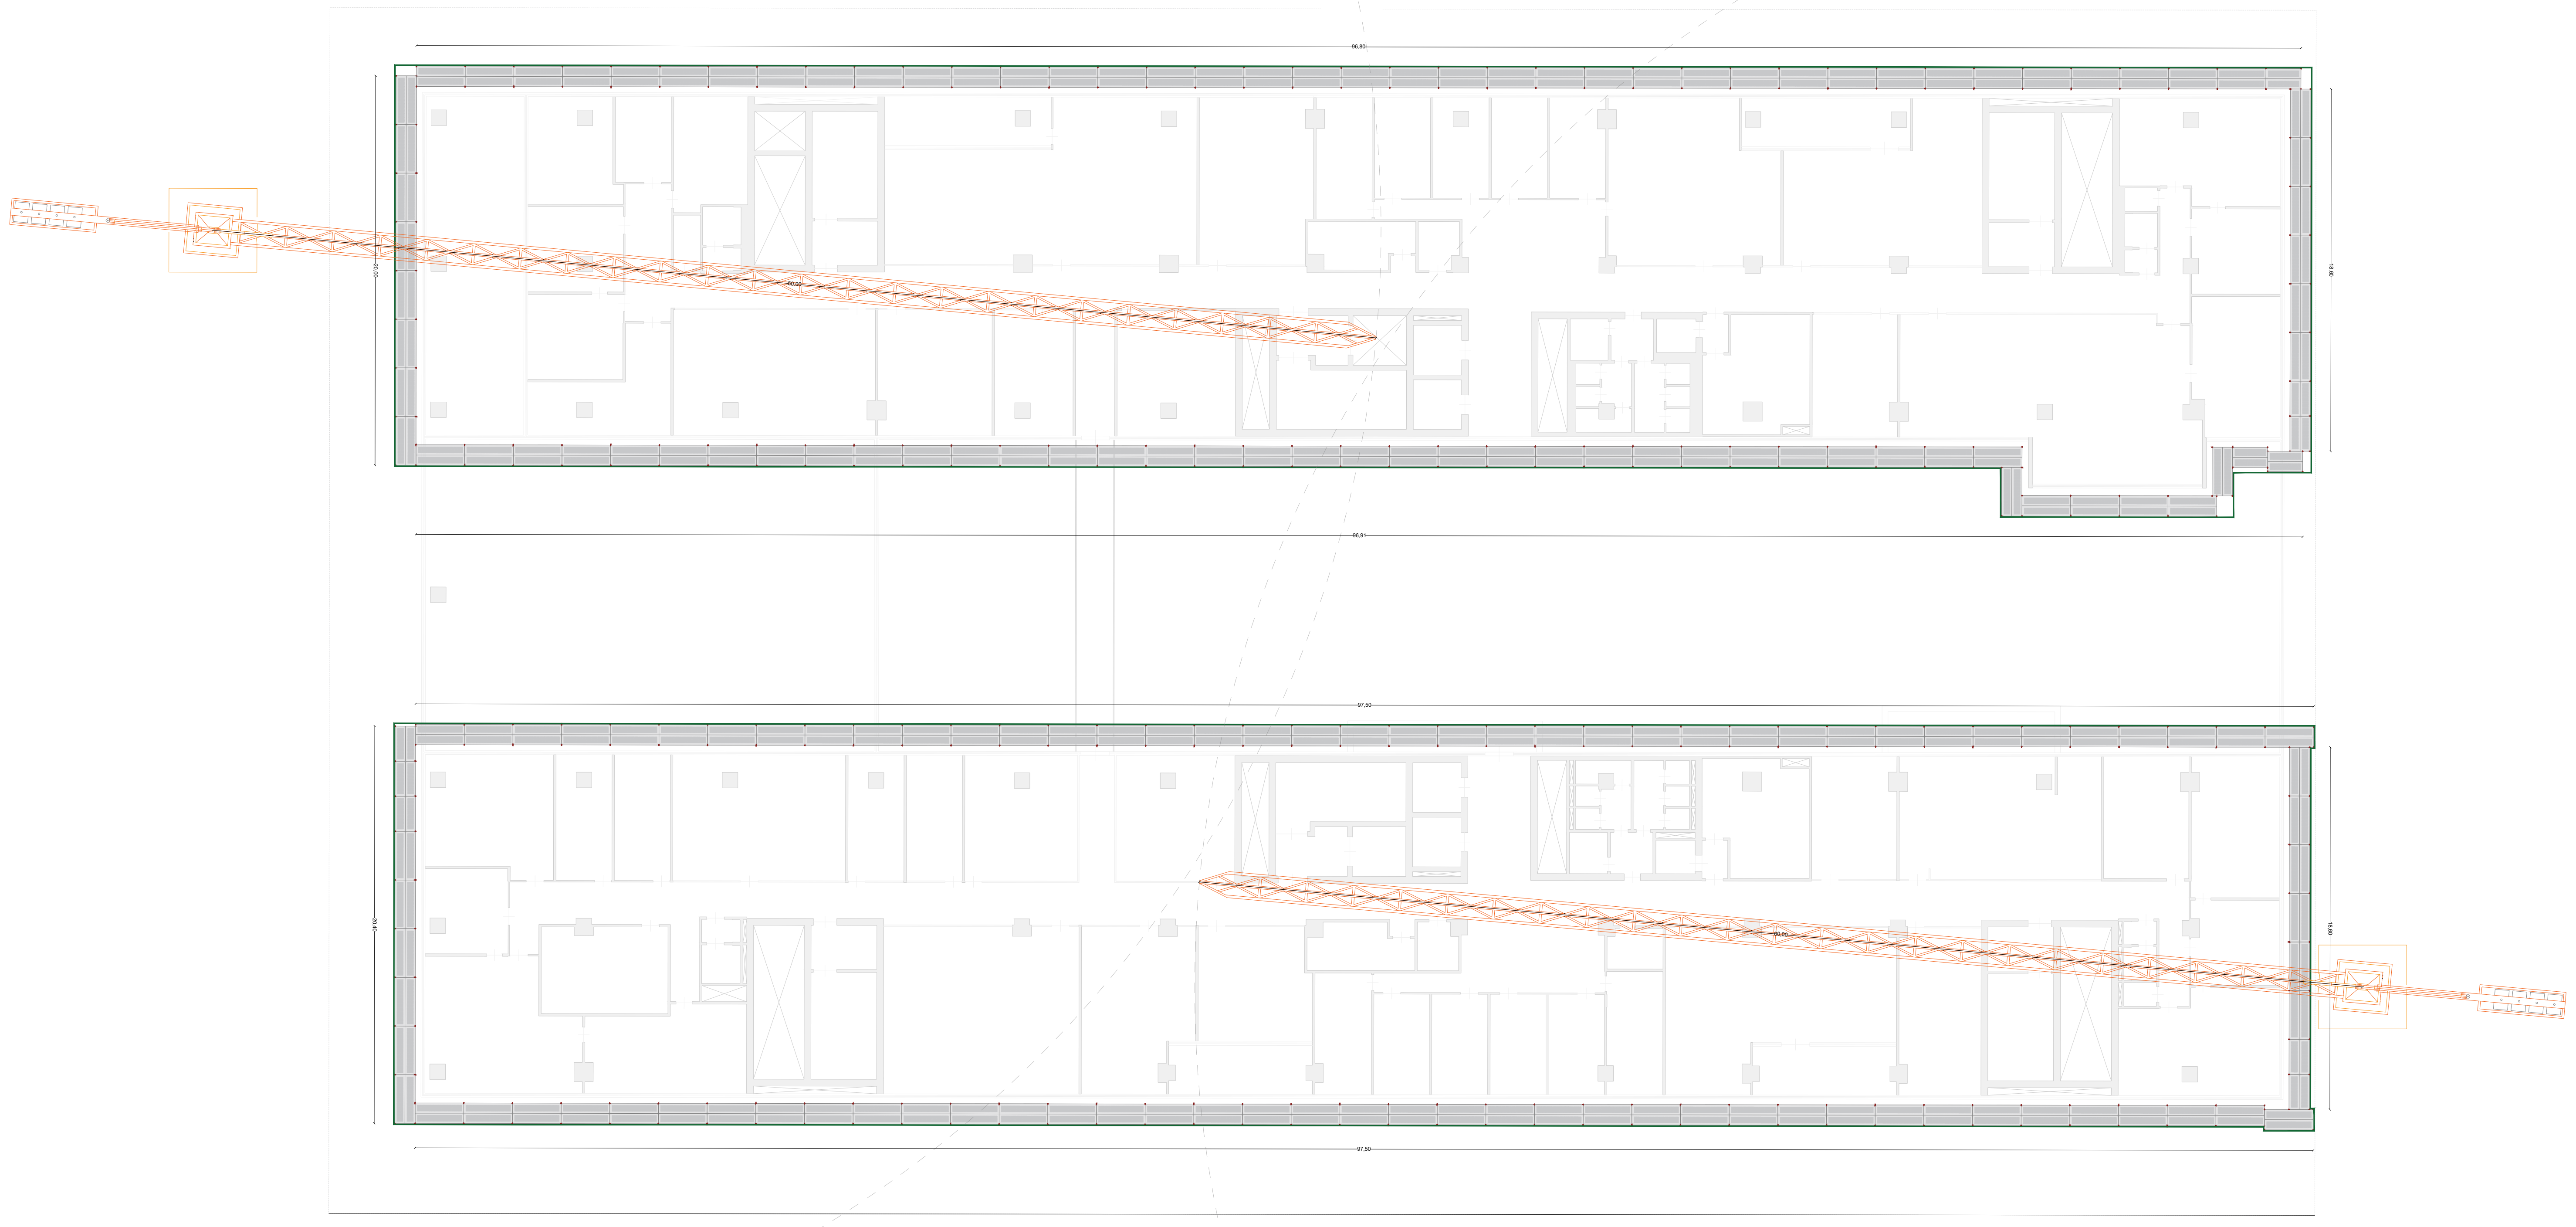

APPROVAZIONE COMMITTENTE	
	A - APPROVATO
	B - APPROVATO CON COMMENTI
	C - NON APPROVATO

Rev.	Data	Descriz.	Red.	Ver.	App.
00	05/10/2026	Prima Emissione			

SCALA

SEDE PROGETTO
VIALE BOSTON 25
Comune di ROMA, RM - 00144

NUMERO PROGETTO
RMB1284

STATO
P

FASE PROGETTUALE:
PFTE

RTP:

Mandataria:	**Mandante:**	**Mandante:**	**Mandante:**	**Mandante:**	**Mandante:**
Progetto strutturale	Progetto architettonico	Progetto architettonico	Progetto impianti	Responsabile progettazione sostenibile dell'oopera	
GPA PARTNERS	PLP/ARCHITECTURE	OBLYK			enser
via Leone X 3 50129 Firenze +39 055 468291 info@gpapartners.com	The White Chapel Building, 10 Whitechapel High Street Londra, E1 8QS, United Kingdom +44 (0)20 3006 3900 info@plparchitecture.com	Via San Vito, 26 20123 Milano, Italia +39 328 841 0677 office@oblyk.studio	Via Cavour, 4 70027 Palo del Colle (BA) +39 080 8594347 info@studioperillo.eu	Via Giuseppe Verdi, 26 63822 Porto San Giorgio (FM) +39 0734674423 info@valentiniarchitetture.com	Via Beccarini, 29 48018 Faenza (RA) +39 0546663423 ingegneria@enser.it

PROGETTO: CIG: B4C1AD81FA CUP: G84H22000360001

Realizzazione della nuova sede del Ministero dell'Ambiente e della Sicurezza Energetica
“MASE”

Codice bene: RMB1284
Codice fabbricato: RM0411001

TITOLO

LAYOUT DI CANTIERE - FASE SCAVI, PIANO TERRA, PIANO TIPO, COPERTURA

AGENZIA DEL DEMANIO
Struttura per la progettazione
Via Barberini 38, 00187, Roma
RUP: Arch. Isabella Di Marsico
DEC: Ing. Benedetto Grivo

AGENZIA DEL DEMANIO

NOME FILE
RMB1284-ADD-PLANLIVEL-ZZ-DR-H-PN0001

REV
00
05/10/2026

LEGENDA	
▨	Ponteggio metallico a telaio prefabbricato
───	Rete di contenimento polveri per ponteggi
───	Rete anticaduta per parapetto di sommità del ponteggio
– – – –	Parapetto provvisorio a montanti prefabbricati (guardacorpo)

LAYOUT DI CANTIERE - FASE REALIZZAZIONE PIANO COPERTURA

Scala 1:200

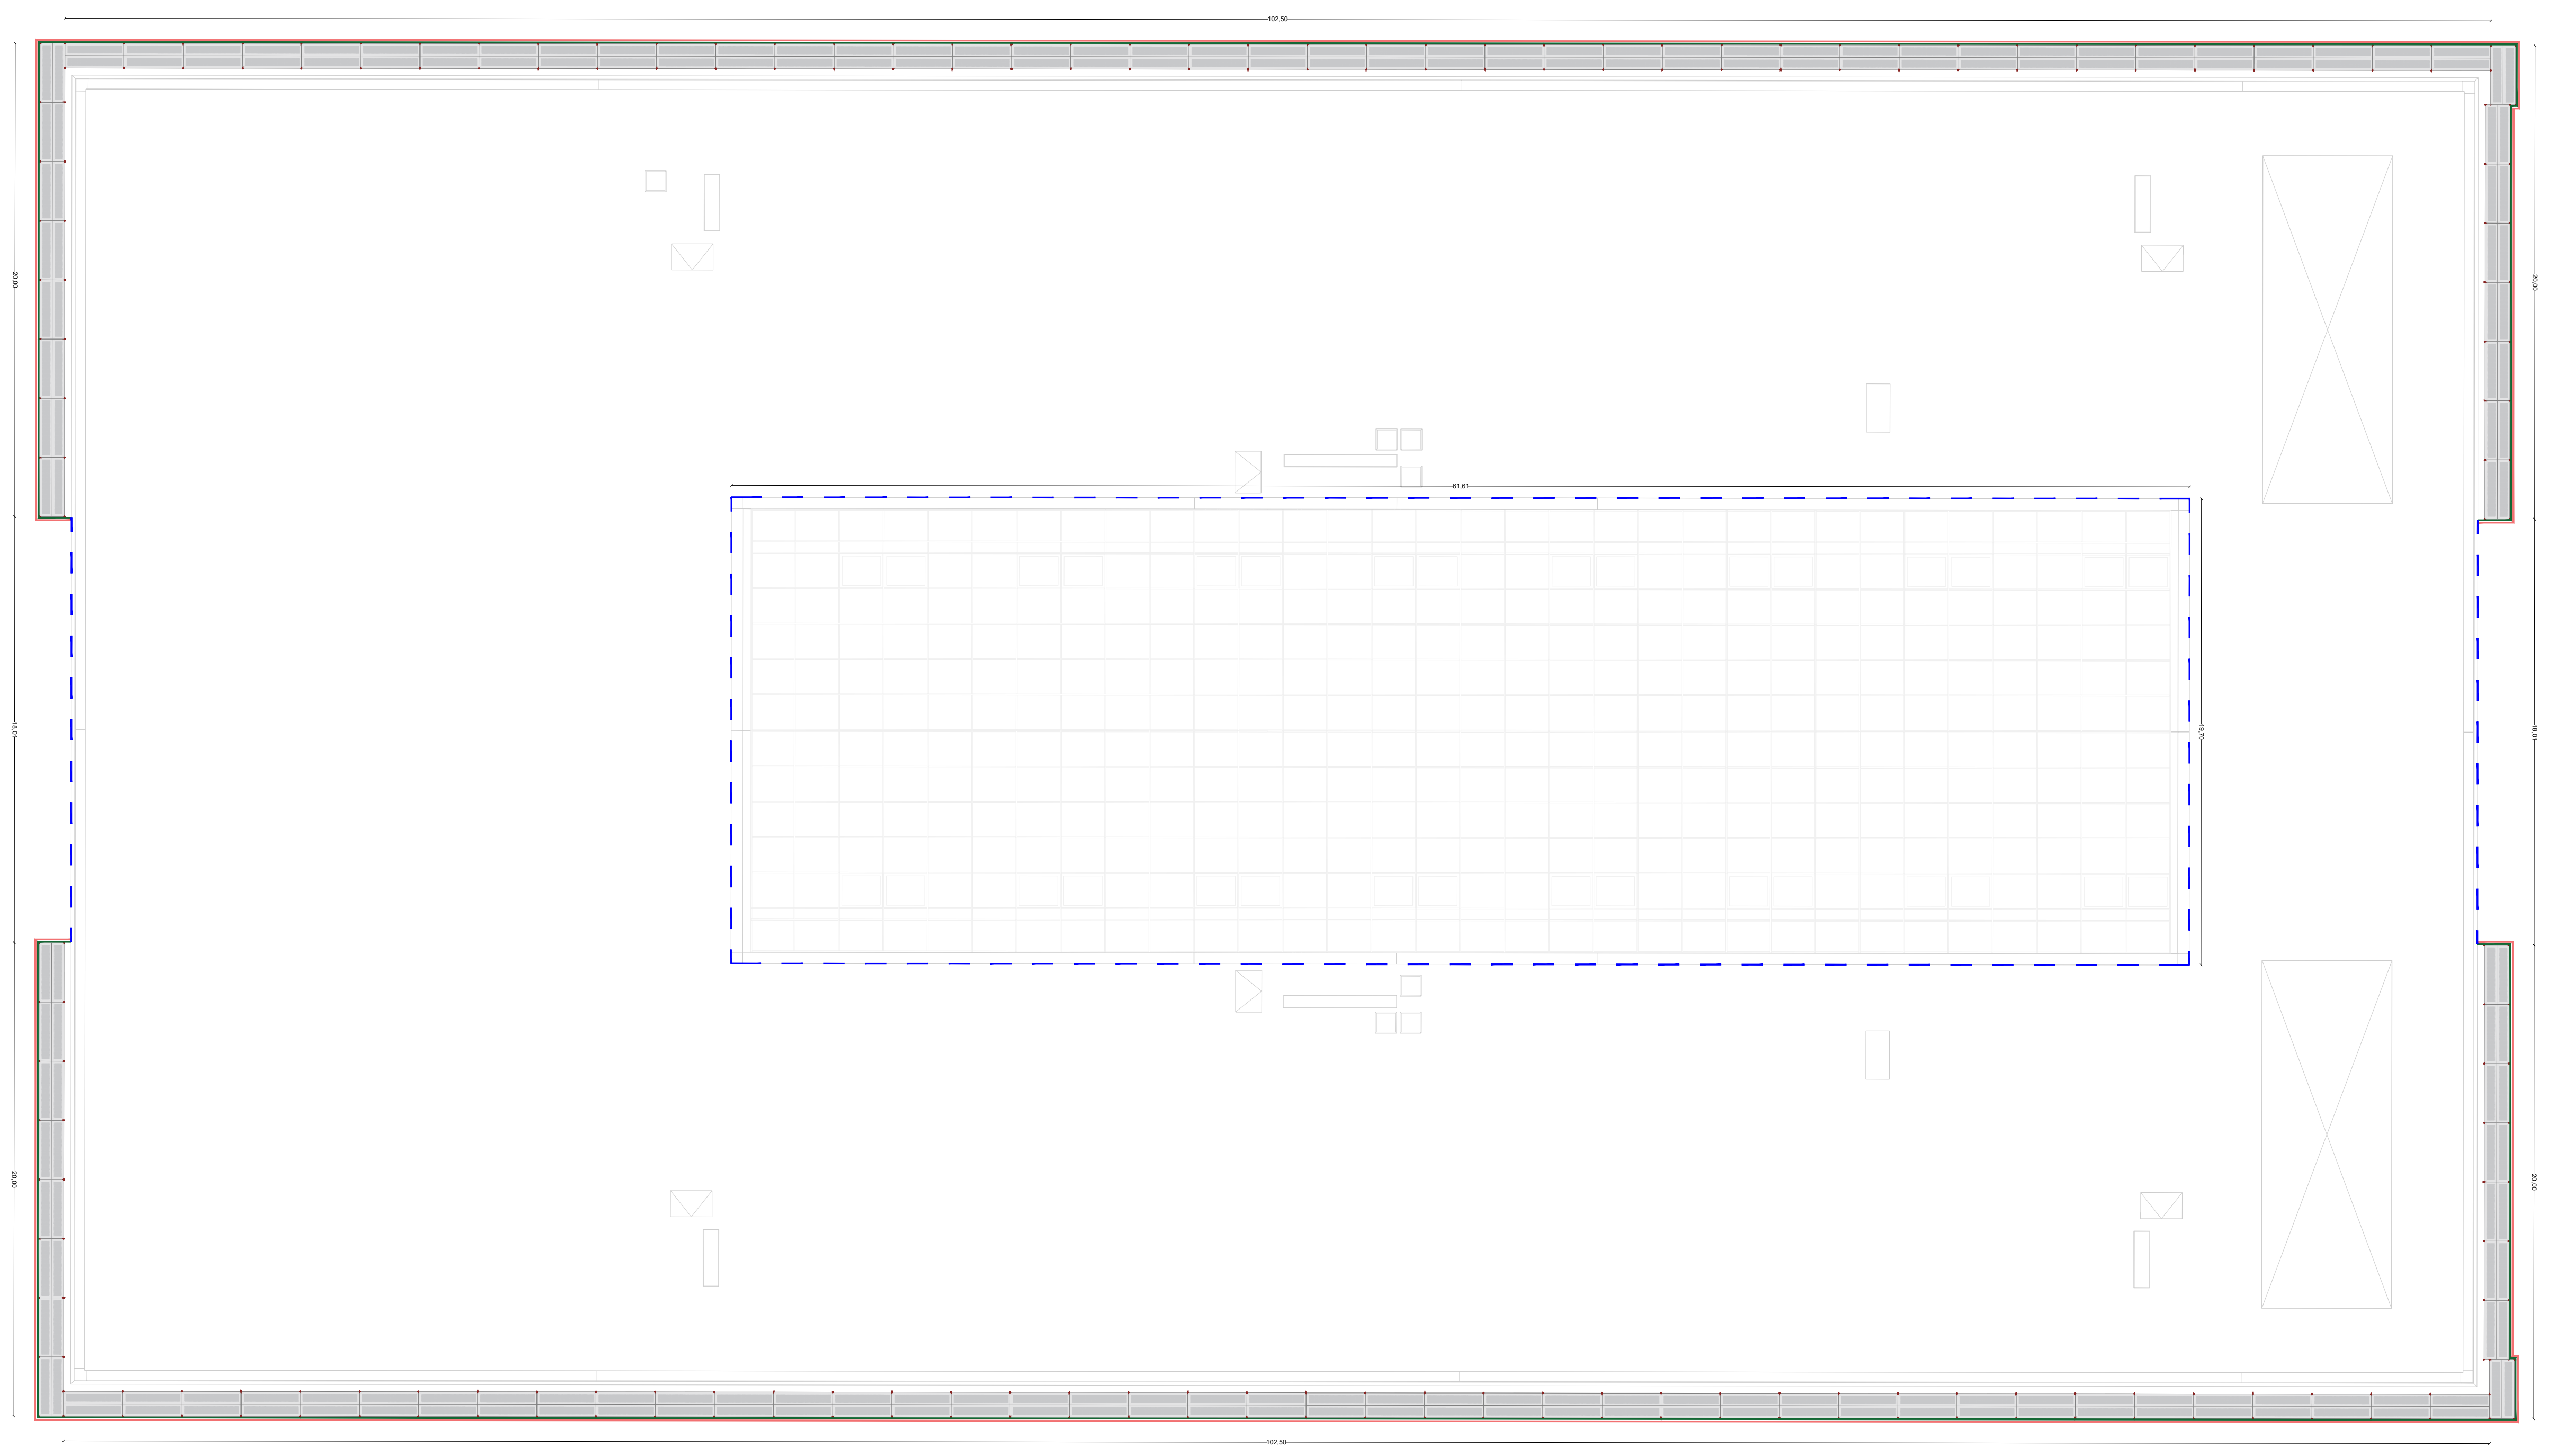

APPROVAZIONE COMMITTENTE	
	A - APPROVATO
	B - APPROVATO CON COMMENTI
	C - NON APPROVATO

Rev.	Data	Descriz.	Red.	Ver.	App.
00	05/10/2026	Prima Emissione			

SCALA

SEDE PROGETTO
VIALE BOSTON 25
Comune di ROMA, RM - 00144

NUMERO PROGETTO
RMB1284

STATO
P

FASE PROGETTUALE:
PFTE

RTP:

Mandataria:	**Mandante:**	**Mandante:**	**Mandante:**	**Mandante:**	**Mandante:**
Progetto strutturale	Progetto architettonico	Progetto architettonico	Progetto impianti	Responsabile progettazione sostenibile dell'oopera	
GPA PARTNERS	PLP/ARCHITECTURE	OBLYK			enser
via Leone X 3 50129 Firenze +39 055 468291 info@gpapartners.com	The White Chapel Building, 10 Whitechapel High Street Londra, E1 8QS, United Kingdom +44 (0)20 3006 3900 info@plparchitecture.com	Via San Vito, 26 20123 Milano, Italia +39 328 841 0677 office@oblyk.studio	Via Cavour, 4 70027 Palo del Colle (BA) +39 080 8594347 info@studioperillo.eu	Via Giuseppe Verdi, 26 63822 Porto San Giorgio (FM) +39 0734674423 info@valentiniarchitetture.com	Via Beccarini, 29 48018 Faenza (RA) +39 0546663423 ingegneria@enser.it

PROGETTO: CIG: B4C1AD81FA CUP: G84H22000360001

Realizzazione della nuova sede del Ministero dell'Ambiente e della Sicurezza Energetica
“MASE”

Codice bene: RMB1284
Codice fabbricato: RM0411001

TITOLO

LAYOUT DI CANTIERE - FASE SCAVI, PIANO TERRA, PIANO TIPO, COPERTURA

AGENZIA DEL DEMANIO
Struttura per la progettazione
Via Barberini 38, 00187, Roma
RUP: Arch. Isabella Di Marsico
DEC: Ing. Benedetto Grivo

AGENZIA DEL DEMANIO

NOME FILE
RMB1284-ADD-PLANLIVEL-ZZ-DR-H-PN0001

REV
00
05/10/2026